

LEGEND	
EXISTING	
STRUCTURE	MANHOLE/SANITARY SEWER STRUCTURE
ELECTRICAL	TELECOMMUNICATION
WATER PIPE	PEDESTAL
STORM SEWER	WATER VALVE
SANITARY SEWER	LIGHT POLE
GAS PIPE	TURF DEMO
FENCE	BRICK PAVERS DEMO
SIGN	GRAVEL PATH DEMO
TREE	CLEANING AND GRUBBING
TREE/BRUSH LINE	

1 DEMOLITION PLAN


SCALE 1" = 10'

DEMOLITION SCHEDULE	
SYMBOL	DESCRIPTION
D-01	EX. BRICK PAVERS OR DECOMPOSED GRANITE - REMOVE AND SALVAGE BRICKS FOR REUSE, DECOMPOSED GRANITE REMOVE & DISPOSE
D-02	EX. TURF REMOVE AND DISPOSE
D-03	EX. GRAVEL REMOVE AND DISPOSE
D-04	EX. SANITARY MANHOLE TO BE ADJUSTED TO NEW GRADE, REMOVE AND SALVAGE COVER, RINGS, AND FRAME FOR REUSE.
D-05	EX. TREE - REMOVE AND DISPOSE
D-06	LIMIT OF DISTURBANCE
D-07	SILT FENCE

NOTES:

- CONTRACTOR SHALL MINIMIZE LIMITS OF CONSTRUCTION FENCE EXCEPT DURING RESTORATION, MOVE AND EXPAND CONSTRUCTION FENCE LIMITS AS REQUIRED TO COMPLETE RESTORATION AND GRADING OF THE PROJECT AREA.
- CONTRACTOR SHALL AVOID DAMAGING TREES OUTSIDE LIMIT OF DISTURBANCE THAT ARE NOT SCHEDULED FOR REMOVAL.
- COORDINATE WORK TO MAINTAIN AT LEAST ONE ACCESS PATH TO CLAUSING BARN AT ALL TIMES.

Graphic Scale	0' 2.5' 5' 10' 15'
DDF Number	1711K-04
Set Type	BD
Date Issued	9/8/2023
Sheet Number	C102

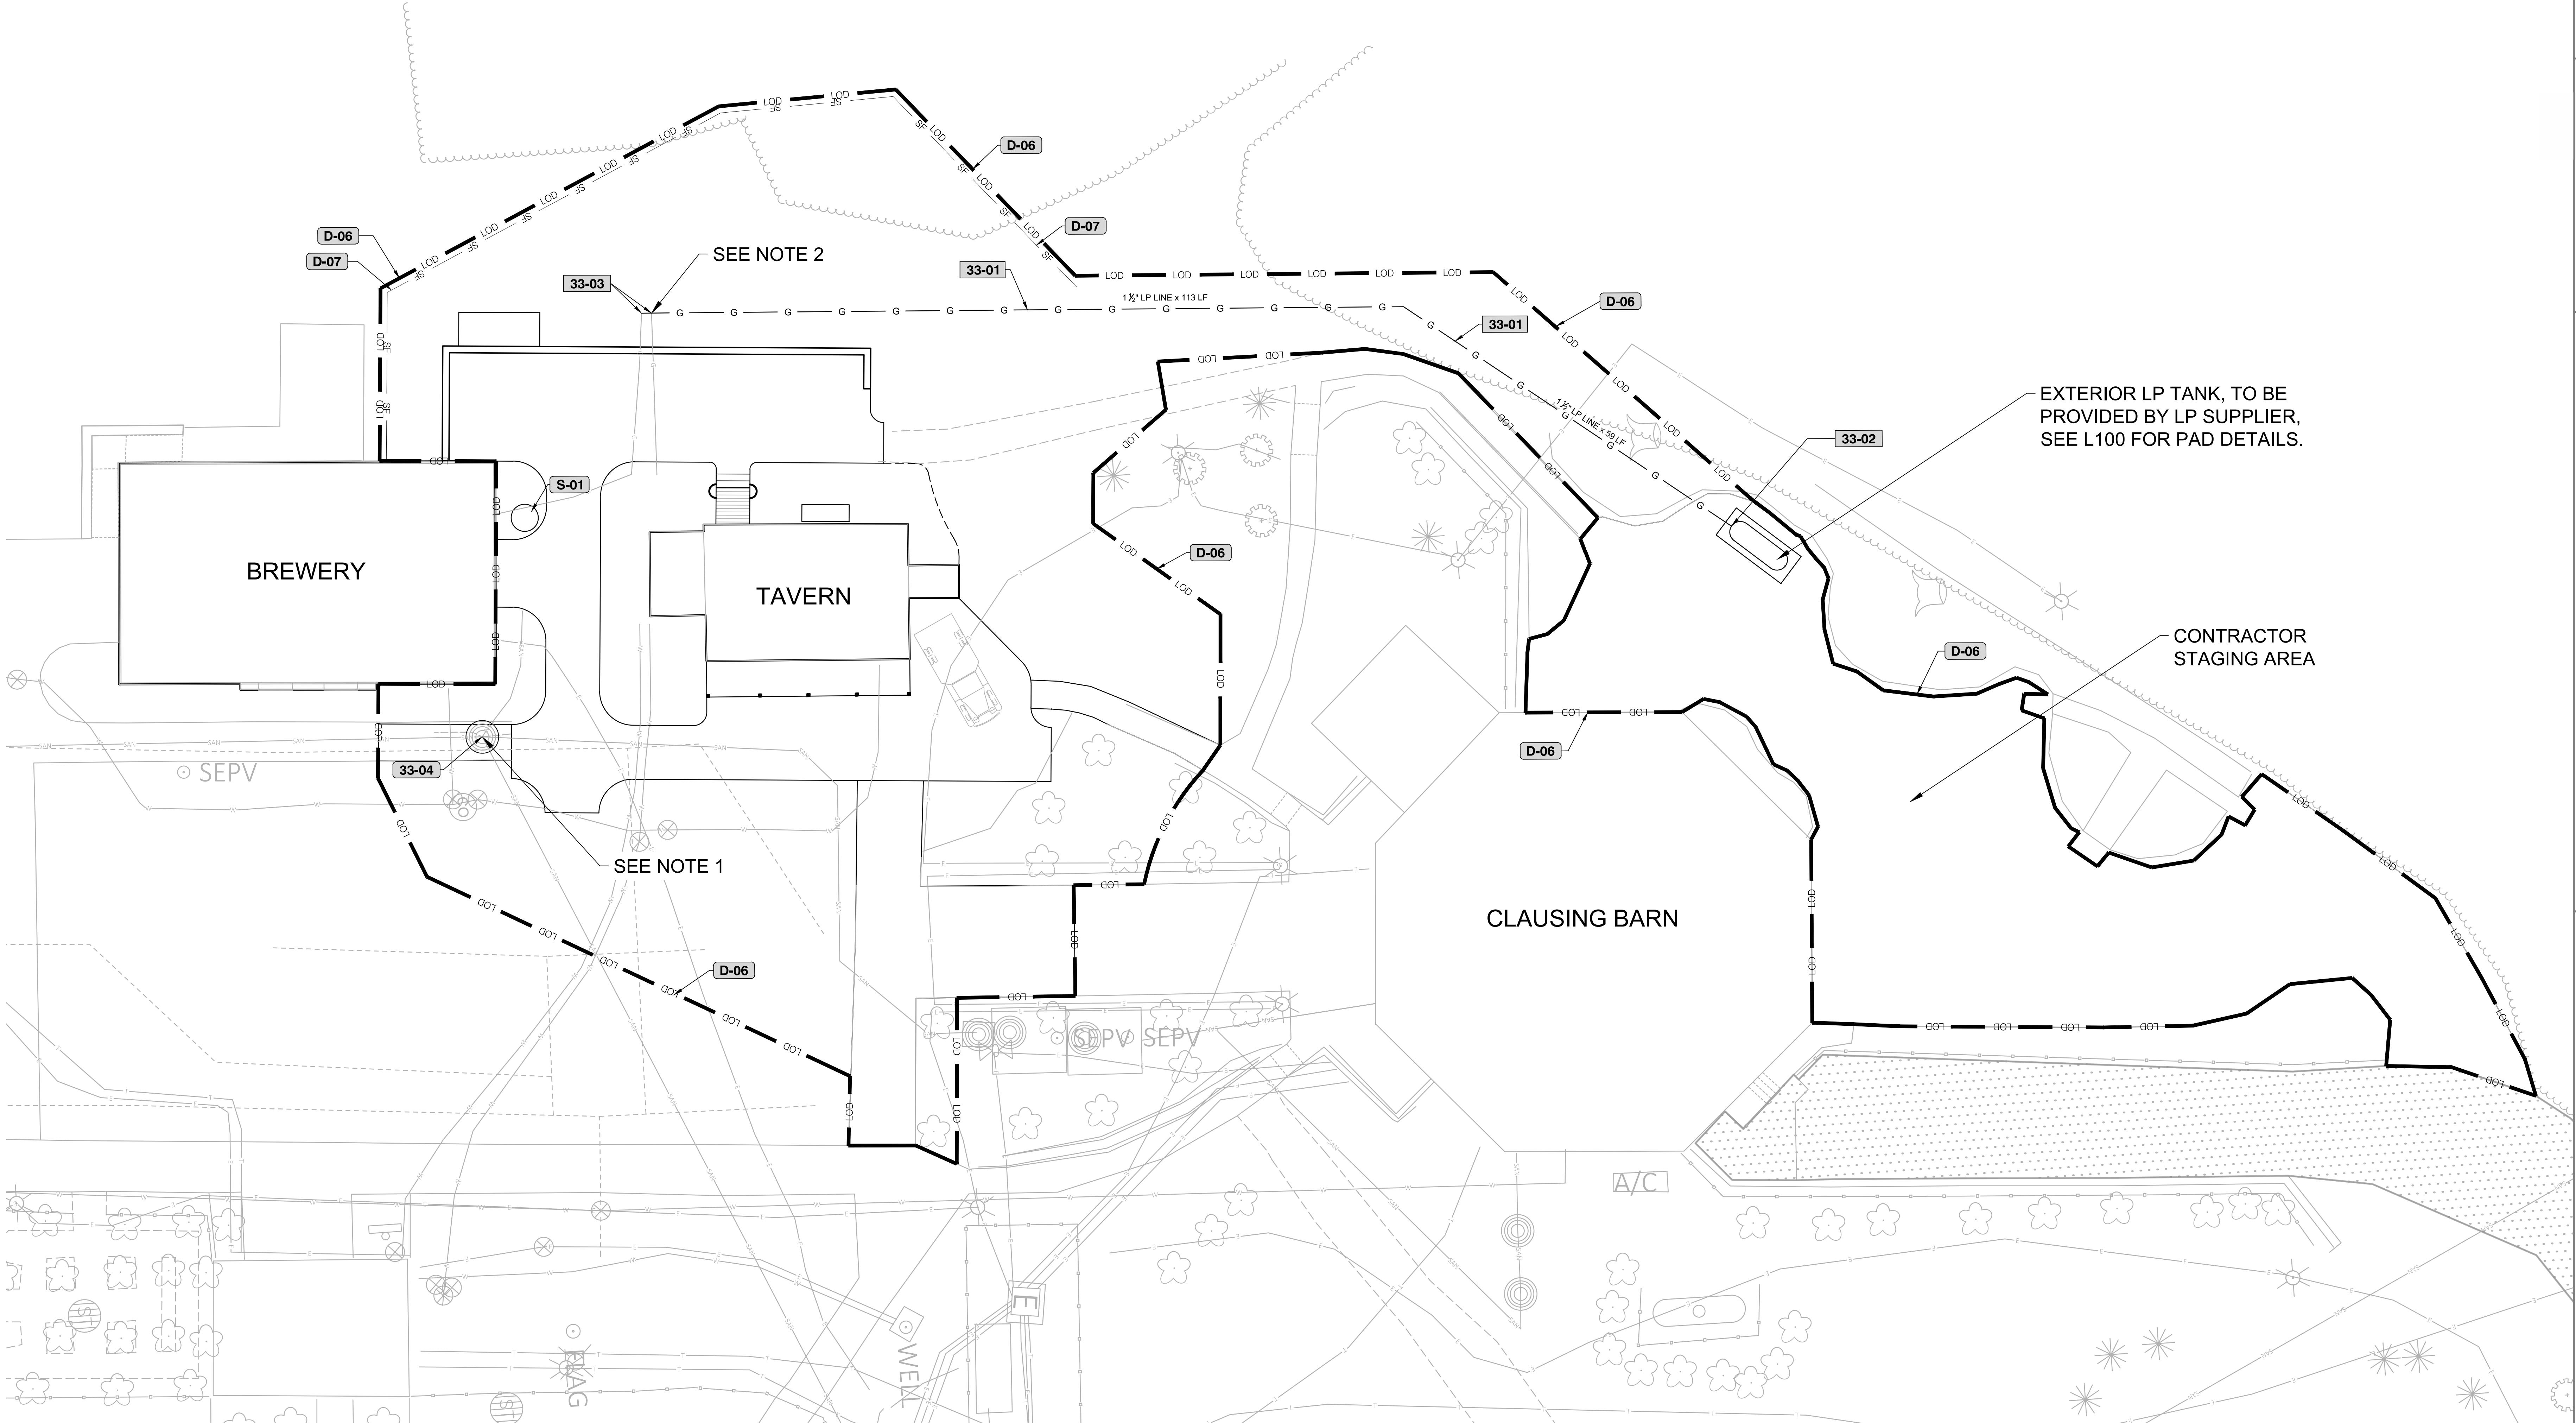

LEGEND	
EXISTING	
STRUCTURE	□
ELECTRICAL	E
WATER PIPE	W
STORM SEWER	SD
SANITARY SEWER	SAN
GAS PIPE	G
FENCE	—
SIGN	■
TREE	★
TREE/BRUSH LINE	~~~~~
MANHOLE/SANITARY SEWER STRUCTURE	◎
TELECOMMUNICATION	●
PEDESTAL	●
WATER VALVE	●VV
LIGHT POLE	★

1 PROPOSED LP GAS PLAN
SCALE 1' = 10'

REFERENCE NOTES SCHEDULE

33 Utilities	
SYMBOL	DESCRIPTION
(33-01)	NEW LP GAS LINE
(33-02)	CONNECT AT LP TANK
(33-03)	CONNECT TO EXISTING STUBS
(33-04)	SANITARY MANHOLE - REPLACE ADJUSTING RINGS, FRAME, AND COVER AND ADJUST TO MATCH PROPOSED GRADE.
(D-06)	LIMIT OF DISTURBANCE
(D-07)	SILT FENCE
(S-01)	Site Furnishings
SYMBOL	DESCRIPTION
(S-01)	KING GAMBRINUS STATUE- OWNER FURNISHED SEE L100

NOTES:

1. SEE SHEET L101 FOR PROPOSED GRADING AND DETAILS ON REPLACEMENT.
2. PROVIDE ALL NECESSARY FITTINGS AT CONNECTION TO EXISTING STUBS AND AS SPECIFIED IN SECTION 33-04 DD.

Graphic Scale	0' 2.5' 5' 10' 15'
DDF Number	1711K-04
Set Type	BD
Date Issued	9/8/2023
Sheet Number	C201

FIGURE GROUND

jporter@figureground-design.com

608-345-5101

NOTES:

1. UPDATED SURVEY PROVIDED BY ONEIDA ENGINEERING SOLUTIONS ON 06/26/2023.
2. ALL HORIZONTAL MEASUREMENTS AND COORDINATES ARE BASED ON THE WISCONSIN COUNTY COORDINATE SYSTEM - WAUKESHA ZONE.
3. ALL ELEVATIONS AND CONTOURS ARE NAVD88.
4. ALL SITE WORK SHALL CONFORM TO CURRENT STATE OF WISCONSIN DEPARTMENT OF ADMINISTRATION MASTER SPECIFICATIONS AND DESIGN GUIDELINES.
5. ALL SIGNAGE AND SITE FURNISHINGS SHALL BE PROVIDED BY THE OWNER.
6. CONTRACTOR SHALL REPORT ANY ERRORS, OMISSIONS OR DISCREPANCIES IN DRAWINGS AND/OR SURVEYED FIELD CONDITIONS PRIOR TO CONSTRUCTION.
7. CALL DIGGERS HOTLINE PRIOR TO CONSTRUCTION AT 800-242-8511.
8. CONTRACTOR SHALL FIELD STAKE THE LOCATION OF ALL SITE WORK FOR REVIEW AND APPROVAL BY OWNER'S REP. PRIOR TO CONSTRUCTION.
9. NO PARKING OF VEHICLES, HEAVY MACHINERY OR STORAGE ON LANDSCAPED AREAS OR WITHIN DRIP LINES OF TREES.
10. ALL DISTURBED AREAS OUTSIDE OF DESIGNATED PLANT BEDS SHALL BE SEDED WITH GRASS MIX UNLESS SPECIFIED OTHERWISE.
11. PLANT BEDS SHALL BE IRRIGATED. CONNECT TO EXISTING IRRIGATION SYSTEM AND STUB NEW LINES TO ALLOW FOR FUTURE EXPANSION.
12. ALL PLANTS WITHIN PROPOSED PLANTING BEDS BY OTHERS.

LEGEND:

	LIMIT OF WORK
	EXISTING PLANTS (TO REMAIN)
	EXISTING CONTOURS
	PROPOSED CONTOURS
	C.I.P. CONCRETE 1 L500
	C.I.P. CONCRETE - EXPOSED AGGREGATE FINISH 1 L500
	TEMPORARY COMPACTED AGGREGATE WEARING SURFACE. PROVIDE 6 INCHES OF COMPACTED 3/4-INCH CRUSHED STONE OR GRAVEL CONFORMING TO WISDOT SECTION 305.2.
	WOOD DECKING SURFACE - SEE ARCHITECTURE DRAWINGS.
	PROPOSED PLANTING BEDS (SHRUBS AND PERENNIALS WITH 18" OF GROWING MEDIUM AND 3" OF SHREDDED HARDWOOD BARK MULCH).
	SEEDED GRASS MIX (TOPDRESS WITH 3" OF GROWING MEDIUM).
	EXISTING BRICK PAVERS TO BE SALVAGED AND REINSTALLED IN-KIND.
	EXISTING GRAVEL PATH TO BE REPLACED IN-KIND.
	EXISTING LANDSCAPE TO SALVAGED AND REINSTALLED OR REPLACED IN-KIND BY OWN.
	CONTROL JOINT 1 L500
	VERIFY (MEASUREMENT) IN FIELD
	CENTERLINE

State of Wisconsin
Department of Administration
Division of Facilities Development



Tavern Renovations
Old World Wisconsin Ethnic Outdoor Museum
Wisconsin Historical Society
Town of Eagle, Wisconsin

Sheet title:
TAVERN LAYOUT PLAN


Revisions:		
No.	Date:	Description:

Graphic	0'	2.5'	10'	15'
DFD Number	1711K-04			
Set Type	BD			
Date Issued	9/8/2023			
Sheet Number	L100			

A/C


NORTH

Sheet title:
TAVERN LAYOUT PLAN

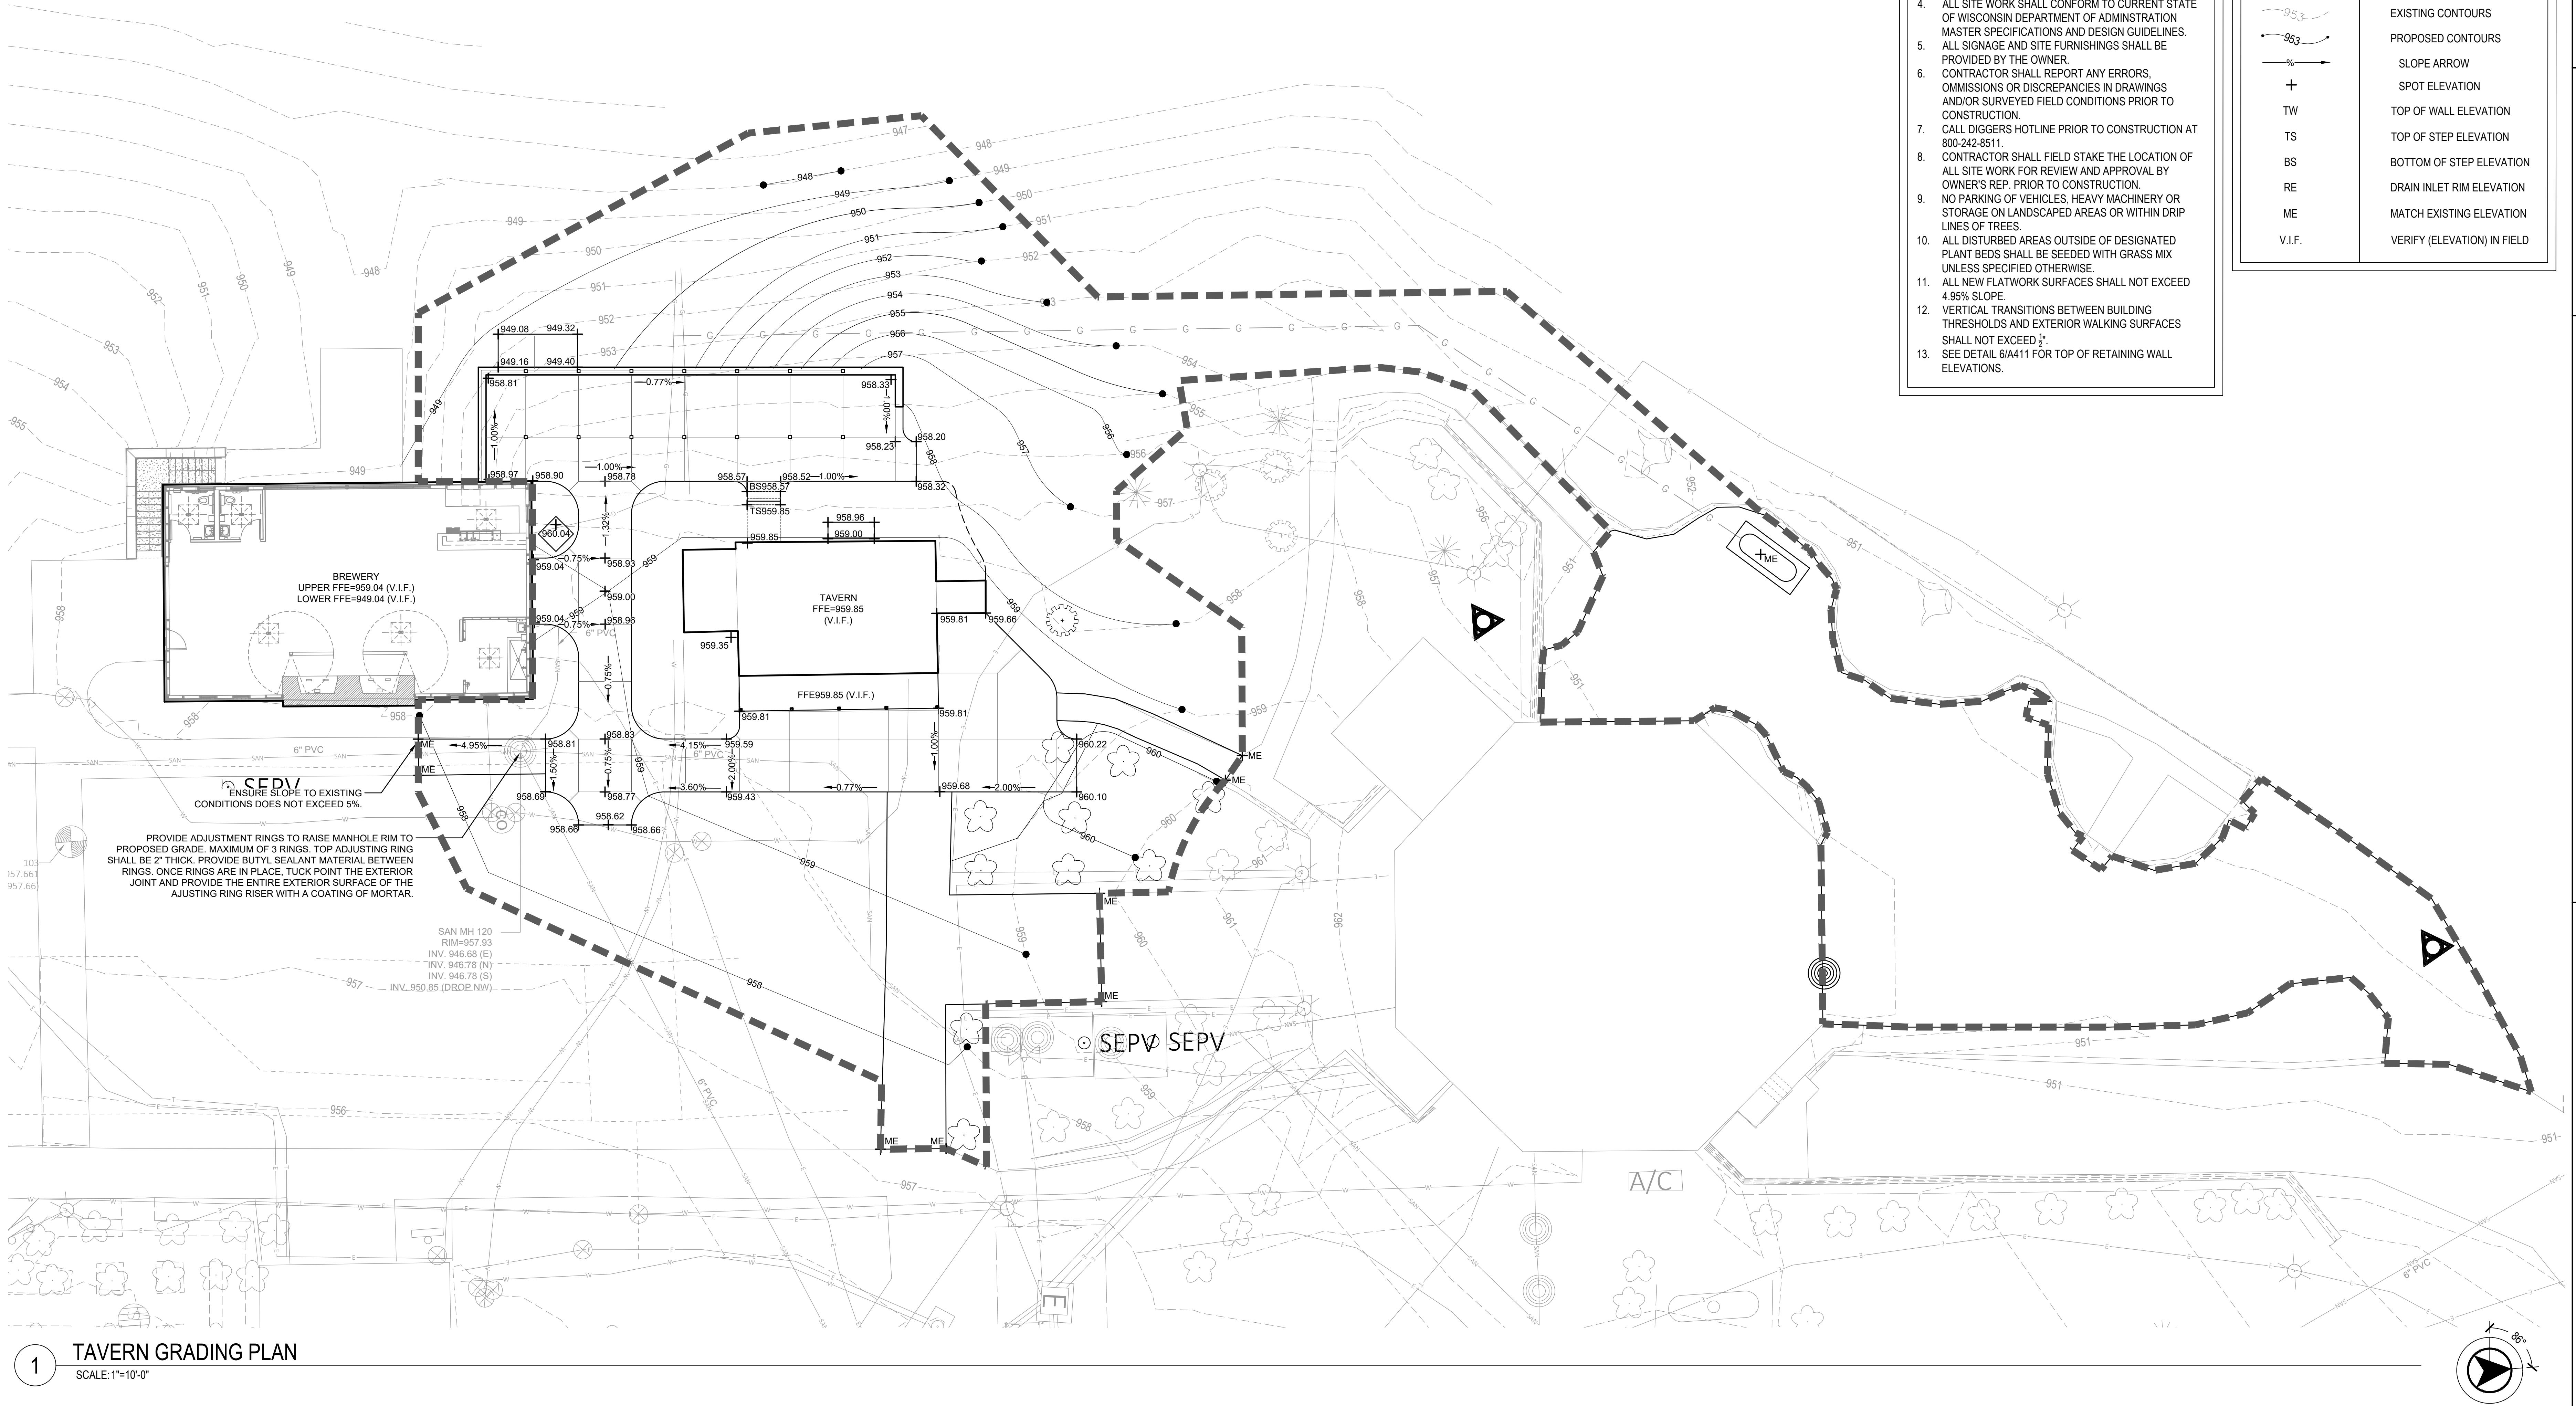

ARO EBERLE ARCHITECTS
433 W. Washington Av (608) 204-7464
Suite 400
Madison, WI 53703
AroEberle.com



State of Wisconsin
Department of Administration
Division of Facilities Development

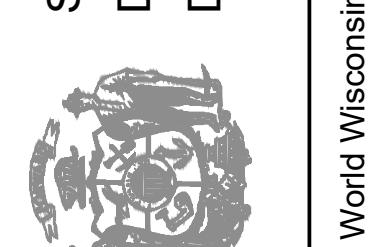

Old World Wisconsin Ethnic Outdoor Museum
Town of Eagle, Wisconsin


Revisions:
No. _____ Date: _____ Description: _____

Graphic Scale: 0' 2.5' 10' 15'
DFD Number: 1711K-04
Set Type: BD
Date Issued: 9/8/2023
Sheet Number: L101

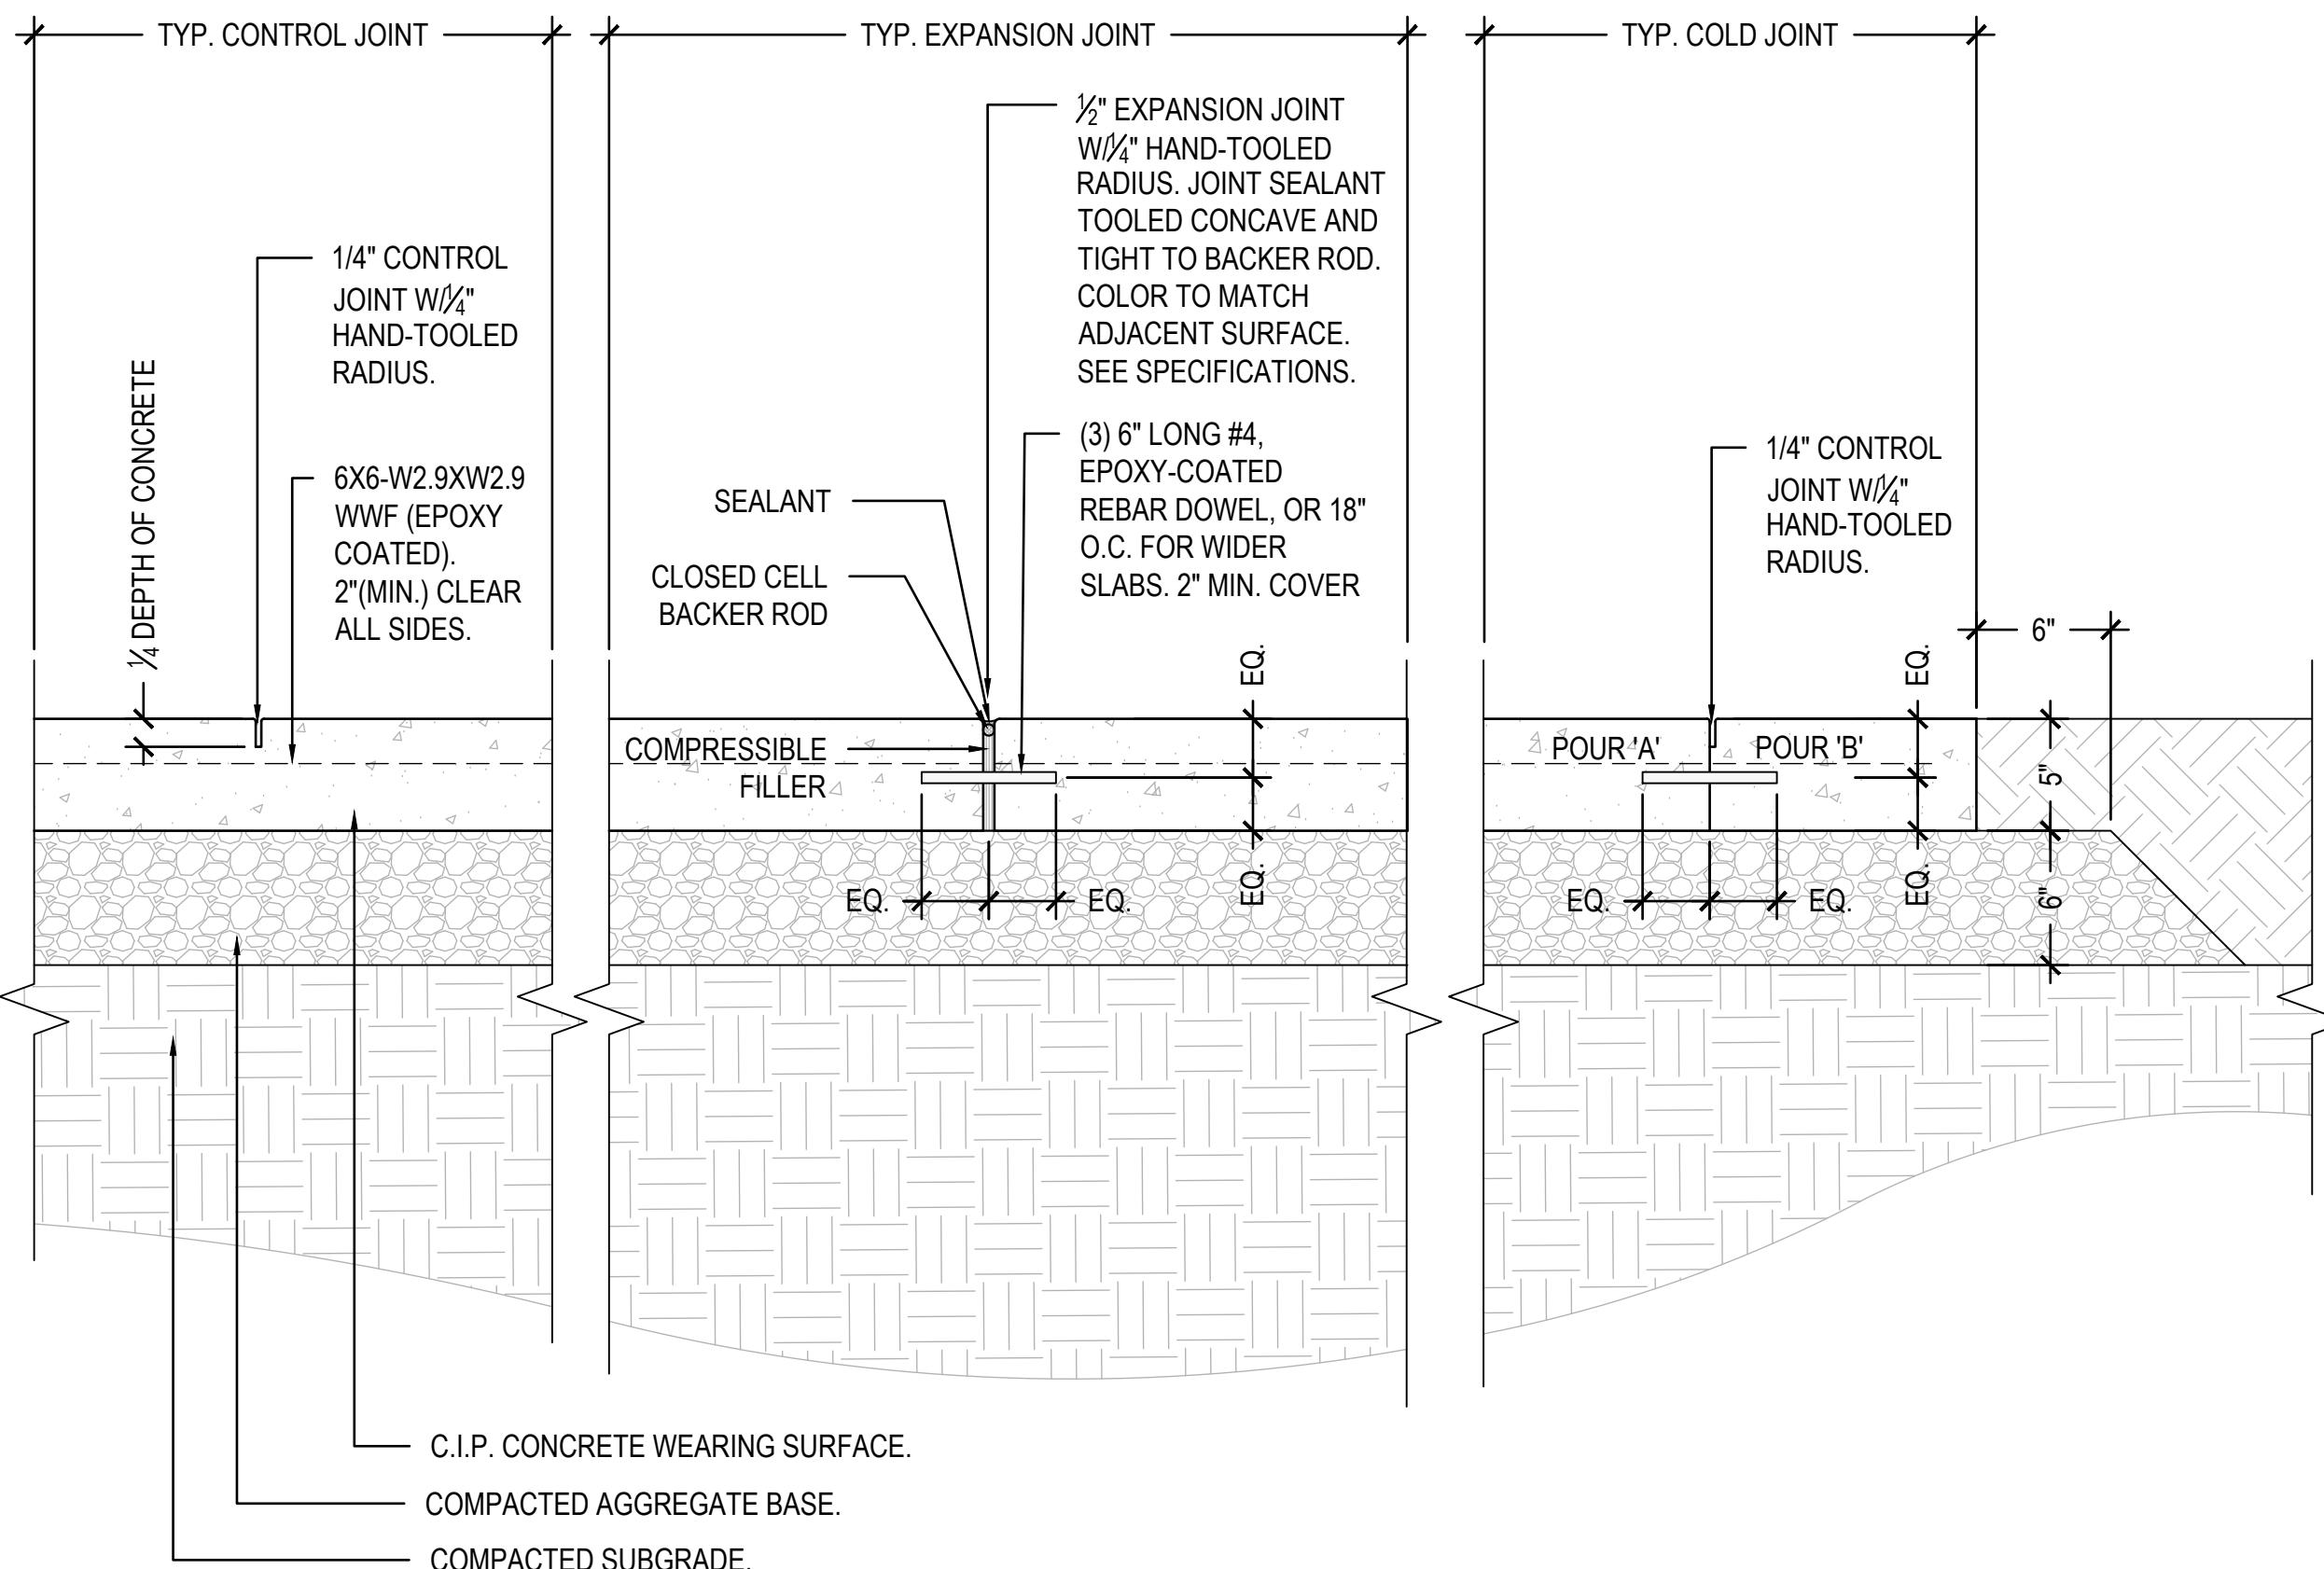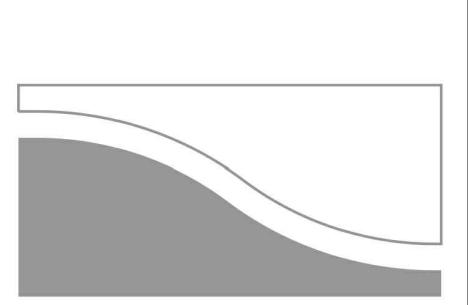

NOTES:
 1. ALL C.I.P. CONCRETE WALKING SURFACES WITHIN LIMIT OF WORK FOR THIS PROJECT SHALL HAVE AN EXPOSED AGGREGATE FINISH. ALL C.I.P. CONCRETE PADS FOR LP TANK, AC UNIT AND KING GAMBRINUS STATUE SHALL HAVE A LIGHT BROOM FINISH. SEE SPECIFICATION SECTIONS 03 30 00 AND 03 08 00.
 2. ALL EXPOSED CORNERS OF C.I.P. CONCRETE SHALL RECEIVE $\frac{1}{4}$ " HAND-TROWELED RADIUS.
 3. CONTROL JOINTS SHALL BE SPACED AS SHOWN ON PLANS.
 4. EXPANSION JOINTS SHALL BE PLACED WHERE CONCRETE WEARING SURFACE ABUTS VERTICAL OBJECTS: I.E. WALLS, FOOTINGS, STAIRS, ETC., WHERE NEW CONCRETE INTERFACES OLD CONCRETE AND WHERE SHOWN ON DRAWINGS.
 5. COLD JOINTS SHALL BE PLACED BETWEEN SEPARATE POURS OF THE SAME WEARING SURFACE.
 6. ALL JOINTS AND EXPOSED EDGES OF CONCRETE SHALL BE HAND-TROWELED W/ $\frac{1}{4}$ " RADIUS.
 7. VERTICAL TRANSITIONS BETWEEN BUILDING THRESHOLDS AND EXTERIOR WALKING SURFACES SHALL NOT EXCEED $\frac{1}{2}$ ".

1 C.I.P. CONCRETE SIDEWALK AND JOINTING - SECTION
SCALE: 1-1/2"=1'-0"

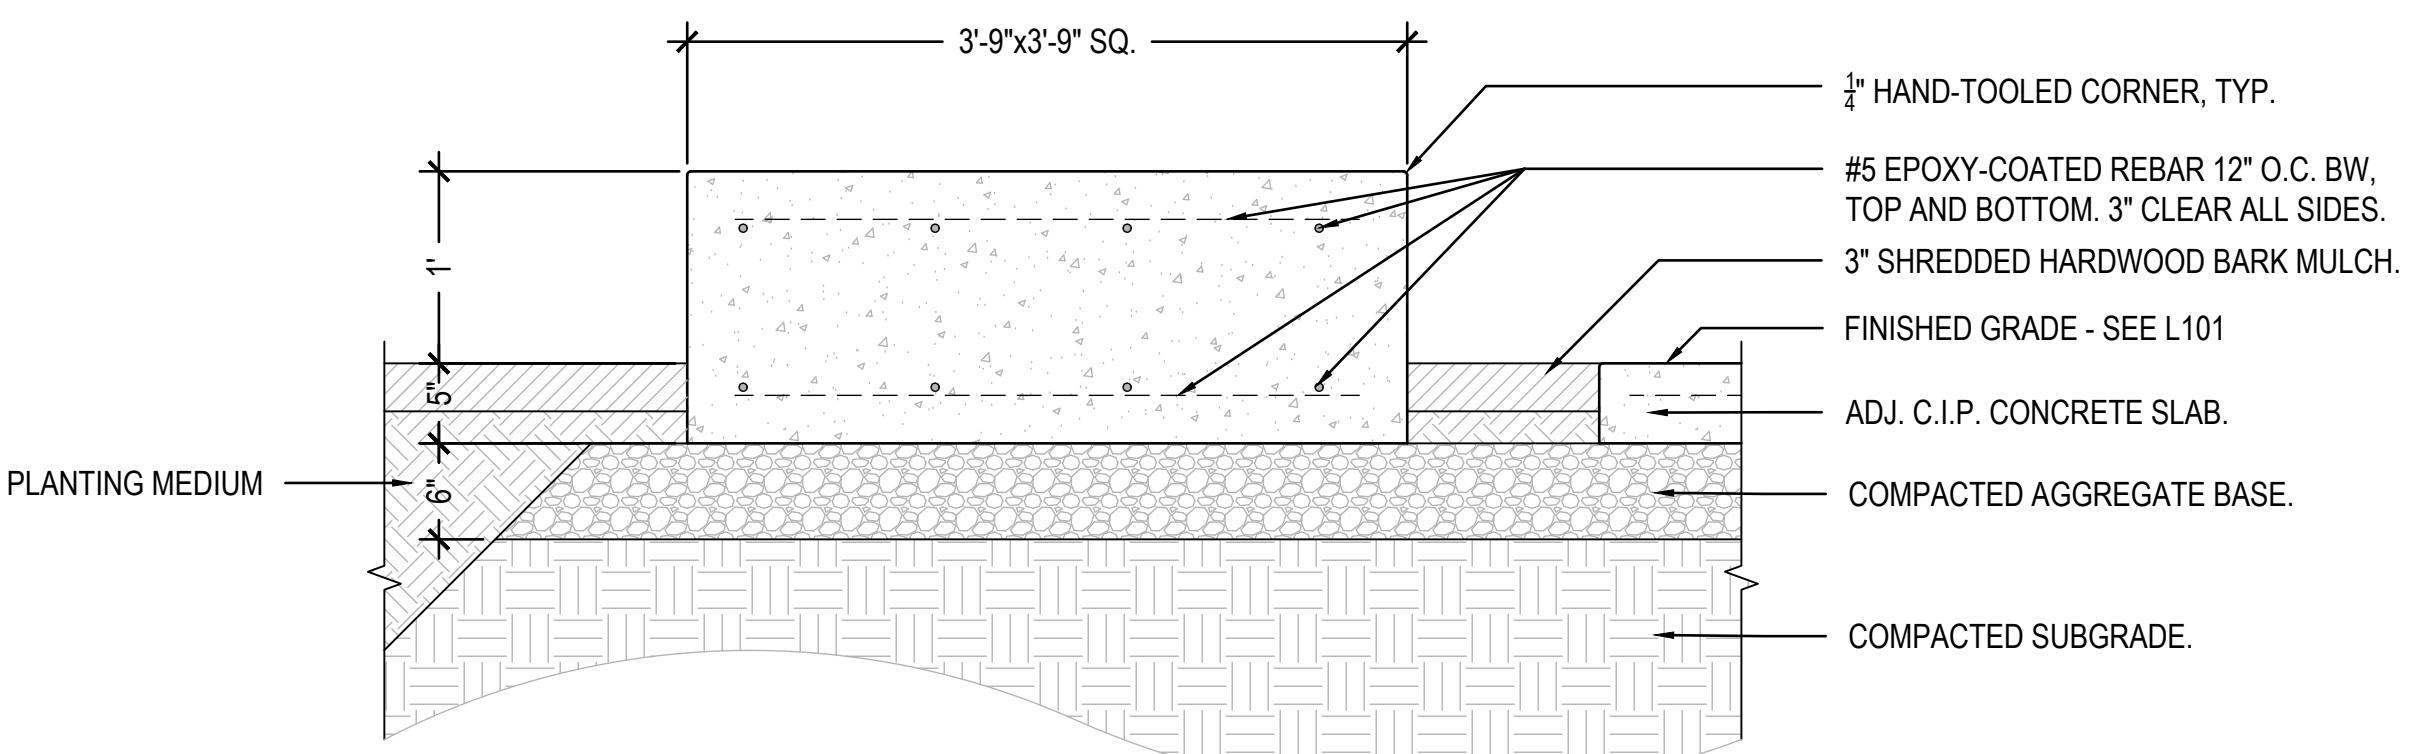

NOTES:
 1. C.I.P. CONCRETE BASE SHALL HAVE SMOOTH HAND-RUBBED FINISH ON EXPOSED VERTICAL FACES.
 2. ALL EXPOSED CORNERS OF C.I.P. CONCRETE SHALL RECEIVE $\frac{1}{4}$ " HAND-TROWELED RADIUS.
 3. INSTALLATION OF STATUE SHALL BE BY OWNER.


2 C.I.P. CONCRETE BASE FOR KING GAMBRINUS STATUE - SECTION
SCALE: 1-1/2"=1'-0"

Tavern Renovations Old World Wisconsin Ethnic Outdoor Museum Wisconsin Historical Society Town of Eagle, Wisconsin	State of Wisconsin Department of Administration Division of Facilities Development
Sheet Title: TAVERN SITE AND PLANTING DETAILS	

Revisions:
No. Date: Description:

Graphic Scale	SEE DETAILS
DFD Number	1711K-04
Set Type	BD
Date Issued	9/8/2023
Sheet Number	L500


DOOR AND HARDWARE SCHEDULE1														
DOOR NUMBER	DOOR				FRAME				MISCELLANEOUS			REMARKS		
	QTY.	LEAF SIZE	WIDTH	HEIGHT	TYPE	MATL	GLAZING TYPE	FINISH	TYPE	MATL	HEAD JAMB	OTHER	DETAILS	
100	(1)	8' - 6"	9'-10 1/2"	P5	WD-2	-	CLR	-	-	3/A001	-	-	-	ETR
101	(1)	8' - 6"	9'-10 1/2"	P4	WD-2	-	CLR	-	-	3/A001	-	-	-	ETR
103	(1)	3'-0"	8'-0"	P1	WD-2	-	CLR	ETR WD	ETR WD	--	-	-	-	ETR

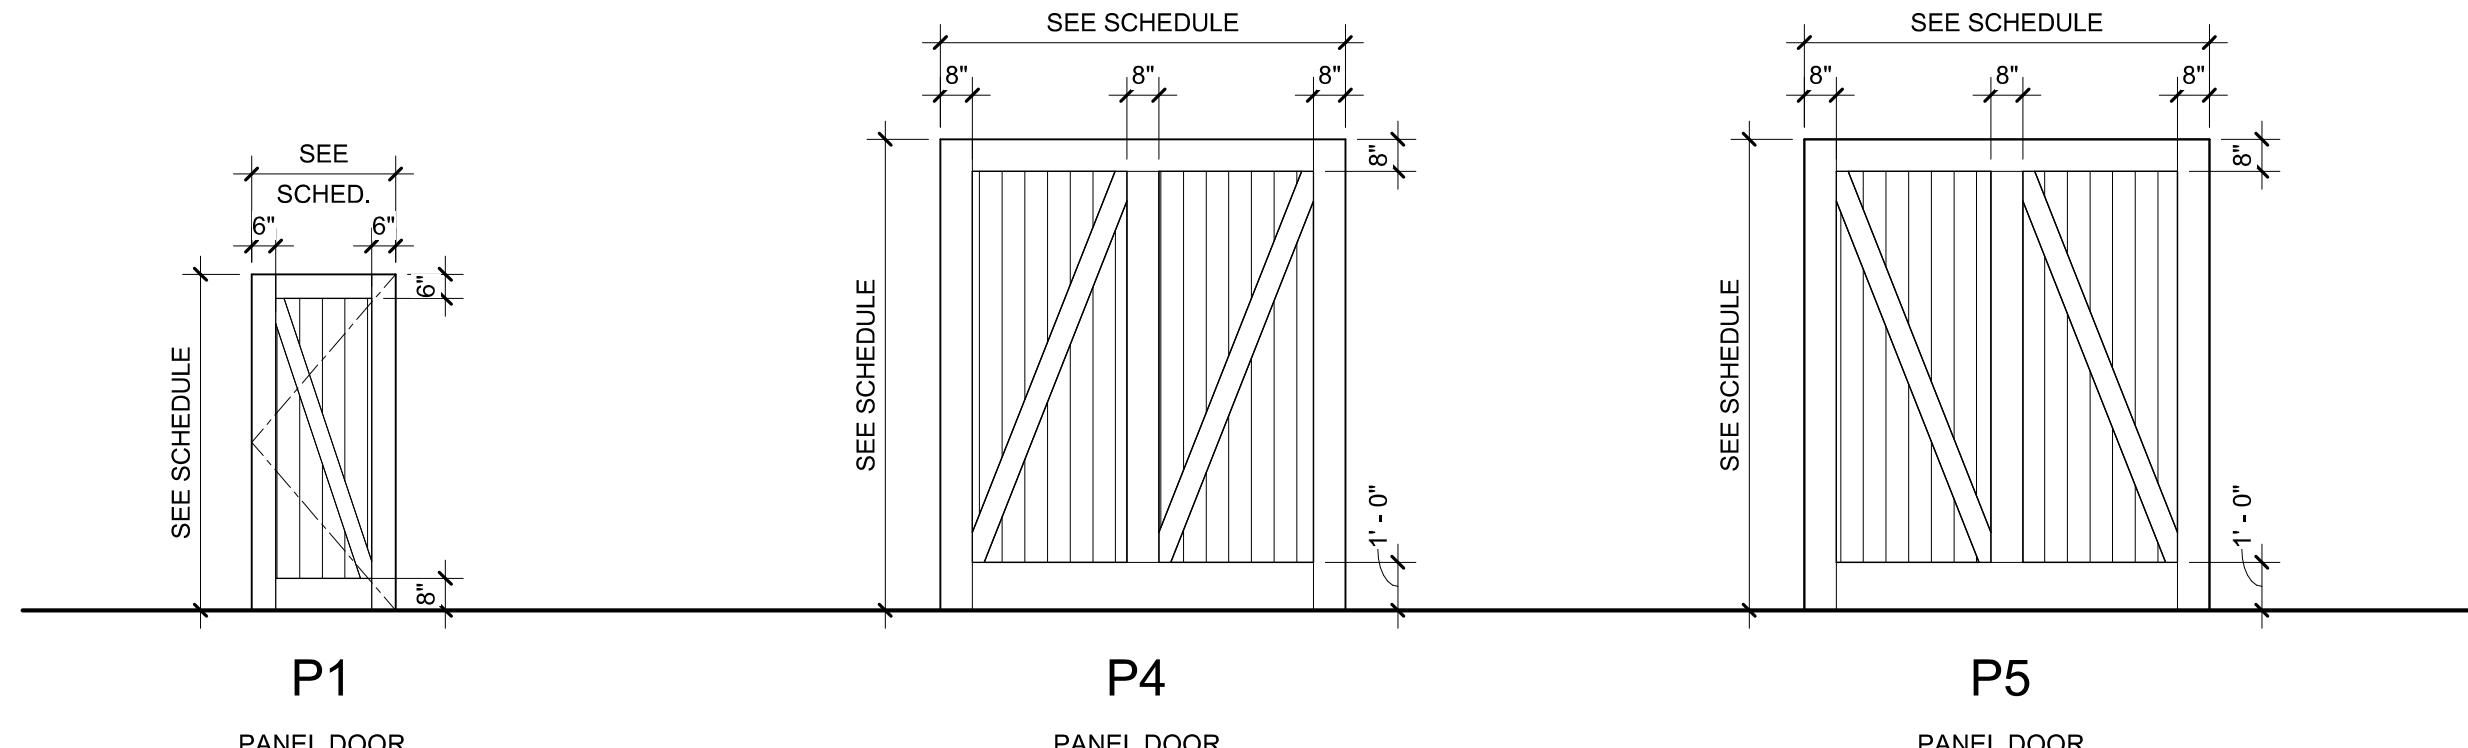

2 DOOR TYPES

1/4" = 1'-0"

0 2 4 8

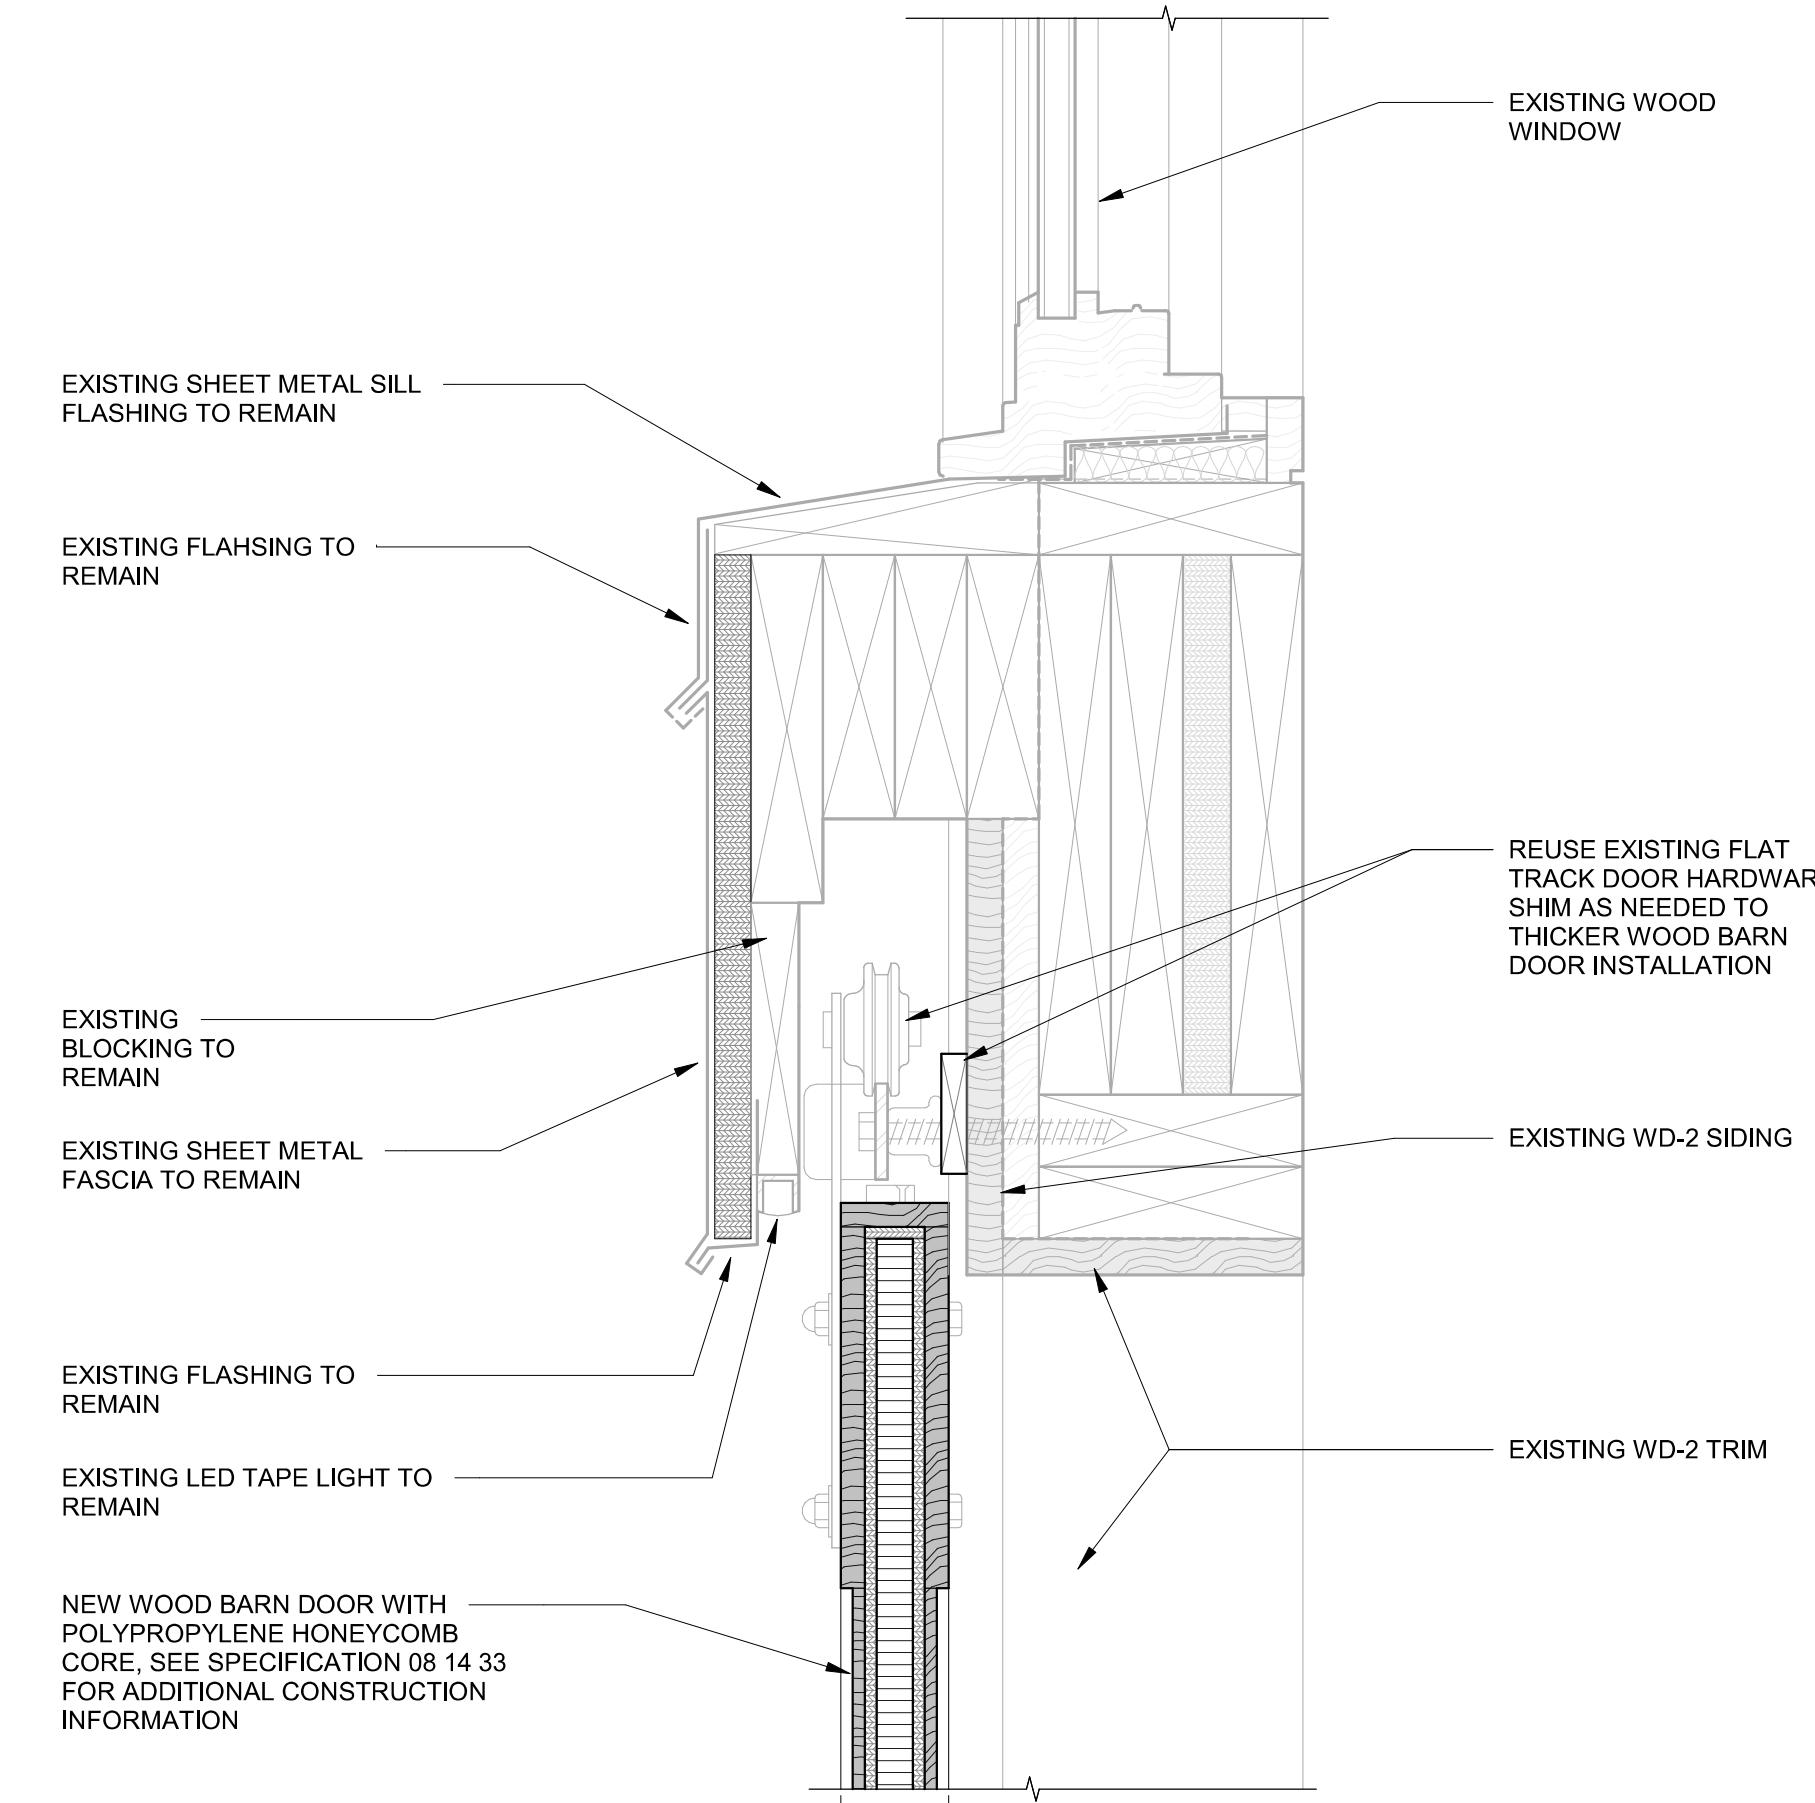

3 BARN DOOR HEAD DETAIL

3" = 1'-0"

0 0.25 0.5 0.75

HAZARDOUS MATERIALS:

ASBESTOS:
EXISTING ROOF SHINGLES, ROOF FELT AND MASTIC ALONG WITH WINDOW GLAZING COMPOUND AND ALL CAULKING, SEALANTS AND MISCELLANEOUS MASTICS/ADHESIVES ARE ASSUMED TO CONTAIN ASBESTOS. CONTRACTOR DISTURBING THESE MATERIALS SHALL COMPLY WITH WISCONSIN ADMINISTRATIVE CODE 159-CERTIFICATION AND TRAINING REQUIREMENTS FOR ASBESTOS ACTIVITIES. SEE SPECIFICATION, GENERAL REQUIREMENTS, #5. HAZARDOUS SUBSTANCES FOR ADDITIONAL INFORMATION.

LEAD BASED PAINT:
EXISTING PAINT IS ASSUMED TO CONTAIN LEAD.

UNLESS REMOVAL OF THE PAINT FROM THE SUBSTRATE IS SPECIFICALLY CALLED OUT, DISTURBANCE OF LEAD-BASED PAINT IS A CONTRACTOR'S SHA REQUIREMENT.

IF REMOVAL OF THE EXISTING PAINT FROM A SUBSTRATE IS REQUIRED, THE DISPOSAL OF THE LEAD-BASED PAINT REMOVED WILL BE BY THE STATE UNDER SEPARATE CONTRACT. CONTRACTOR IS RESPONSIBLE FOR COLLECTION OF THE LEAD-BASED PAINT CHIPS, BLAST MEDIA, REMOVAL AGENTS OR LEAD BASED PAINT DUSTS REMOVED FROM ITS SUBSTRATE. THE STATE WILL PAY DIRECTLY TO THE PROVIDER FOR THE REMOVAL OF THE LEAD-BASED PAINT. THE PROVIDER, ONLY LEAD BASED PAINT CHIPS AND/OR DEBRIS IS TO BE DEPOSITED INTO THE DISPOSAL CONTAINERS PROVIDED. CHARGES FOR THE CONTAINERS, TRANSPORT AND DISPOSAL OF THE LEAD BASED PAINT WASTE WILL BE PAID DIRECTLY BY THE STATE.

BUILDING CODE INFORMATION:

APPLICABLE CODES:
WISCONSIN UNIFORM COMMERCIAL BUILDING CODE
EFFECTIVE MAY 1, 2018 (BASED ON 2015 INTERNATIONAL
BUILDING CODE WITH WISCONSIN AMENDMENTS - SPS 361-366)

2015 INTERNATIONAL EXISTING BUILDING CODE

2015 INTERNATIONAL ENERGY CONSERVATION CODE WITH WISCONSIN AMENDMENTS - SPS 363

2015 INTERNATIONAL MECHANICAL CODE WITH WISCONSIN AMENDMENTS - SPS 364

2015 INTERNATIONAL FUEL GAS CODE WITH WISCONSIN AMENDMENTS - SPS 365

2015 WISCONSIN PLUMBING CODE - SPS 381-387

WISCONSIN STATE ELECTRICAL CODE - SPS 316

BUILDING NAME: TAVERN

CLASS OF CONSTRUCTION:
TYPE SB UNPROTECTED
CLASSIFIED AS A HISTORIC STRUCTURE
BY WISCONSIN HISTORIC SOCIETY

BUILDING LEVEL:
LEVEL 1

OCCUPANCY: BUSINESS (B) OCCUPANCY

LOWER LEVEL = 4 OCCUPANTS

FIRST FLOOR = 32 OCCUPANTS

SECOND FLOOR = 6 OCCUPANTS

ALTERATION LEVEL:
LEVEL 1


PROJECT WORK AREA:

LOWER LEVEL = 907 SF


FIRST FLOOR = 632 SF

SECOND FLOOR = 569 SF

LEGEND - PLAN SYMBOLS

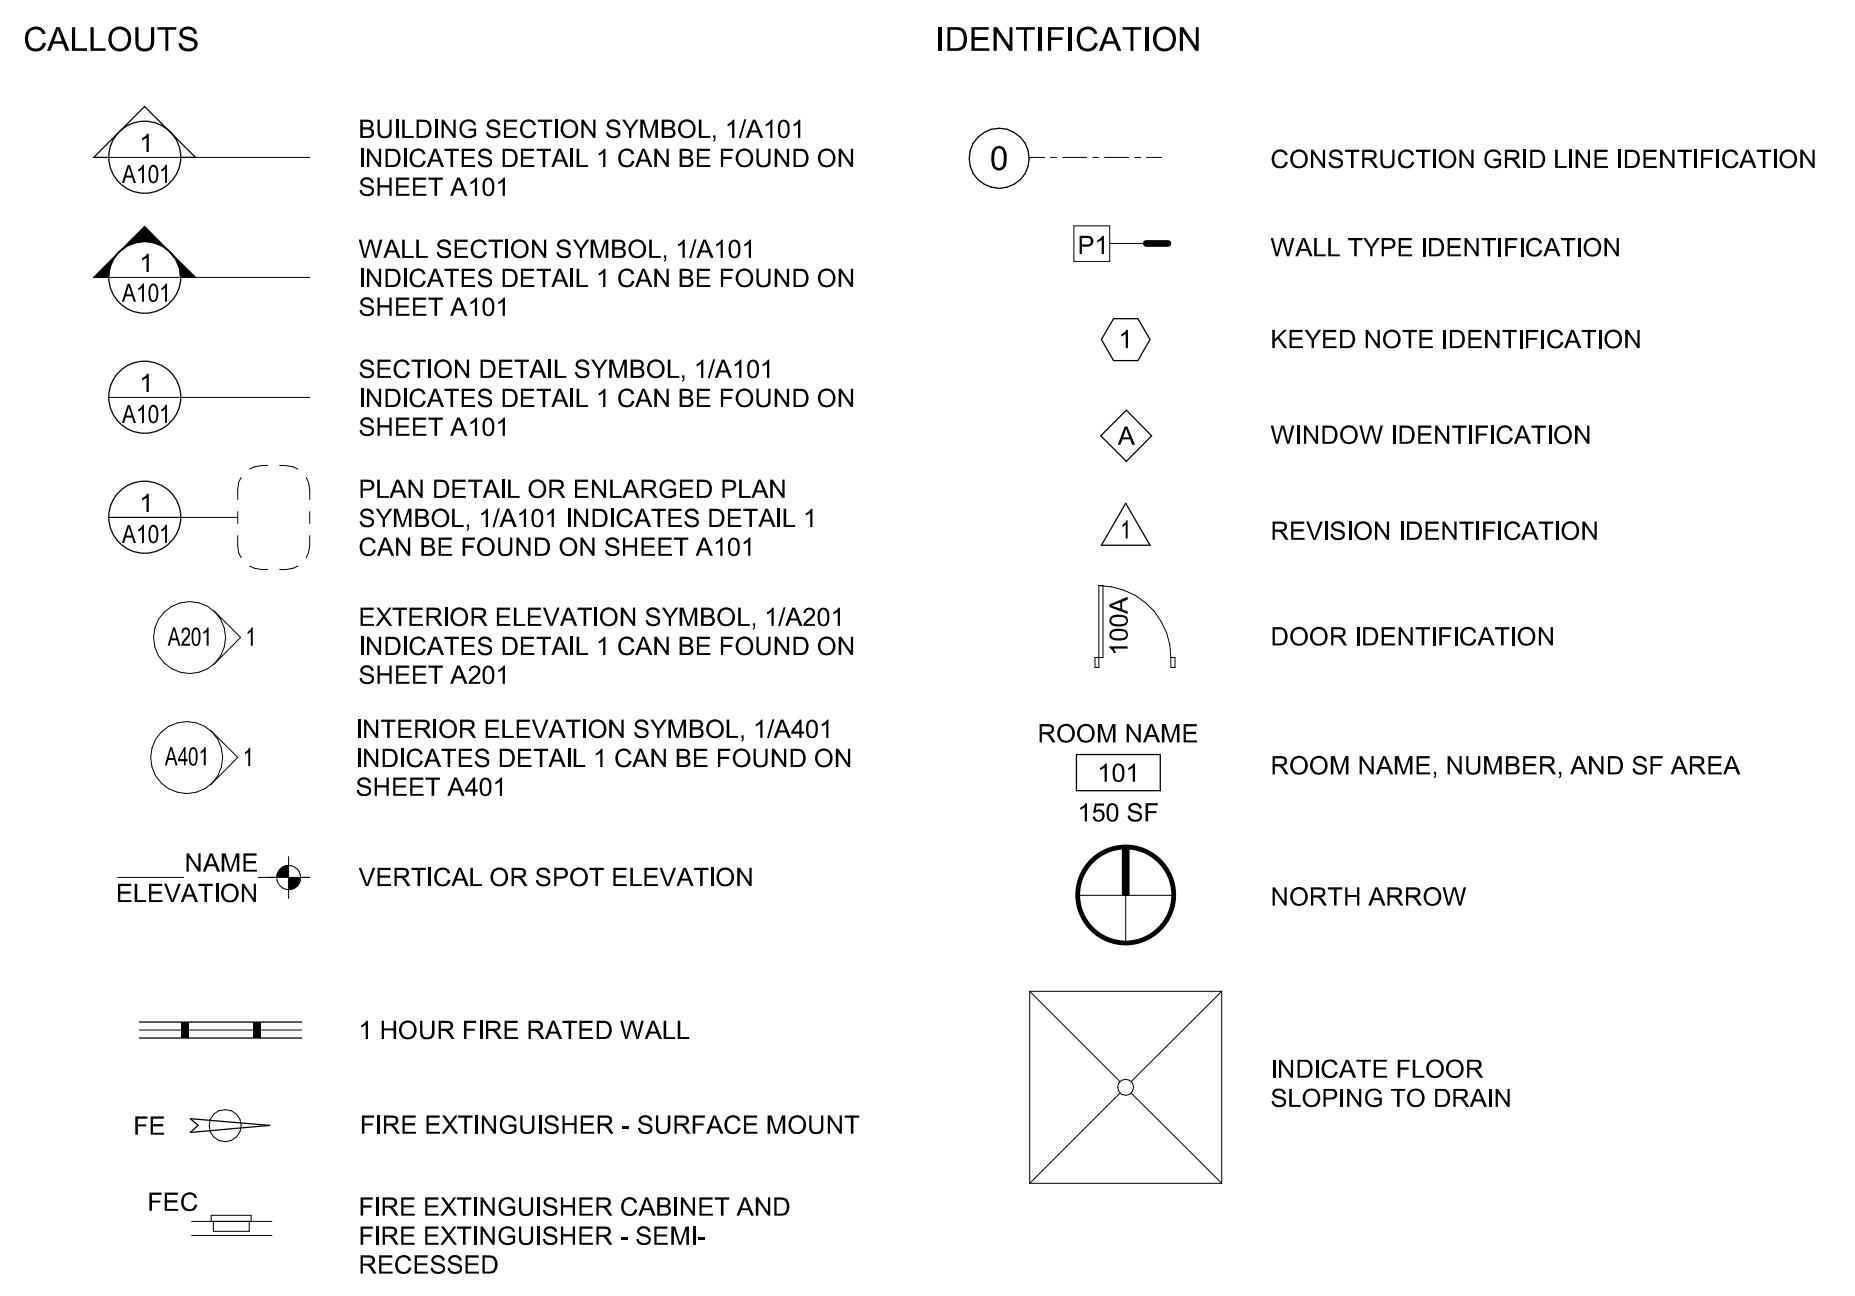


HATCH SYMBOLS

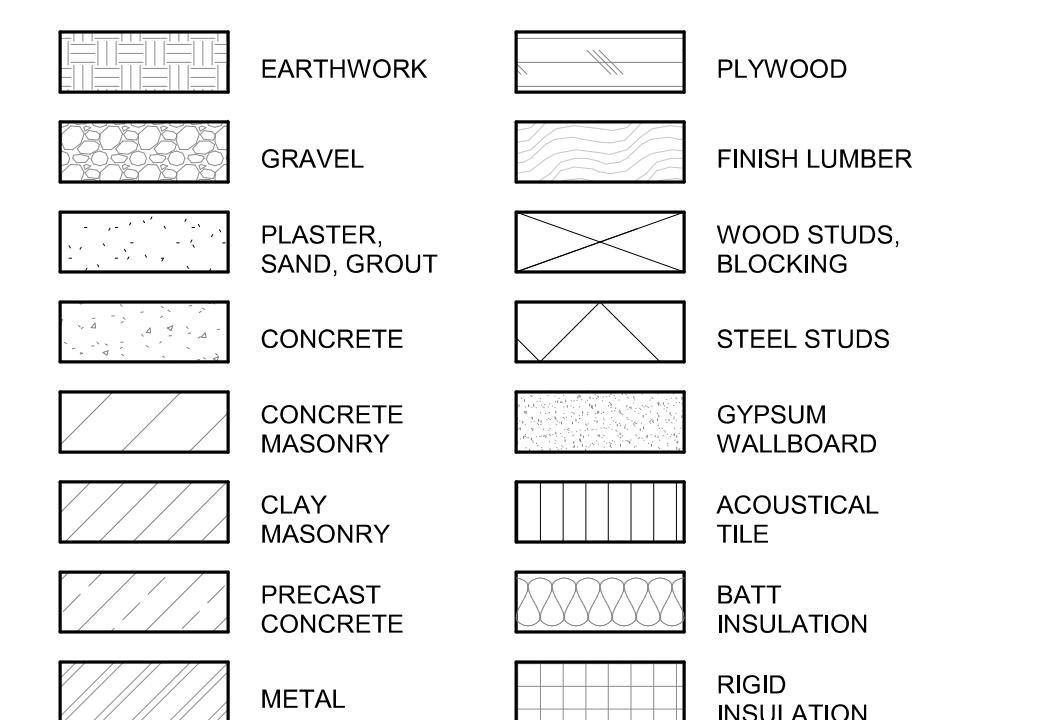


ABBREVIATIONS:

ADA - AMERICAN WITH DISABILITIES ACT
AF - ABOVE FLOOR
AV - AUTO VISUAL
CFGI - CONTRACTOR FURNISHED CONTRACTOR INSTALLED
CL - CENTERLINE
CNC - CAVING
CLR - CLEAR
DIM - DIMENSION
DN - DOWN
EAC - EC
EC - ELECTRICAL CONTRACTOR
ESEW - EMERGENCY SAFETY SHOWER/EYEWASH
ETR - EXISTING TO REMAIN
EUD - ELEVATED UNTIL
FD - FLOOR DRAIN
FEC - FIRE EXTINGUISHER CABINET
FRT - FIRE RESISTANT TREATED
FSP - FIRE SPRINKLER
GC - GENERAL CONTRACTOR
GWB - GYPSUM WALL BOARD
LFC - LAB FURNISHINGS CONTRACTOR
MAN - MANUFACTURED
MB - MARKERBOARD
MC - MECHANICAL CONTRACTOR
MIN - MINIMUM
MS - MINERAL INSULOUS
MTD - MOUNTED
NIC - NOT IN CONTRACT
NTS - NOT TO SCALE
OFCI - OWNER FURNISHED CONTRACTOR INSTALLED
OPF - OWNER FURNISHED OWNER INSTALLED
OPP - OPPOSITE
PC - PLUMBING CONTRACTOR
SM - STONE
SS - STAINLESS STEEL
STD - STANDARD
THK - THICK
TYP - TYPICAL
UNO - UNLESS OTHERWISE NOTED
UNO - UNLESS NOTED OTHERWISE
W/ - WITH

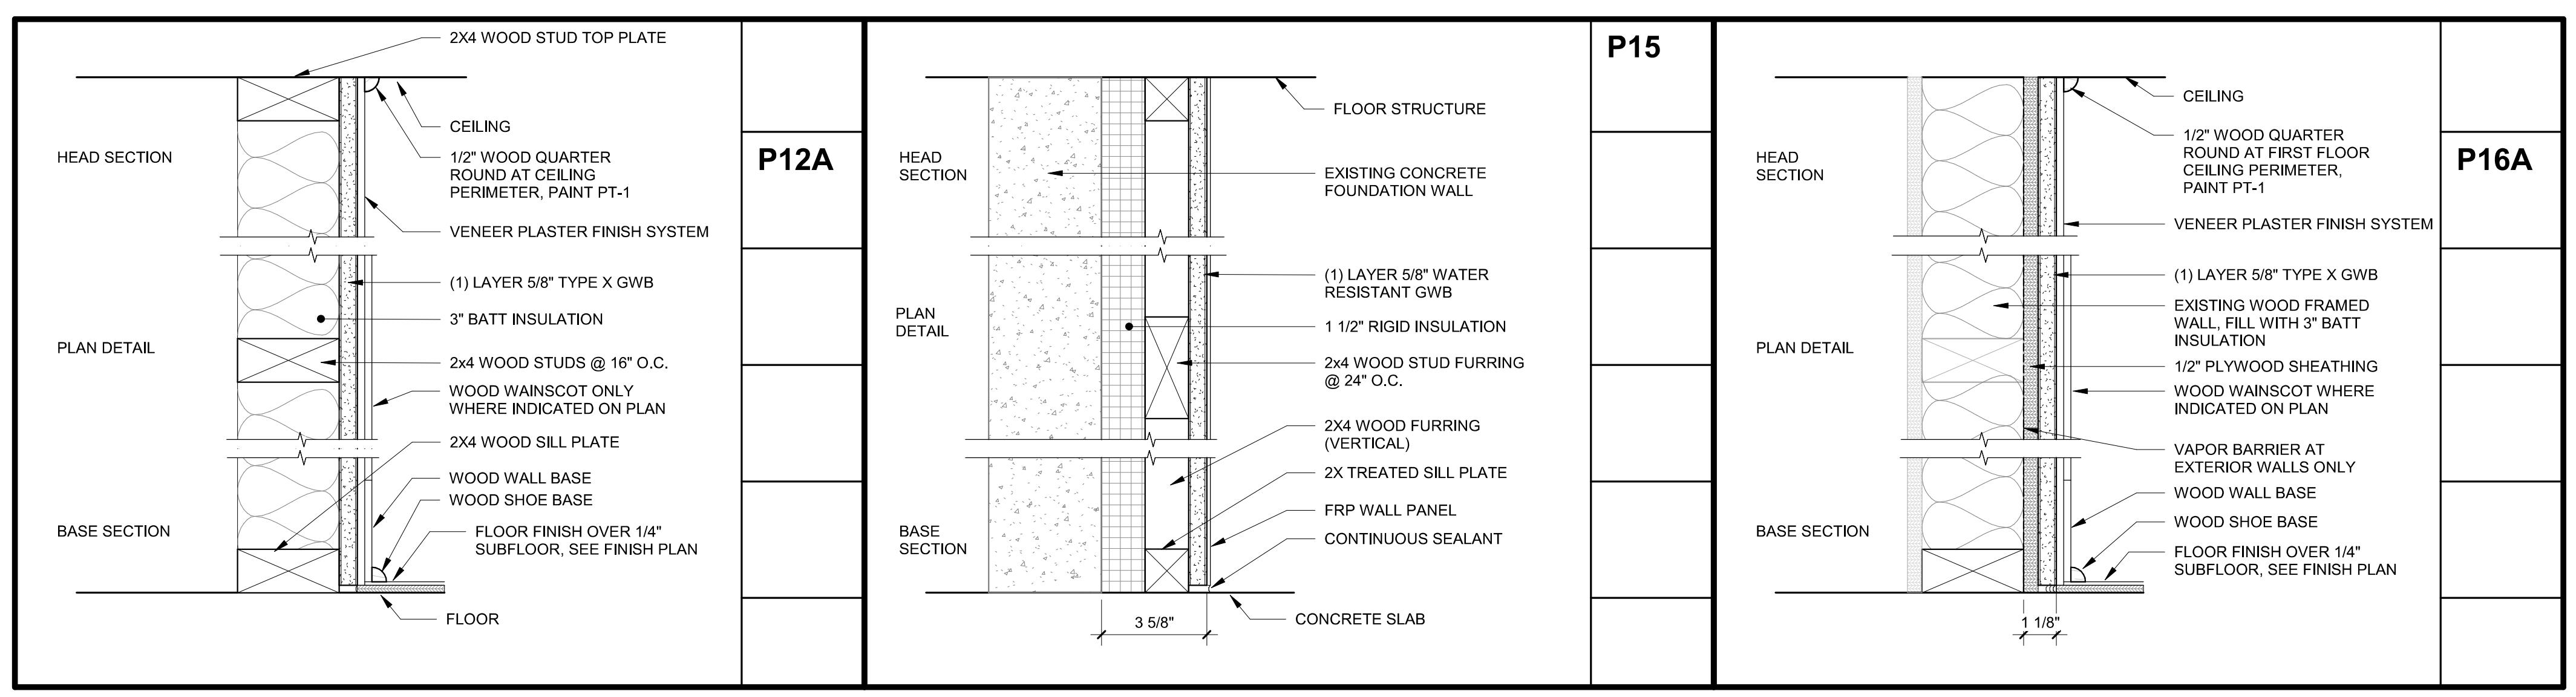

1 PARTITION TYPES

3" = 1'-0"

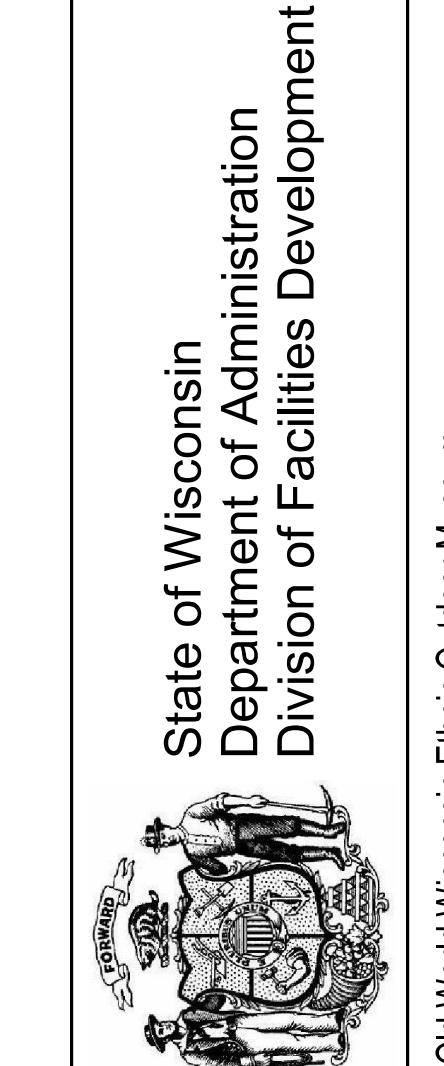

Town of Eagle, Wisconsin

Tavern Renovations
Old World Wisconsin Ethnic Outdoor Museum
Wisconsin Historical Society
Town of Eagle, Wisconsin
Sheet Title:
NOTES, SYMBOLS, ABBREVIATIONS AND PARTITION TYPES

Revisions:

No. Date: Description:

Graphic Scale	See Details
DFD Number	171K-04
Set Type	BD
Date Issued	9/8/2023
Sheet Number	A001

DEMOLITION PLAN GENERAL NOTES:


1. ALL EXISTING WALLS TO REMAIN ARE SHOWN SHADED.
2. TEMPORARY LIGHTING IS THE RESPONSIBILITY OF THE ELECTRICAL CONTRACTOR FOR THE DURATION OF THE PROJECT.
3. COORDINATE WITH SPECIFICATION SECTION 01 74 19 FOR CONSTRUCTION WASTE MANAGEMENT AND PROJECT RECYCLING REQUIREMENTS.
4. SEE SHEET ED110 FOR ADDITIONAL ELECTRICAL DEMOLITION ITEMS.

DEMOLITION PLAN SYMBOL LEGEND

- — — TEMPORARY DUST PARTITION
- — — EXISTING PARTITION TO REMAIN
- · · · · EXISTING PARTITION TO BE REMOVED
- · · · · EXISTING DOOR TO REMAIN
- · · · · EXISTING DOOR TO BE REMOVED
- — — EXISTING ITEM TO REMAIN
- — — EXISTING ITEM TO BE REMOVED
- ① KEYED NOTE IDENTIFICATION

KEYED NOTES #

- | | |
|----|---|
| 1 | DEMO EXISTING WOOD PANELED WALLS ENTIRELY |
| 2 | REMOVE EXISTING WOOD WINDOW OR DOOR TRIM AND STORE TO ALLOW FOR PLASTER REMOVAL. TRACK PIECES THAT ARE REMOVED SO THEY CAN BE REINSTALLED IN THE SAME LOCATIONS |
| 3 | REMOVE REMAINING EXISTING WOOD WALL BASE, AND STORE TO ALLOW FOR PLASTER REMOVAL. TRACK PIECES THAT ARE REMOVED SO THEY CAN BE REINSTALLED IN THE SAME LOCATIONS |
| 4 | REMOVE EXISTING PLASTER AND ALL WOOD LATH, LEAVE EXTERIOR/INTERIOR WOOD WALL FRAMING, AND ALL WOOD BLOCKING FOR WAINGSCOTING INSTALLATION |
| 5 | REMOVE EXTERIOR DOORS AND STRIP WHITE PAINT ON THE INTERIOR FACE. PREP FOR STAIN FINISH. REMOVE EXISTING HARDWARE NEEDED TO COMPLETE WORK. REINSTALL DOOR AFTER STAINING IS COMPLETE. |
| 6 | REMOVE AND STORE EXISTING TOILET PARTITIONS TO ALLOW FOR WALL PLASTER REMOVAL AT EXTERIOR WALL |
| 7 | CONCRETE WALL BASE TO REMAIN |
| 8 | PLASTER TO REMAIN AT INTERIOR TOILET ROOM FIXTURE WALL |
| 9 | DEMO EXISTING GRAB BAR |
| 10 | DEMO PLASTER TO LEVEL OF WOOD SEAT (APPROX 16" AFF). INSTALL BATT INSULATION IN CAVITY FROM ABOVE DOWN TO WALL SPACE BELOW |
| 11 | CUT 24"X24" OPENING IN EXISTING CONCRETE FOUNDATION WALL FOR NEW ALUMINUM LOUVER INSTALLATION. LOCATE OPENING AS SHOWN WITH TOP OF OPENING 18" BELOW TOP OF FOUNDATION WALL |
| 12 | MODIFY FRAMED OPENING TO ACCEPT OFG WOOD DOOR. WOOD DOOR TO BE INSTALLED ON INTERIOR ONLY. DO NOT CUT OPENING THROUGH TO EXTERIOR SHEATHING AND SIDING |
| 13 | DEMO EXISTING SURFACE MOUNTED LIGHTING. SEE ELECTRICAL |
| 14 | REMOVE EXISTING TONGUE AND GROOVE WOOD CEILING AS NEEDED TO INSTALL NEW LIGHTING AS SHOWN ON ELECTRICAL SHEETS |
| 15 | DEMO EXISTING QUARTER ROUND TRIM AT CEILING TO WALL TRANSITION |
| 16 | REMOVE EXISTING PLASTER CEILING AS NEEDED TO INSTALL NEW LIGHTS AND MECHANICAL GRILLS AS SHOWN ON ELECTRICAL AND MECHANICAL SHEETS |

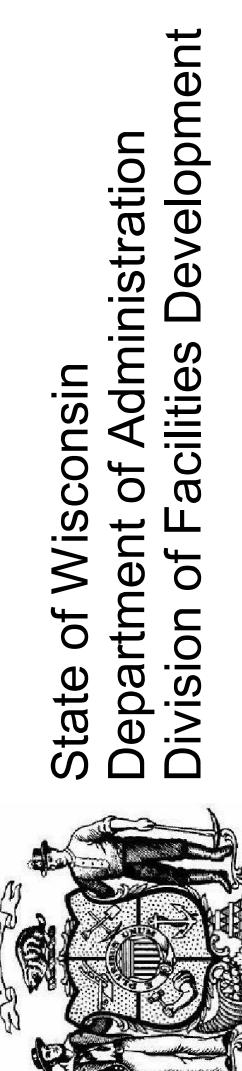


Old World Wisconsin Ethnic Outdoor Museum
Town of Eagle, Wisconsin

State of Wisconsin
Department of Administration
Division of Facilities Development

Old World Wisconsin Ethnic Outdoor Museum
Town of Eagle, Wisconsin


Tavern Renovations
Old World Wisconsin Ethnic Outdoor Museum
Wisconsin Historical Society
Town of Eagle, Wisconsin
Sheet Title:
TAVERN FIRST AND SECOND FLOOR DEMOLITION PLANS

Revisions:
No. Date: Description:

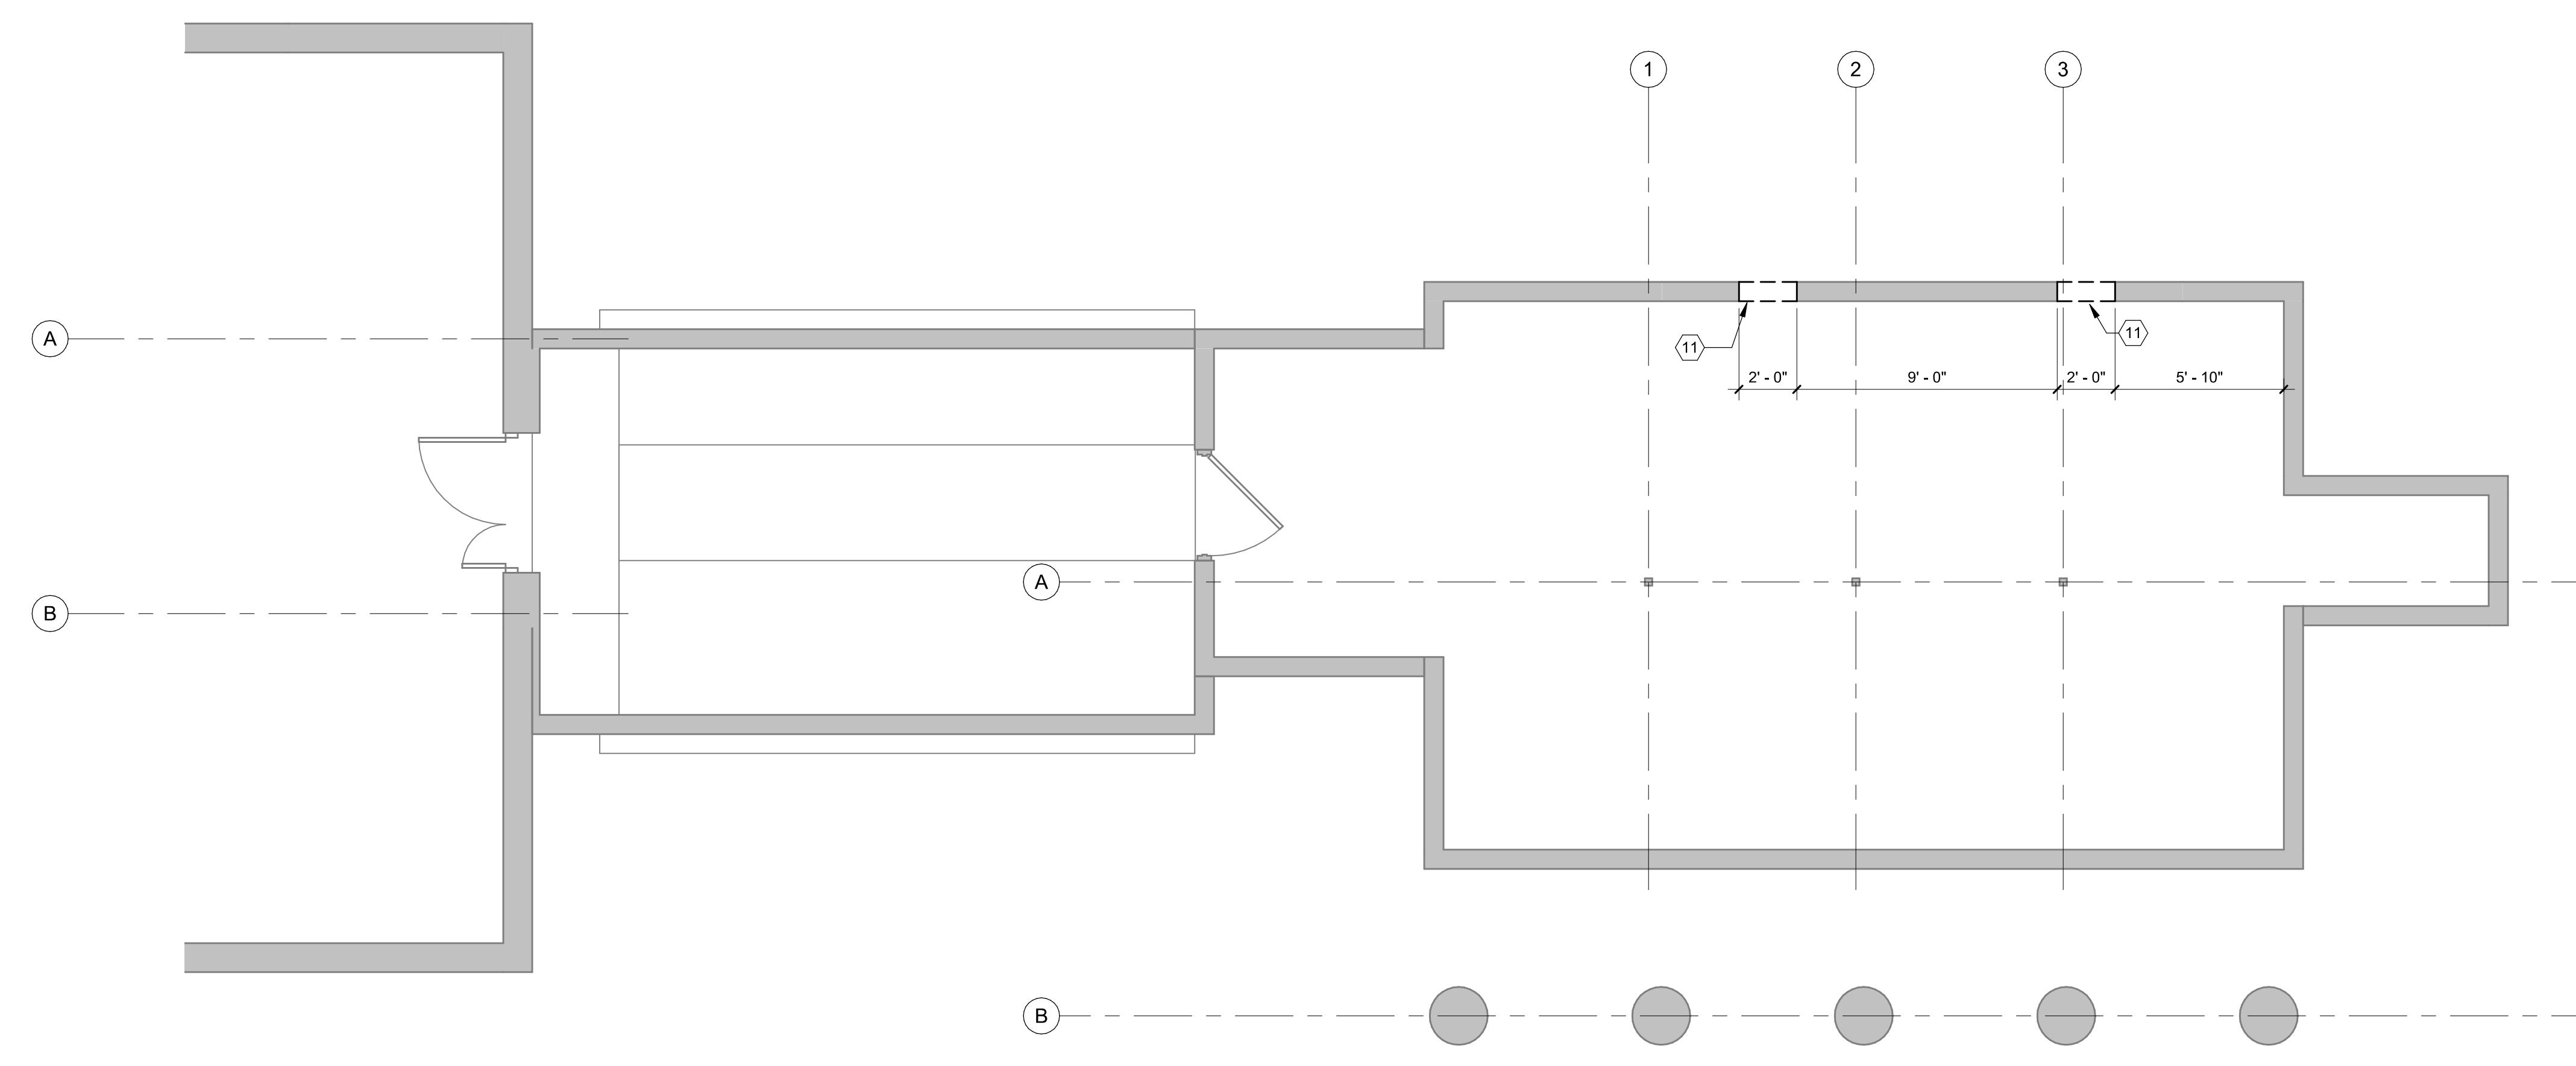


NORTH
1 TAVERN LOWER LEVEL DEMOLITION PLAN

0 2 4 8

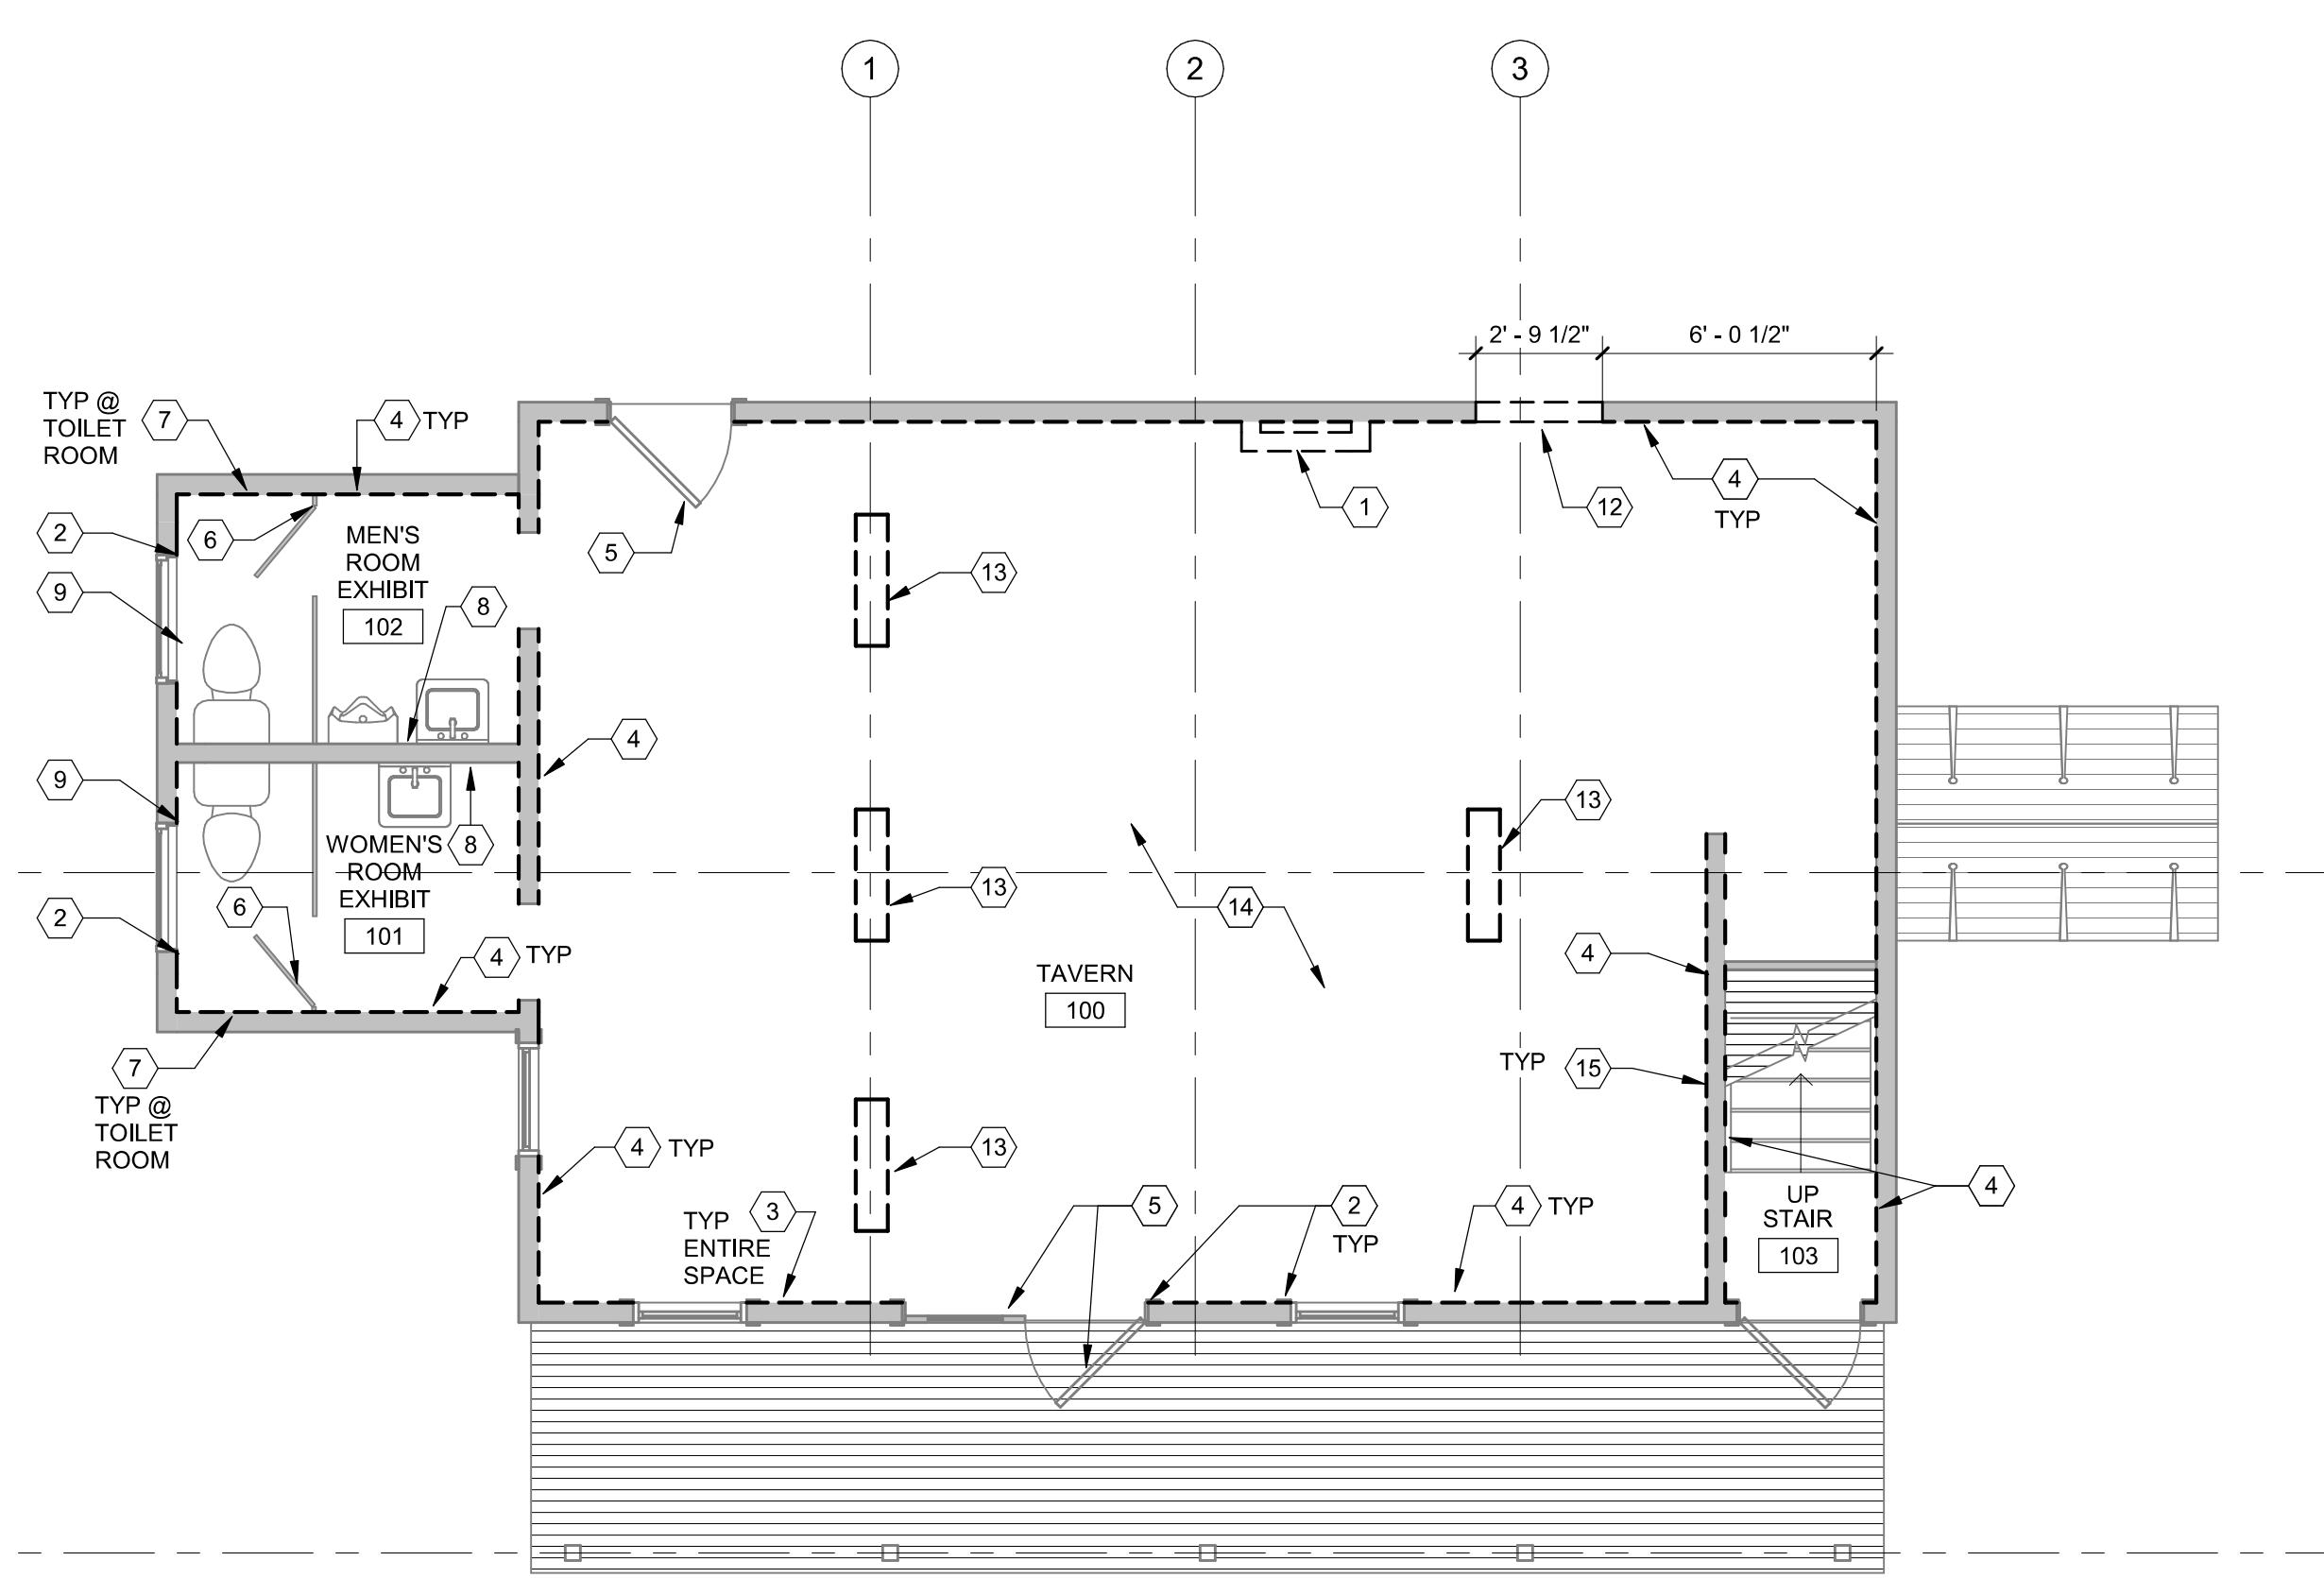

NORTH
2 TAVERN FIRST FLOOR DEMOLITION PLAN

0 2 4 8

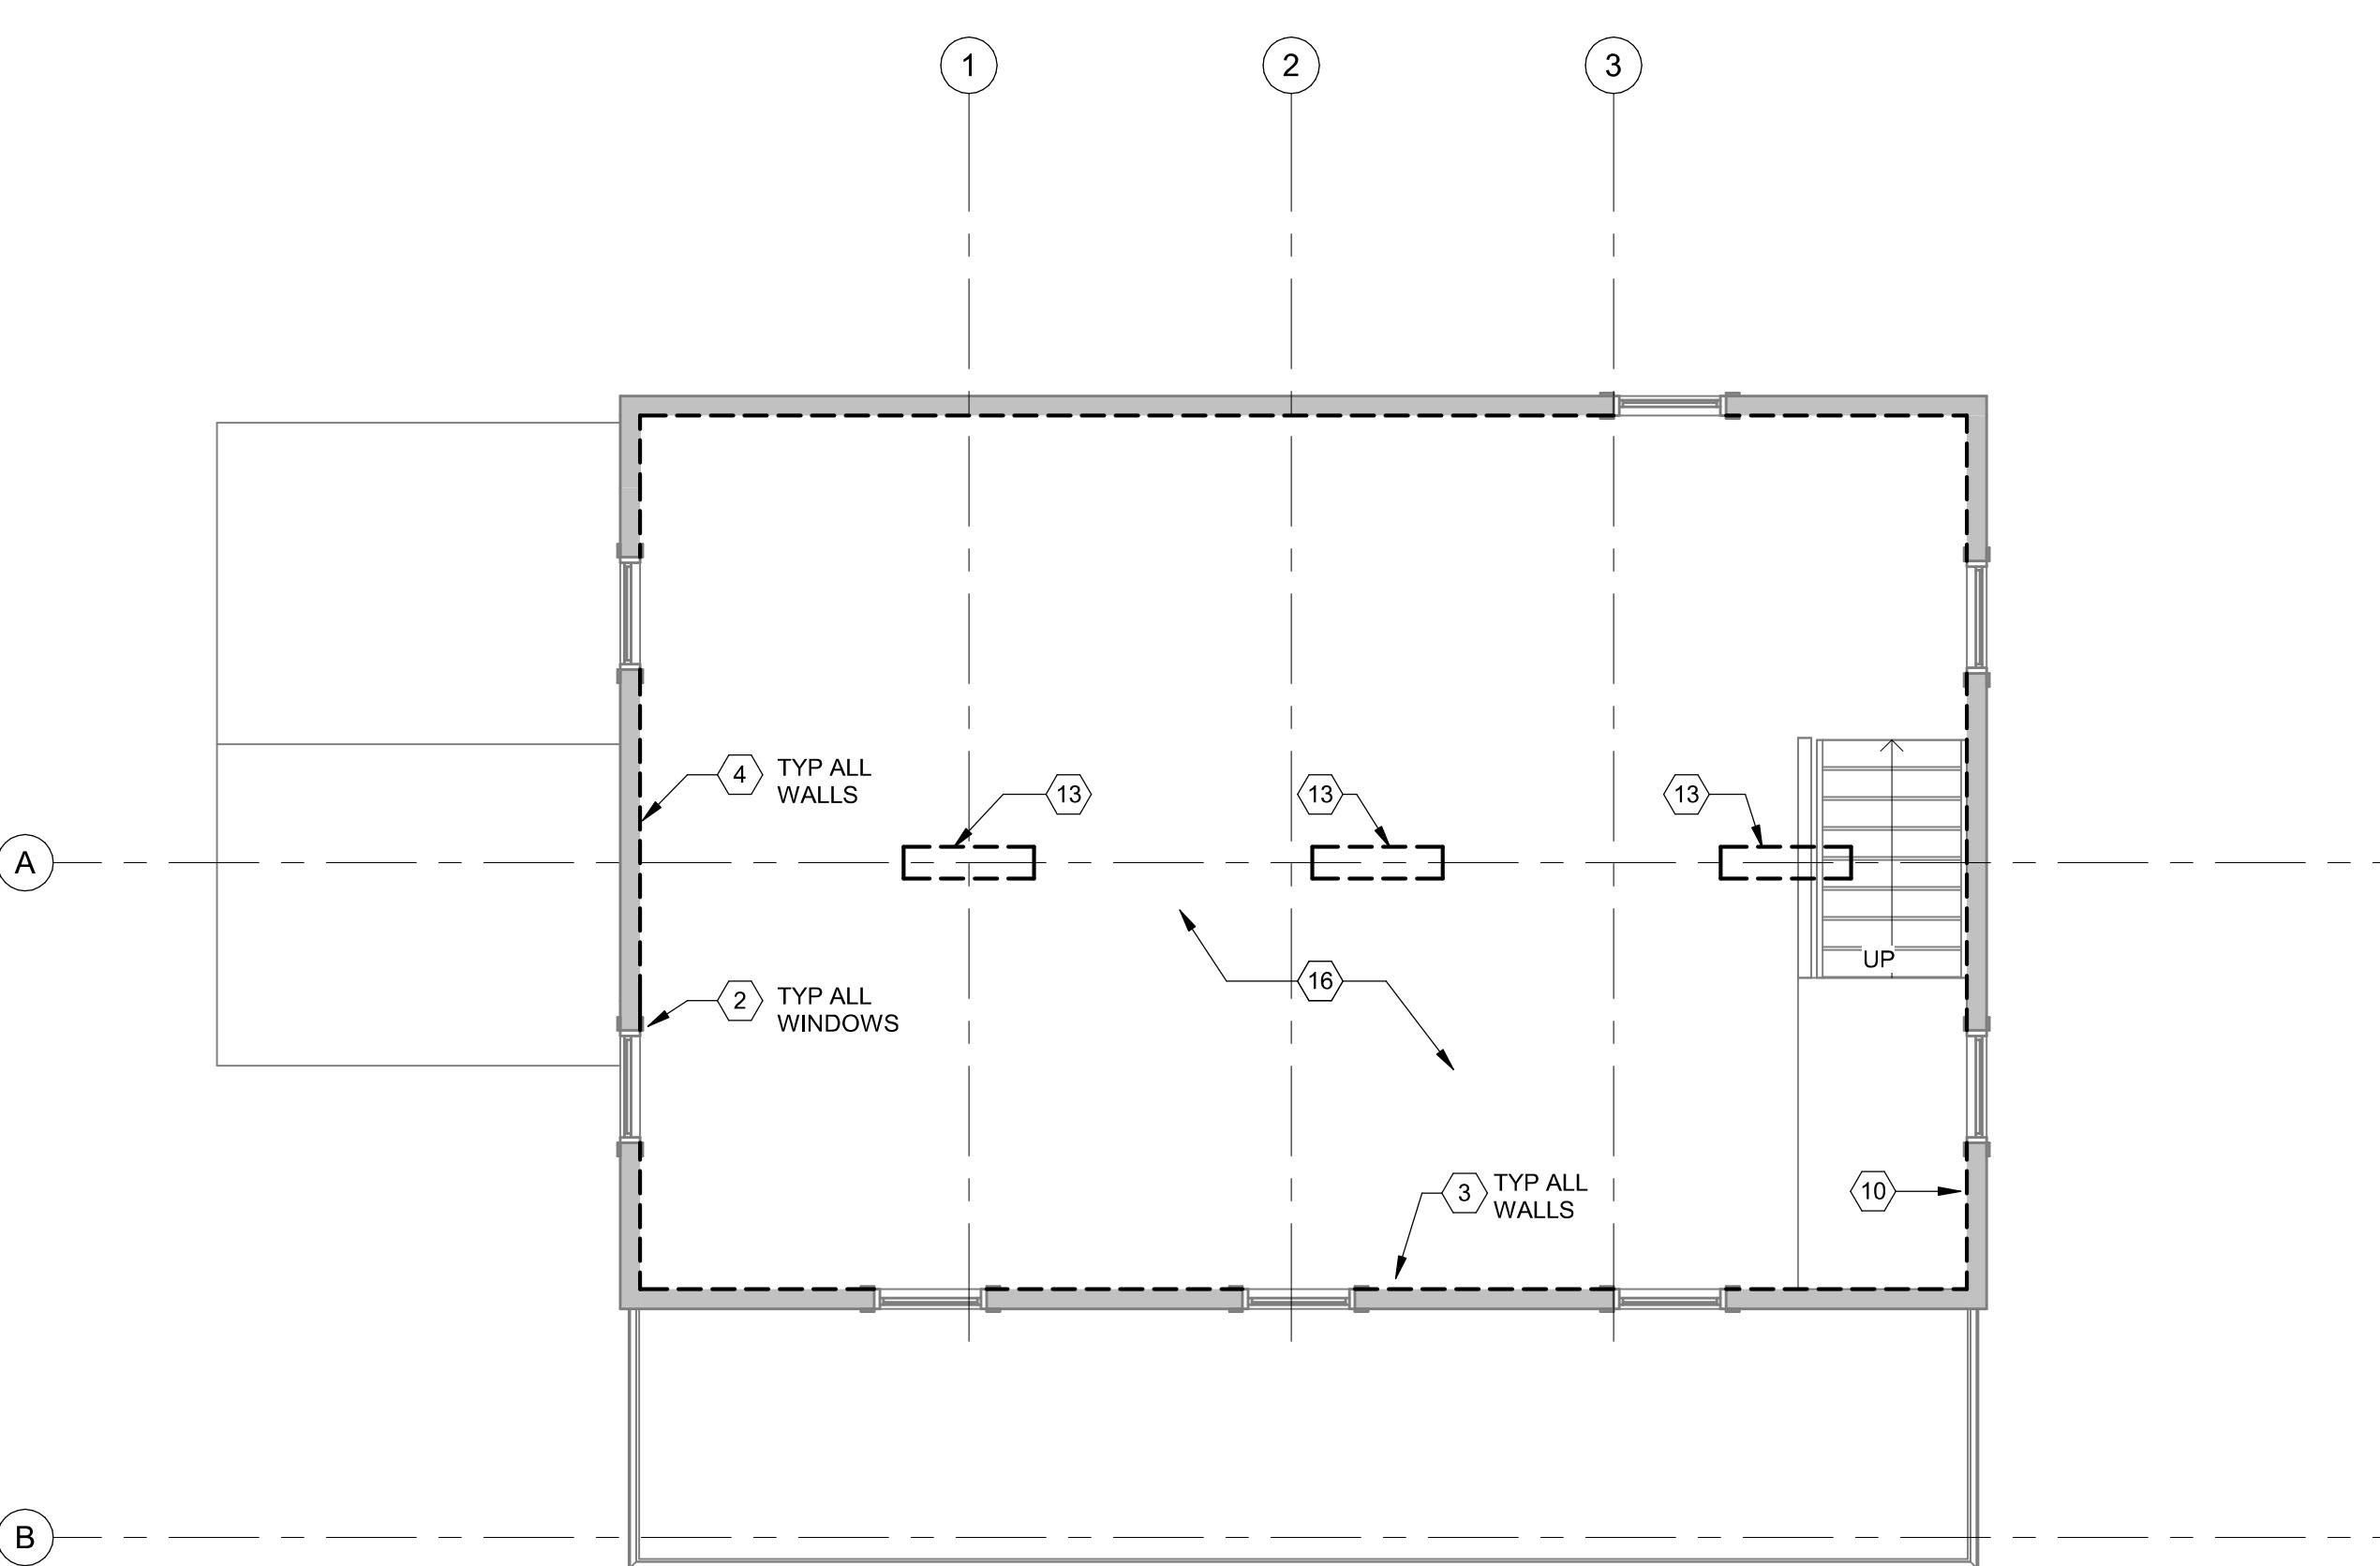

NORTH
3 SECOND FLOOR DEMOLITION PLAN


0 2 4 8

Graphic Scale	See Details
DFD Number	1711K-04
Set Type	BD
Date Issued	9/8/2023
Sheet Number	AD111

Consultant:

CEILING GENERAL NOTES:


- REFER TO A115 FOR FINISH PLANS AND MATERIAL SCHEDULES.
- REFER TO MEP DRAWINGS, SPECIFICATIONS, AND SCHEDULES FOR TYPE AND QUANTITY OF FIXTURES AND EQUIPMENT SHOWN ON THIS PLAN.
- RCP'S INDICATE LAYOUT ONLY. REFER TO ELECTRICAL DRAWINGS FOR ADDITIONAL INFORMATION.
- ALL METAL LINEAR DIFFUSERS AND SHOP PRIMED ACCESS PANELS SHALL BE PAINTED TO MATCH SURROUNDING WALL OR CEILING SURFACE.

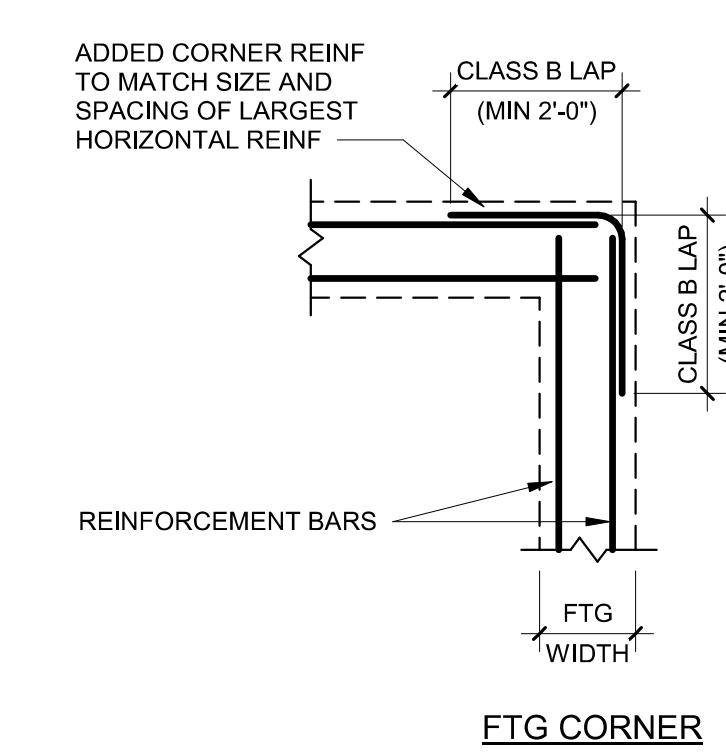


CEILING LEGEND:

	PLASTER CEILING (PAINTED)
	SURFACE MOUNTED LIGHT FIXTURE
	SUPPLY AIR DIFFUSER
	RETURN AIR DIFFUSER / EXHAUST GRILL
	EXHAUST FAN
	RECESSED CAN LIGHT
	INDUSTRIAL FLUORESCENT
	CEILING MOUNTED EXIT LIGHT
	JUNCTION BOX
	SMOKE DETECTOR
	WIRELESS ACCESS POINT
	9'-0" ACP-1 CEILING HEIGHT / MATERIAL

3 TYPICAL FOOTING CORNER REINFORCEMENT

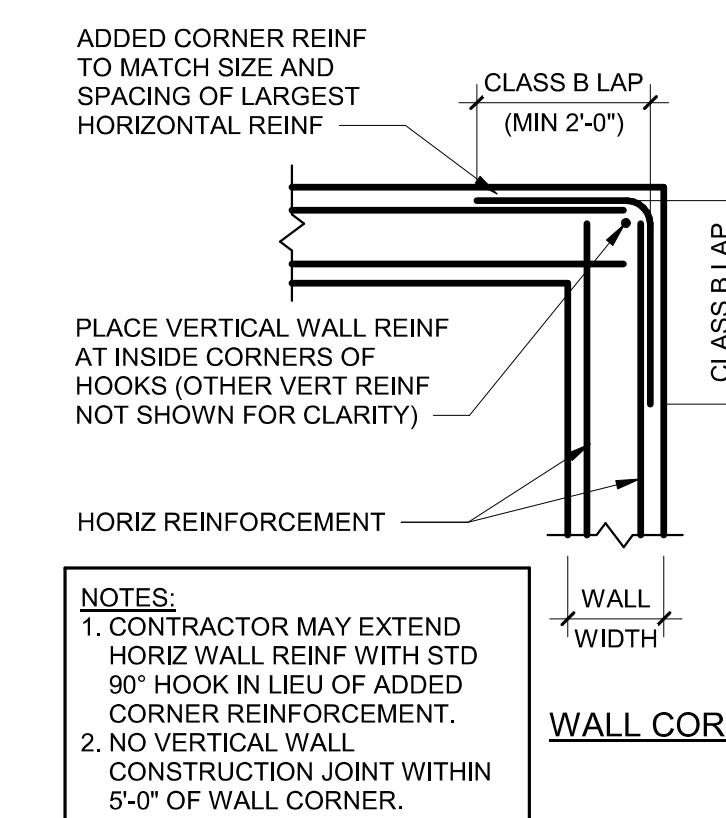

FOUNDATION LEGEND:

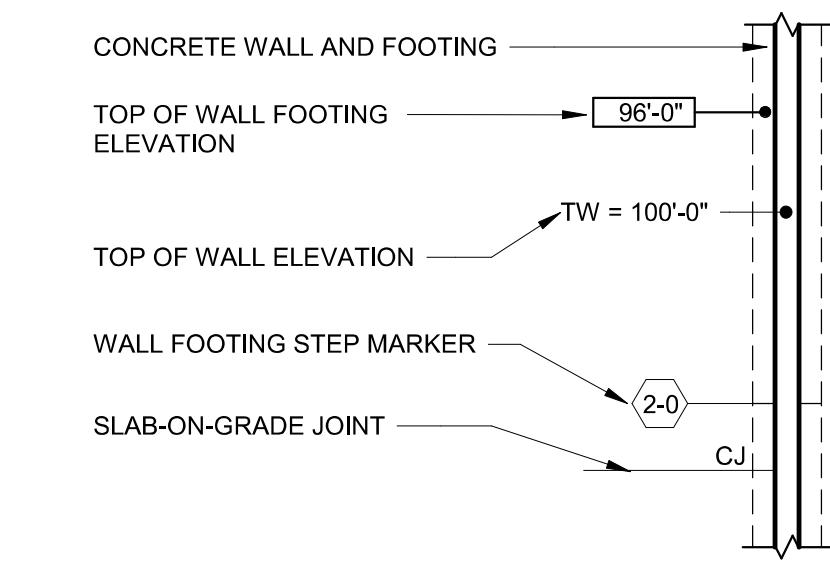


FLOOR PLAN GENERAL NOTES:

- SITE DATUM OF 959.85 = FLOOR EL. 101'-0" ON ARCHITECTURAL DRAWINGS.
- FIELD VERIFY ALL DIMENSIONS, BRING ANY DISCREPANCIES TO THE ATTENTION OF THE ARCHITECT / ENGINEER FOR FINAL DECISION.
- SEE SHEET A401 FOR DOOR SCHEDULE AND PARTITION TYPES.
- DIMENSIONS ON FLOOR PLAN ARE BASED ON FACE OF FINISH WALL TO FINISHED WALL (NOMINAL).
- REFER TO DEMOLITION SHEETS FOR COORDINATION OF DEMOLITION SCOPE.
- REFER TO MECHANICAL, ELECTRICAL, AND PLUMBING DRAWINGS FOR ADDITIONAL ITEMS AND NOTES.

KEYED NOTES


- 42" HIGH GALVANIZED METAL REMOVABLE GUARDRAIL, MOUNTED TO SIDE OF CONCRETE PIT WALL. MAXIMUM SECTION LENGTH OF 4'-0", SEE DETAIL 1/A111
- EXISTING HOLLOW METAL DOOR AND FRAME
- EXISTING STEEL COLUMNS TO REMAIN
- 24"X24" PAINTED ALUMINUM LOUVER, SEE DETAIL 3/A511
- METAL WINDOW WELL, ATTACH TO EXISTING CONCRETE FOUNDATION WALL. PROVIDE METAL GRATE COVER AND FILL BOTTOM 12' WITH CLEAR DRAINING FIL, SEE 1/A301 FOR HEIGHT AND LOCATION VERTICALLY FROM LOUVER OPENING
- EXISTING STONE VENEER ON CONCRETE FOUNDATION WALL AT BREWERY BUILDING
- 14" WIDE BOARD FORMED CONCRETE RETAINING WALL. SEE DETAIL 5/A411 FOR REINFORCING
- STRIP FOOTING, SEE DETAIL 5/A411 FOR REINFORCING
- PROVIDE EXPANSION JOINT AT EXISTING BREWERY BUILDING WHERE NEW FOUNDATION WALL ABUTS EXISTING BREWERY WALL
- 24" ROUND DRILLED PIER, 6'-0" DEEP, T/PIER = 99'-0" TYP, REINFORCE W/ (8) #6 VERT. AND #3 TIES @ 12' O.C. PROVIDE MOMENT RESISTANCE POST BASE CONNECTION WITH DRILLED PIER
- HUB DRAIN, SEE PLUMBING
- FLOOR CLEAN OUT, SEE PLUMBING
- FLOOR DRAIN, SEE PLUMBING

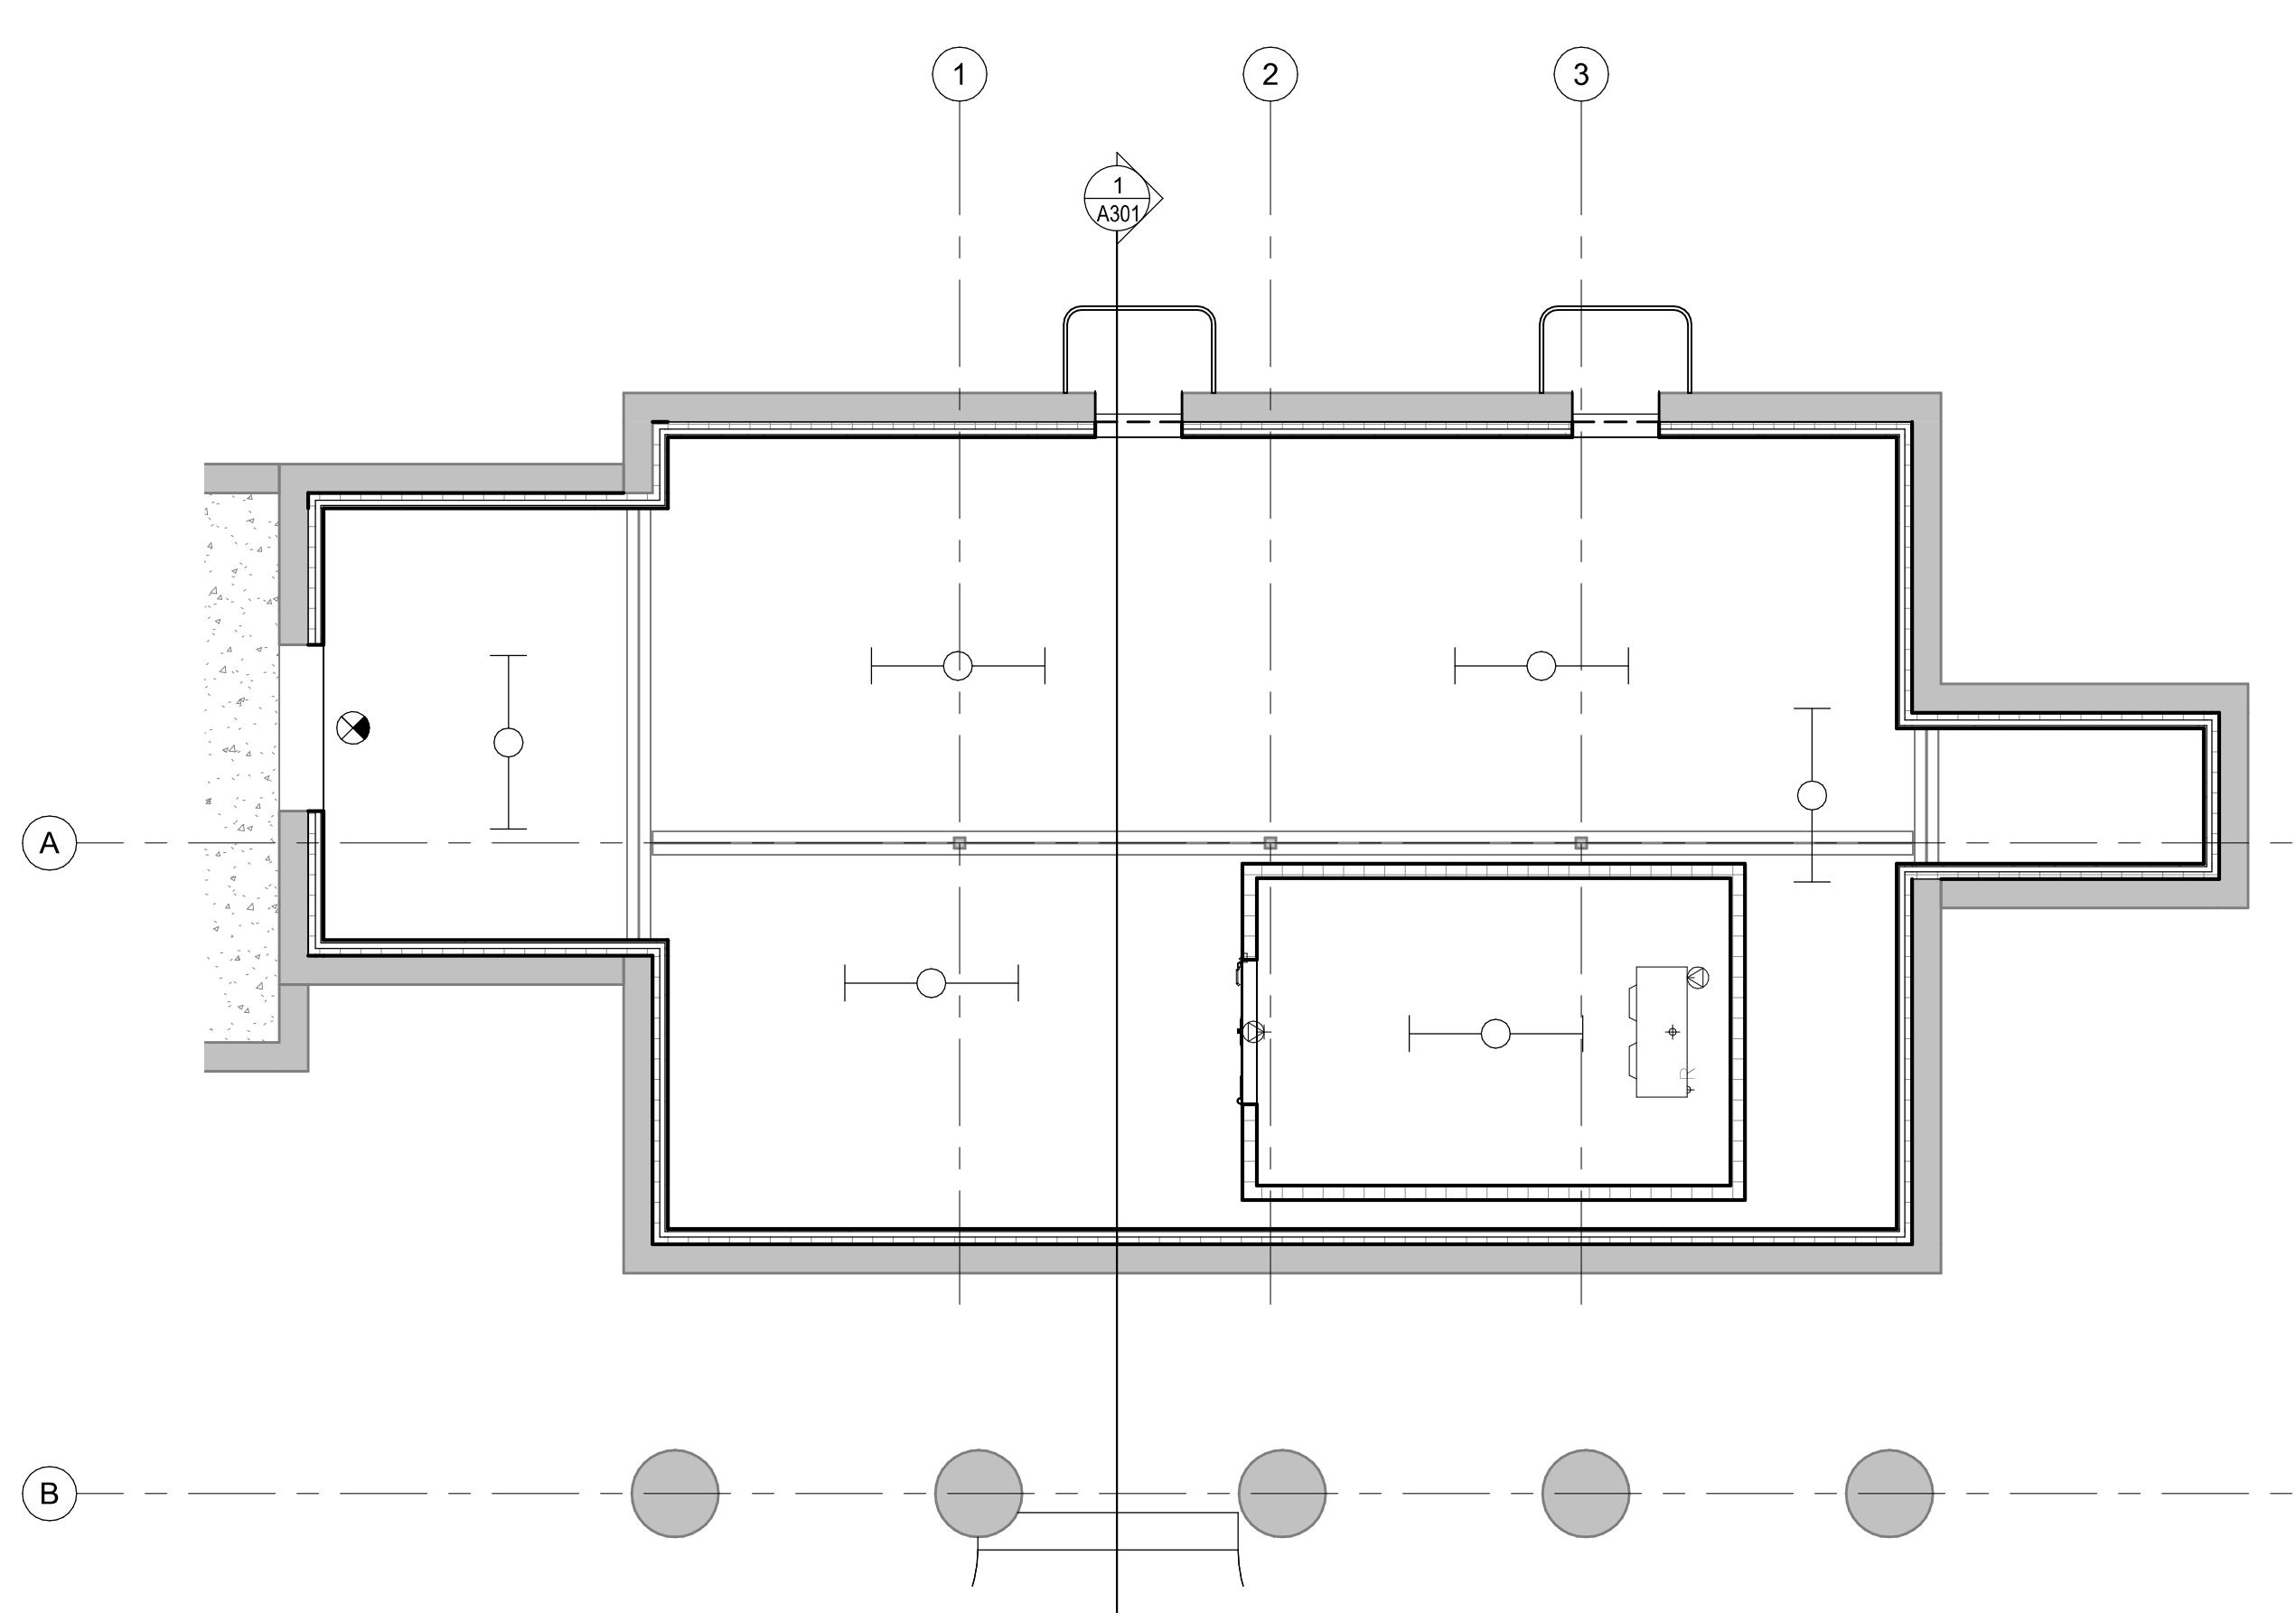

NORTH
2 TAVERN LOWER LEVEL CEILING PLAN

1/4" = 1'-0"

0 2 4 8

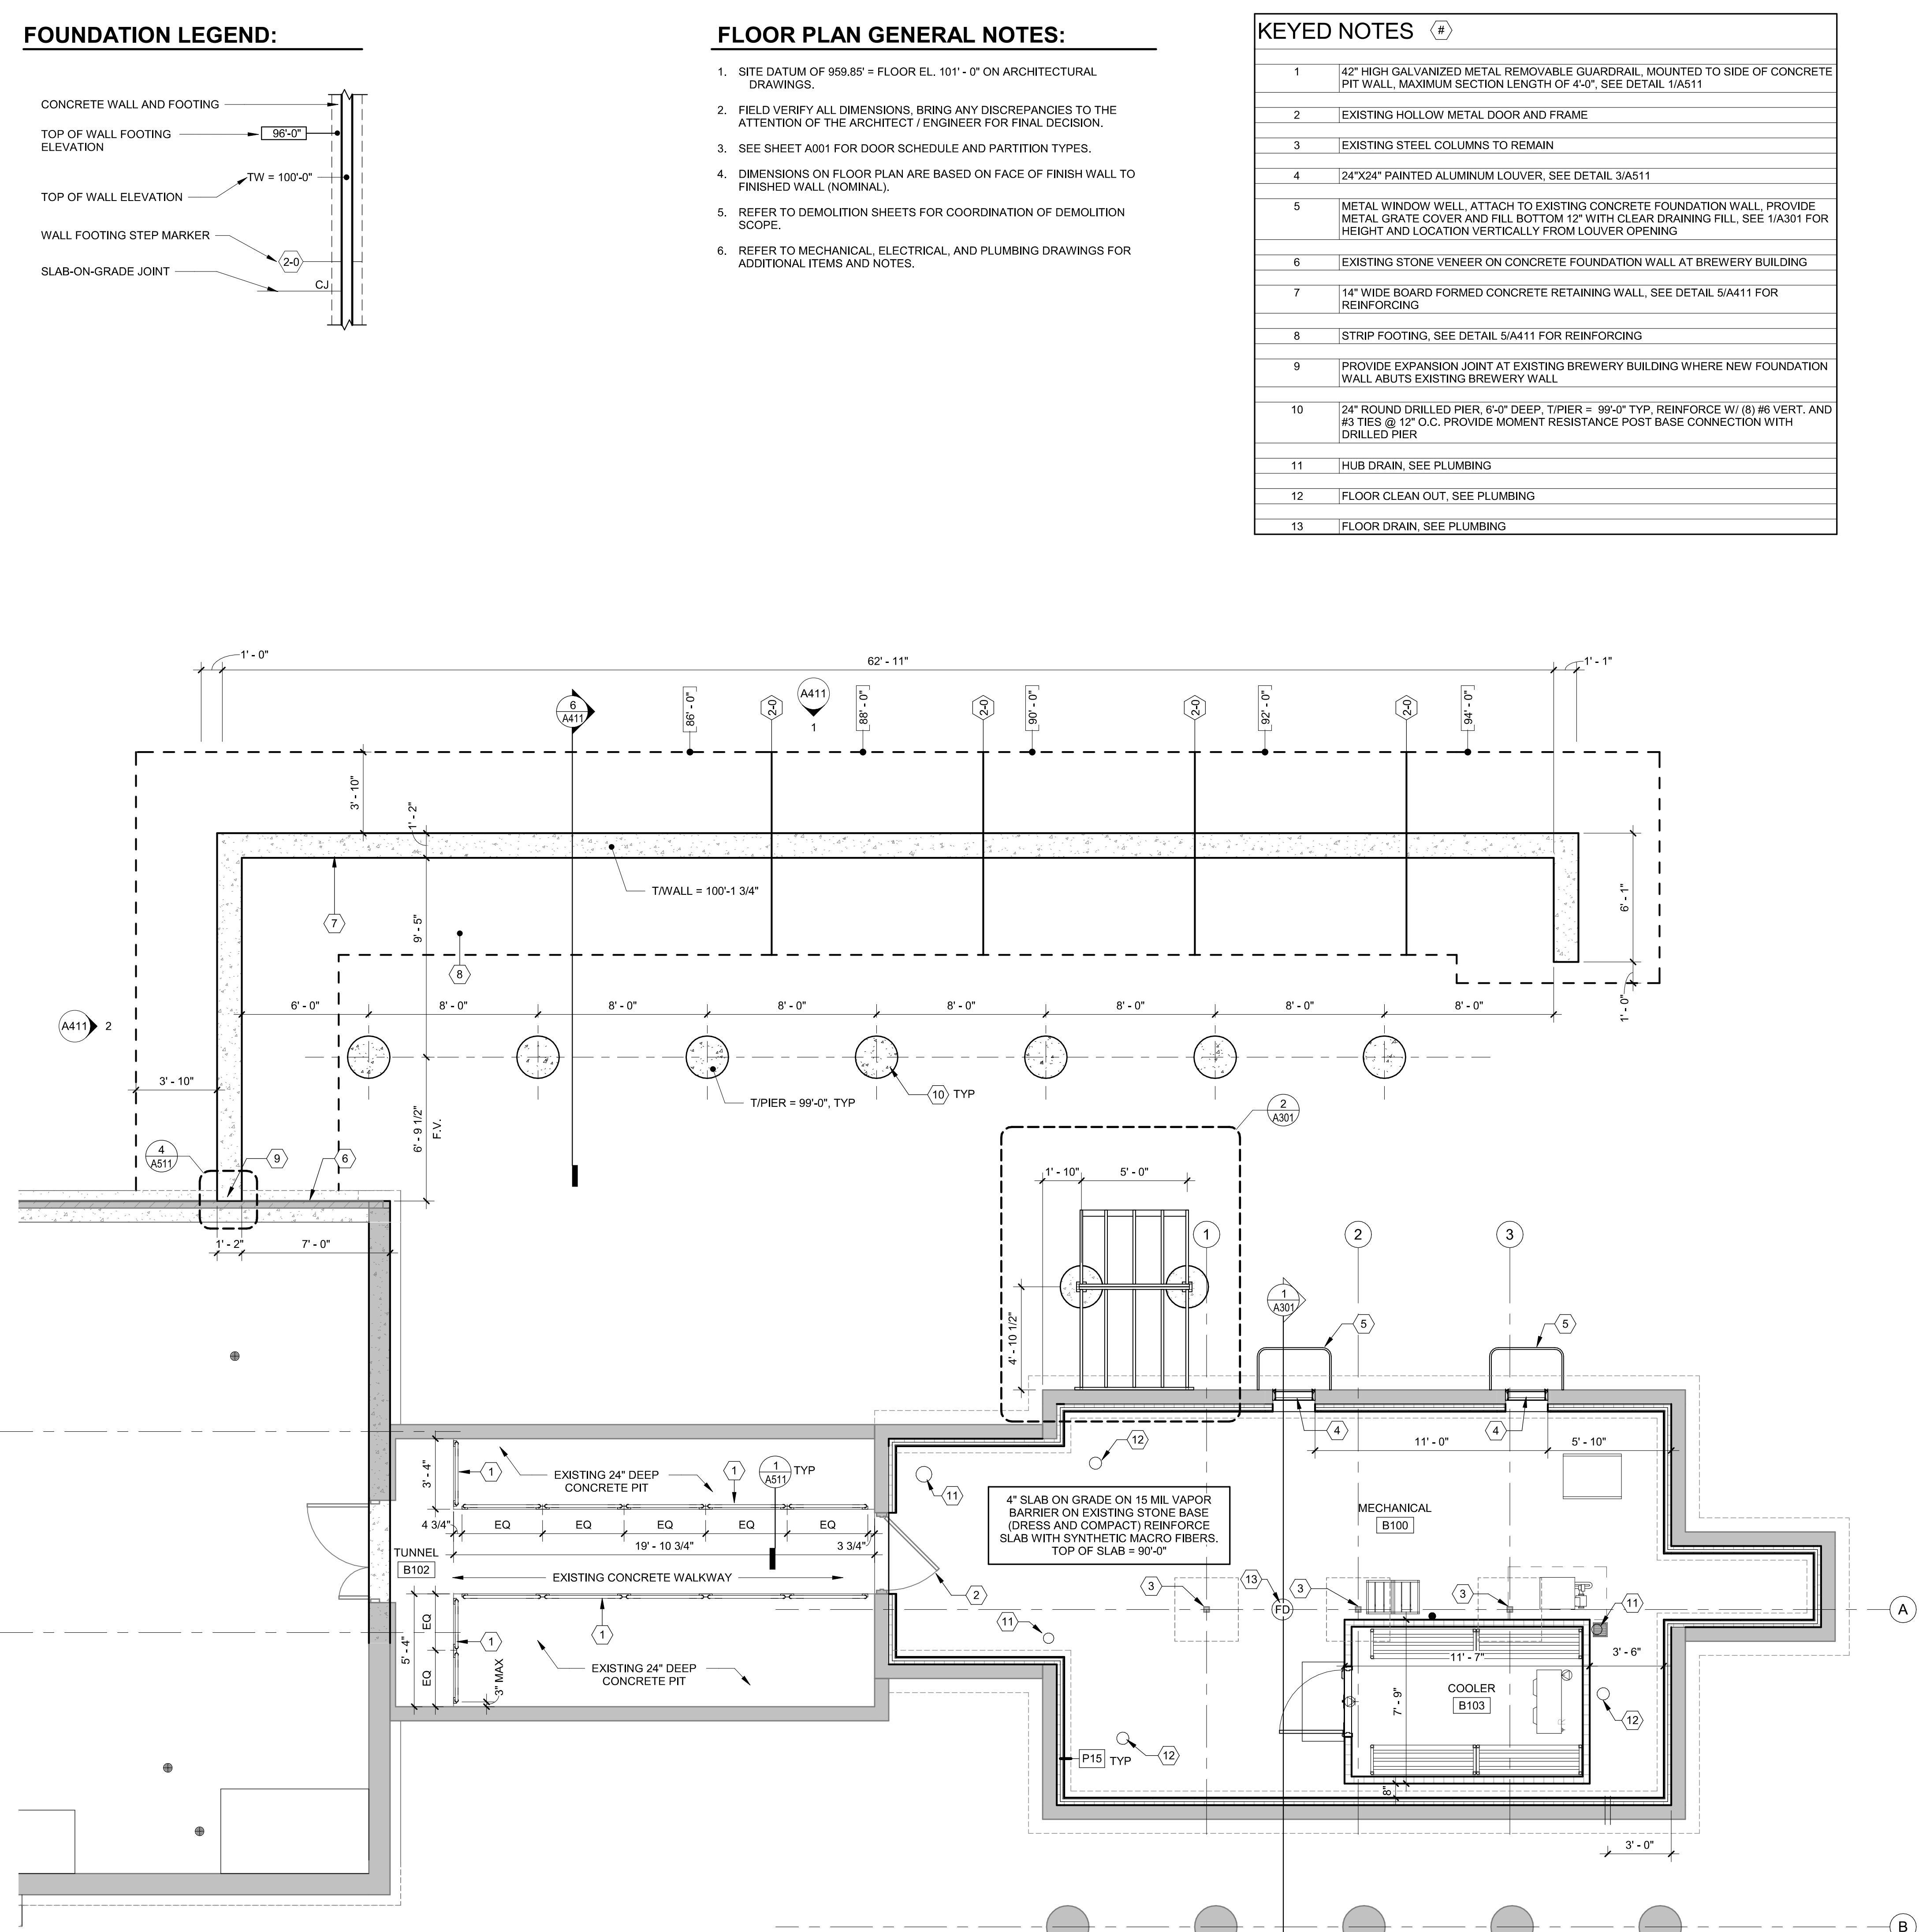

NORTH
1 TAVERN LOWER LEVEL FLOOR PLAN

0 2 4 8

State of Wisconsin
Department of Administration
Division of Facilities Development
 Old World Wisconsin Ethnic Outdoor Museum
Town of Eagle, Wisconsin


Old World Wisconsin Ethnic Outdoor Museum
Town of Eagle, Wisconsin

Tavern Renovations
Old World Wisconsin Ethnic Outdoor Museum
Wisconsin Historical Society
Town of Eagle, Wisconsin

Sheet Title:
TAVERN LOWER LEVEL PLANS

Revisions:
No. Date: Description:

Graphic Scale	See Details
DFD Number	1711K-04
Set Type	BD
Date Issued	9/8/2023
Sheet Number	A111

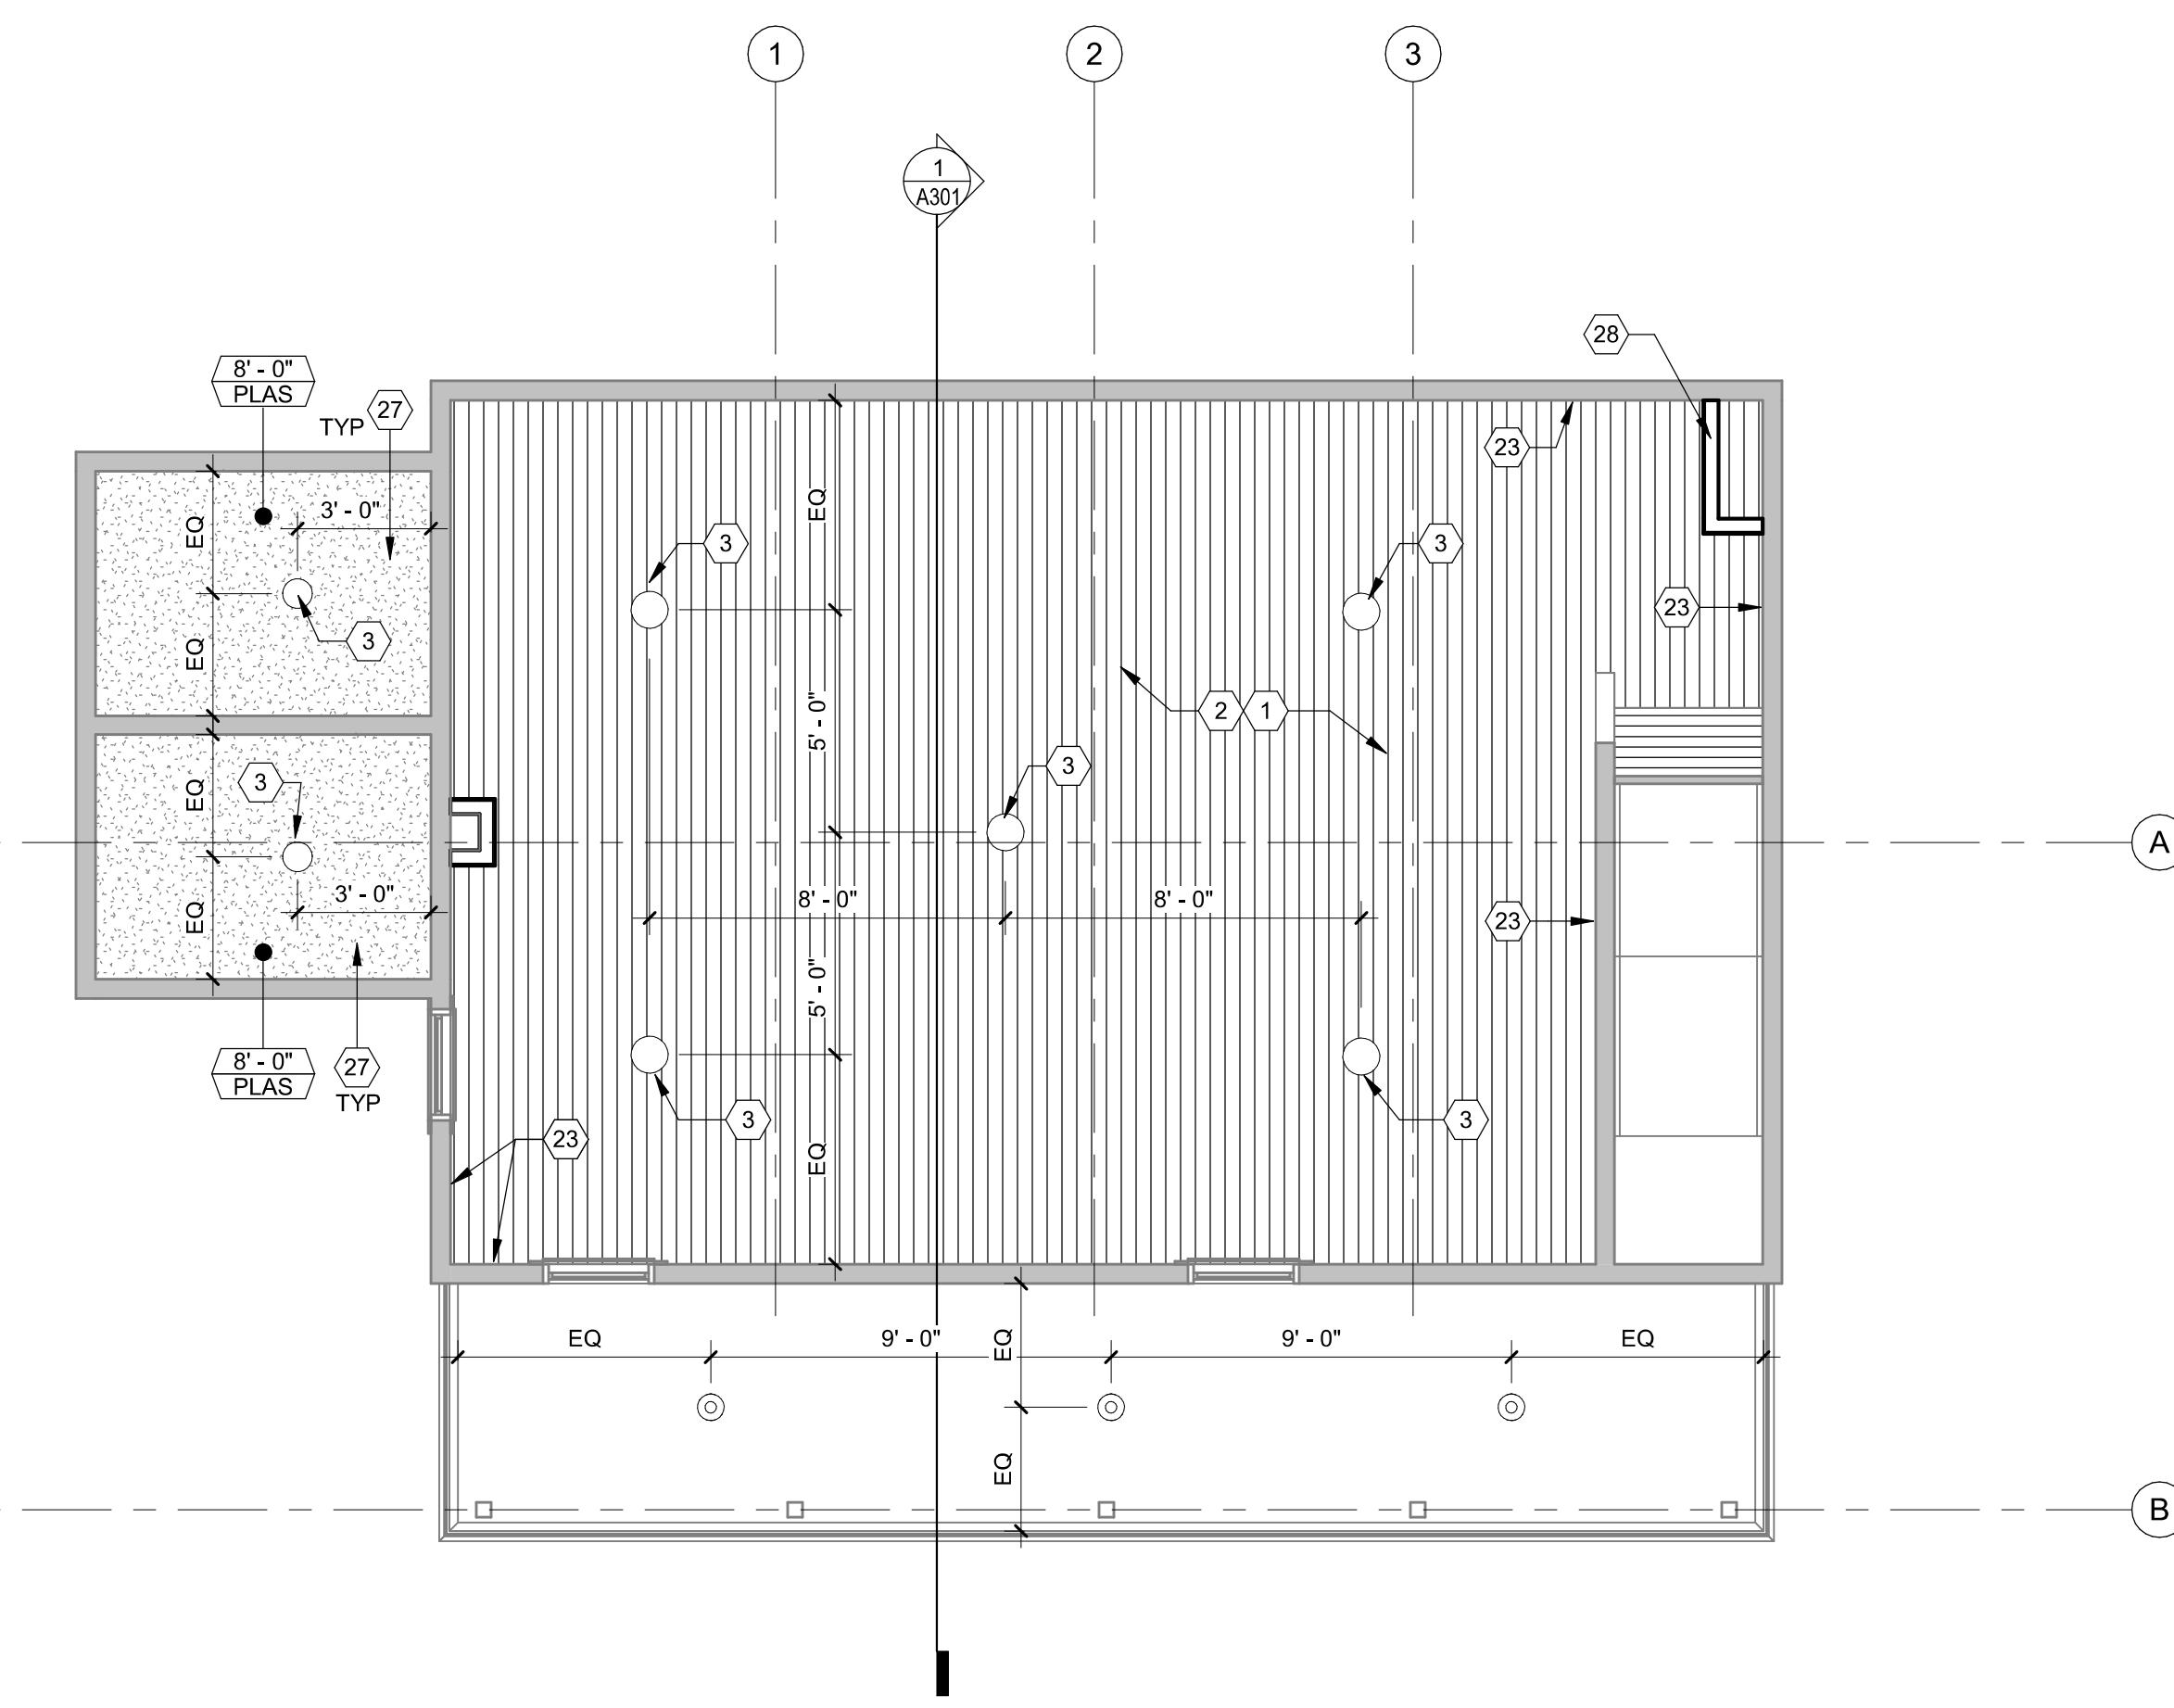

NORTH
2 TAVERN FIRST FLOOR CEILING PLAN
1/4" = 1'-0"

CEILING GENERAL NOTES:

- REFER TO A115 FOR FINISH PLANS AND MATERIAL SCHEDULES.
- REFER TO MEP DRAWINGS, SPECIFICATIONS, AND SCHEDULES FOR TYPE AND QUANTITY OF FIXTURES AND EQUIPMENT SHOWN ON THIS PLAN.
- RCP'S INDICATE LAYOUT ONLY. REFER TO ELECTRICAL DRAWINGS FOR ADDITIONAL INFORMATION.
- ALL METAL LINEAR DIFFUSERS AND SHOP PRIMED ACCESS PANELS SHALL BE PAINTED TO MATCH SURROUNDING WALL OR CEILING SURFACE.
- REFER TO DEMOLITION SHEETS FOR COORDINATION OF DEMOLITION SCOPE.
- REFER TO MECHANICAL, ELECTRICAL, AND PLUMBING DRAWINGS FOR ADDITIONAL ITEMS AND NOTES.

FLOOR PLAN GENERAL NOTES:

- SITE DATUM OF 959.85' = FLOOR EL. 101 - 0" ON ARCHITECTURAL DRAWINGS.
- FIELD VERIFY ALL DIMENSIONS, BRING ANY DISCREPANCIES TO THE ATTENTION OF THE ARCHITECT / ENGINEER FOR FINAL DECISION.
- SEE SHEET A001 FOR DOOR SCHEDULE AND PARTITION TYPES.
- DIMENSIONS ON FLOOR PLAN ARE BASED ON FACE OF FINISH WALL TO FINISHED WALL (NOMINAL).
- REFER TO DEMOLITION SHEETS FOR COORDINATION OF DEMOLITION SCOPE.
- REFER TO MECHANICAL, ELECTRICAL, AND PLUMBING DRAWINGS FOR ADDITIONAL ITEMS AND NOTES.

KEYED NOTES #


- PREP EXISTING WOOD TONGUE AND GROOVE CEILING, BY REMOVING ANY FLAKING PAINT AND SANDING SMOOTH, PAINT PT-2
- REPAIR TONGUE AND GROOVE WOOD CEILING AT DEMOLISHED CEILING LIGHTS AND WHERE REMOVED TO INSTALL NEW LIGHTING AS NEEDED
- CEILING MOUNTED LIGHT
- INSTALL NEW 1 1/2" DIAMETER WOOD HANDRAIL ON EXISTING HANDRAIL BRACKETS, PROVIDE ADDITIONAL BRACKET ON EXISTING GUARDRAIL TO EXTEND HANDRAIL TO THE TOP STRINGER
- RESTORE AND REINSTALL OWNER PROVIDED WOOD WAINSCOTING AND TRIM, OFCI
- RESTORE AND REINSTALL OWNER PROVIDED WOOD WALL BASE AS WELL AS EXISTING WALL BASE REMOVED DURING DEMOLITION, REPAIR OR REPLACE WITH WALL BASE TO MATCH SIZE AND COLOR AS NEEDED.
- INSTALL BATT INSULATION IN EXISTING EXTERIOR/ INTERIOR WALL CAVITY, VAPOR BARRIER, PLYWOOD SHEATHING AND GWB WITH PLASTER VENEER ON EXTERIOR FACE OF WALL, SEE PARTITION TYPE P16A
- REINSTALL EXISTING WOOD TOILET PARTITIONS
- PROVIDE WOODEN THRESHOLD AT GAP BETWEEN CONCRETE BATHROOM FLOOR AND WOOD TAVERN FLOOR, DIFFERENCE IN HEIGHT IS APPROXIMATELY 2", STAIN TO MATCH BATHROOM DOOR TRIM COLOR
- RESTORE AND REINSTALL OWNER PROVIDED WOOD BATHROOM DOORS AND HARDWARE, FIELD VERIFY FIT, BOTTOM OF DOOR MAY NEED TO BE TRIMMED AS MAIN ROOM AND TOILET ROOM FLOORS ARE NO LONGER LEVEL, SEAL BOTTOM OF DOOR IF TRIMMING IS NEEDED
- PAINT EXISTING CONCRETE FLOOR, PT-7

- REINSTALL OWNER PROVIDED HISTORIC BAR, OFCI
- REINSTALL OWNER PROVIDED HISTORIC BACK BAR AND MIRROR, OFCI
- REINSTALL OWNER PROVIDED HISTORIC COOLER PANELS, OFCI
- INSTALL NEW 1 1/2" DIAMETER WOOD HANDRAIL ON NEW WALL MOUNTED HANDRAIL BRACKETS
- NEW MECHANICAL WALL GRILL IN DEMOLISHED WALL LOCATION, LOCATE GRILL AT FLOOR SIMILAR TO GRILLS ON EAST WALL
- NEW FOODSERVICE EQUIPMENT INSTALLED BEHIND EXISTING OWNER PROVIDED HISTORIC WOOD BAR, SEE FOODSERVICE PLAN
- INSTALL OWNER PROVIDED WOOD DOOR AND FRAME IN LOCATION INDICATED ON PLAN. MODIFY EXTERIOR WOOD WALL FRAMING TO ACCEPT DOOR, DO NOT CUT DOOR OPENING THROUGH TO THE EXTERIOR WALL, THIS IS NOT INTENDED TO BE AN OPERABLE DOOR
- STAIN INTERIOR FACE OF EXTERIOR DOORS TO MATCH EXISTING WOOD TRIM, REINSTALL EXISTING HARDWARE AND REINSTALL DOOR IN EXISTING FRAME
- 6X6 PRESSURE TREATED WOOD COLUMNS, PAINTED
- 14" WIDE BOARD FORMED CONCRETE RETAINING WALL, SEE DETAIL 5/A411 FOR REINFORCING
- METAL WINDOW WELL, ATTACH TO EXISTING CONCRETE FOUNDATION WALL, PROVIDE METAL GRATE COVER AND FILL BOTTOM 12" WITH CLEAR DRAINING FILL, SEE 1/A301 FOR HEIGHT AND LOCATION VERTICALLY FROM LOUVER OPENING
- INSTALL NEW QUARTER ROUND TRIM, WD-3, AT CEILING TO WALL TRANSITION, PAINT PT-2
- CONCRETE SLAB ON GRADE, SEE LANDSCAPING PLANS FOR EXTENT
- NEW WOOD BARN DOORS IN EXISTING OPENING, REUSE EXISTING HARDWARE AND ALL FLASHING AND SWEEPS, REPLACE DOOR PANELS AS SCHEDULED (2) BARN DOORS TOTAL, SEE A001 FOR SCHEDULE INFORMATION
- WOOD GUARDRAILS, SEE DETAIL 7/A411
- REPAIR EXISTING HOLES OR CRACKS IN PLASTER CEILING
- NEW WALLS TO UNDERSIDE OF EXISTING CEILING, CEILING TO REMAIN
- INSTALL OFCI WOOD WAINSCOTING AND TRIM AT NEW WALLS
- EDGE OF SUNSHADE STRUCTURE ABOVE
- NEW WOOD BREWERY DOOR IN EXISTING OPENING, REUSE EXISTING HARDWARE AND ALL FLASHING AND SWEEPS, REPLACE DOOR PANEL AS SCHEDULED (1) MAN DOOR TOTAL, SEE A001 FOR SCHEDULE INFORMATION


Tavern Renovations
Old World Wisconsin Ethnic Outdoor Museum
Wisconsin Historical Society
Town of Eagle, Wisconsin

Sheet Title: TAVERN FIRST FLOOR PLANS

Revisions:		
No.	Date:	Description:
Graphic Scale		
See Details		
DFD Number		
171K-04		
Set Type		
BD		
Date Issued		
9/8/2023		
Sheet Number		
A112		

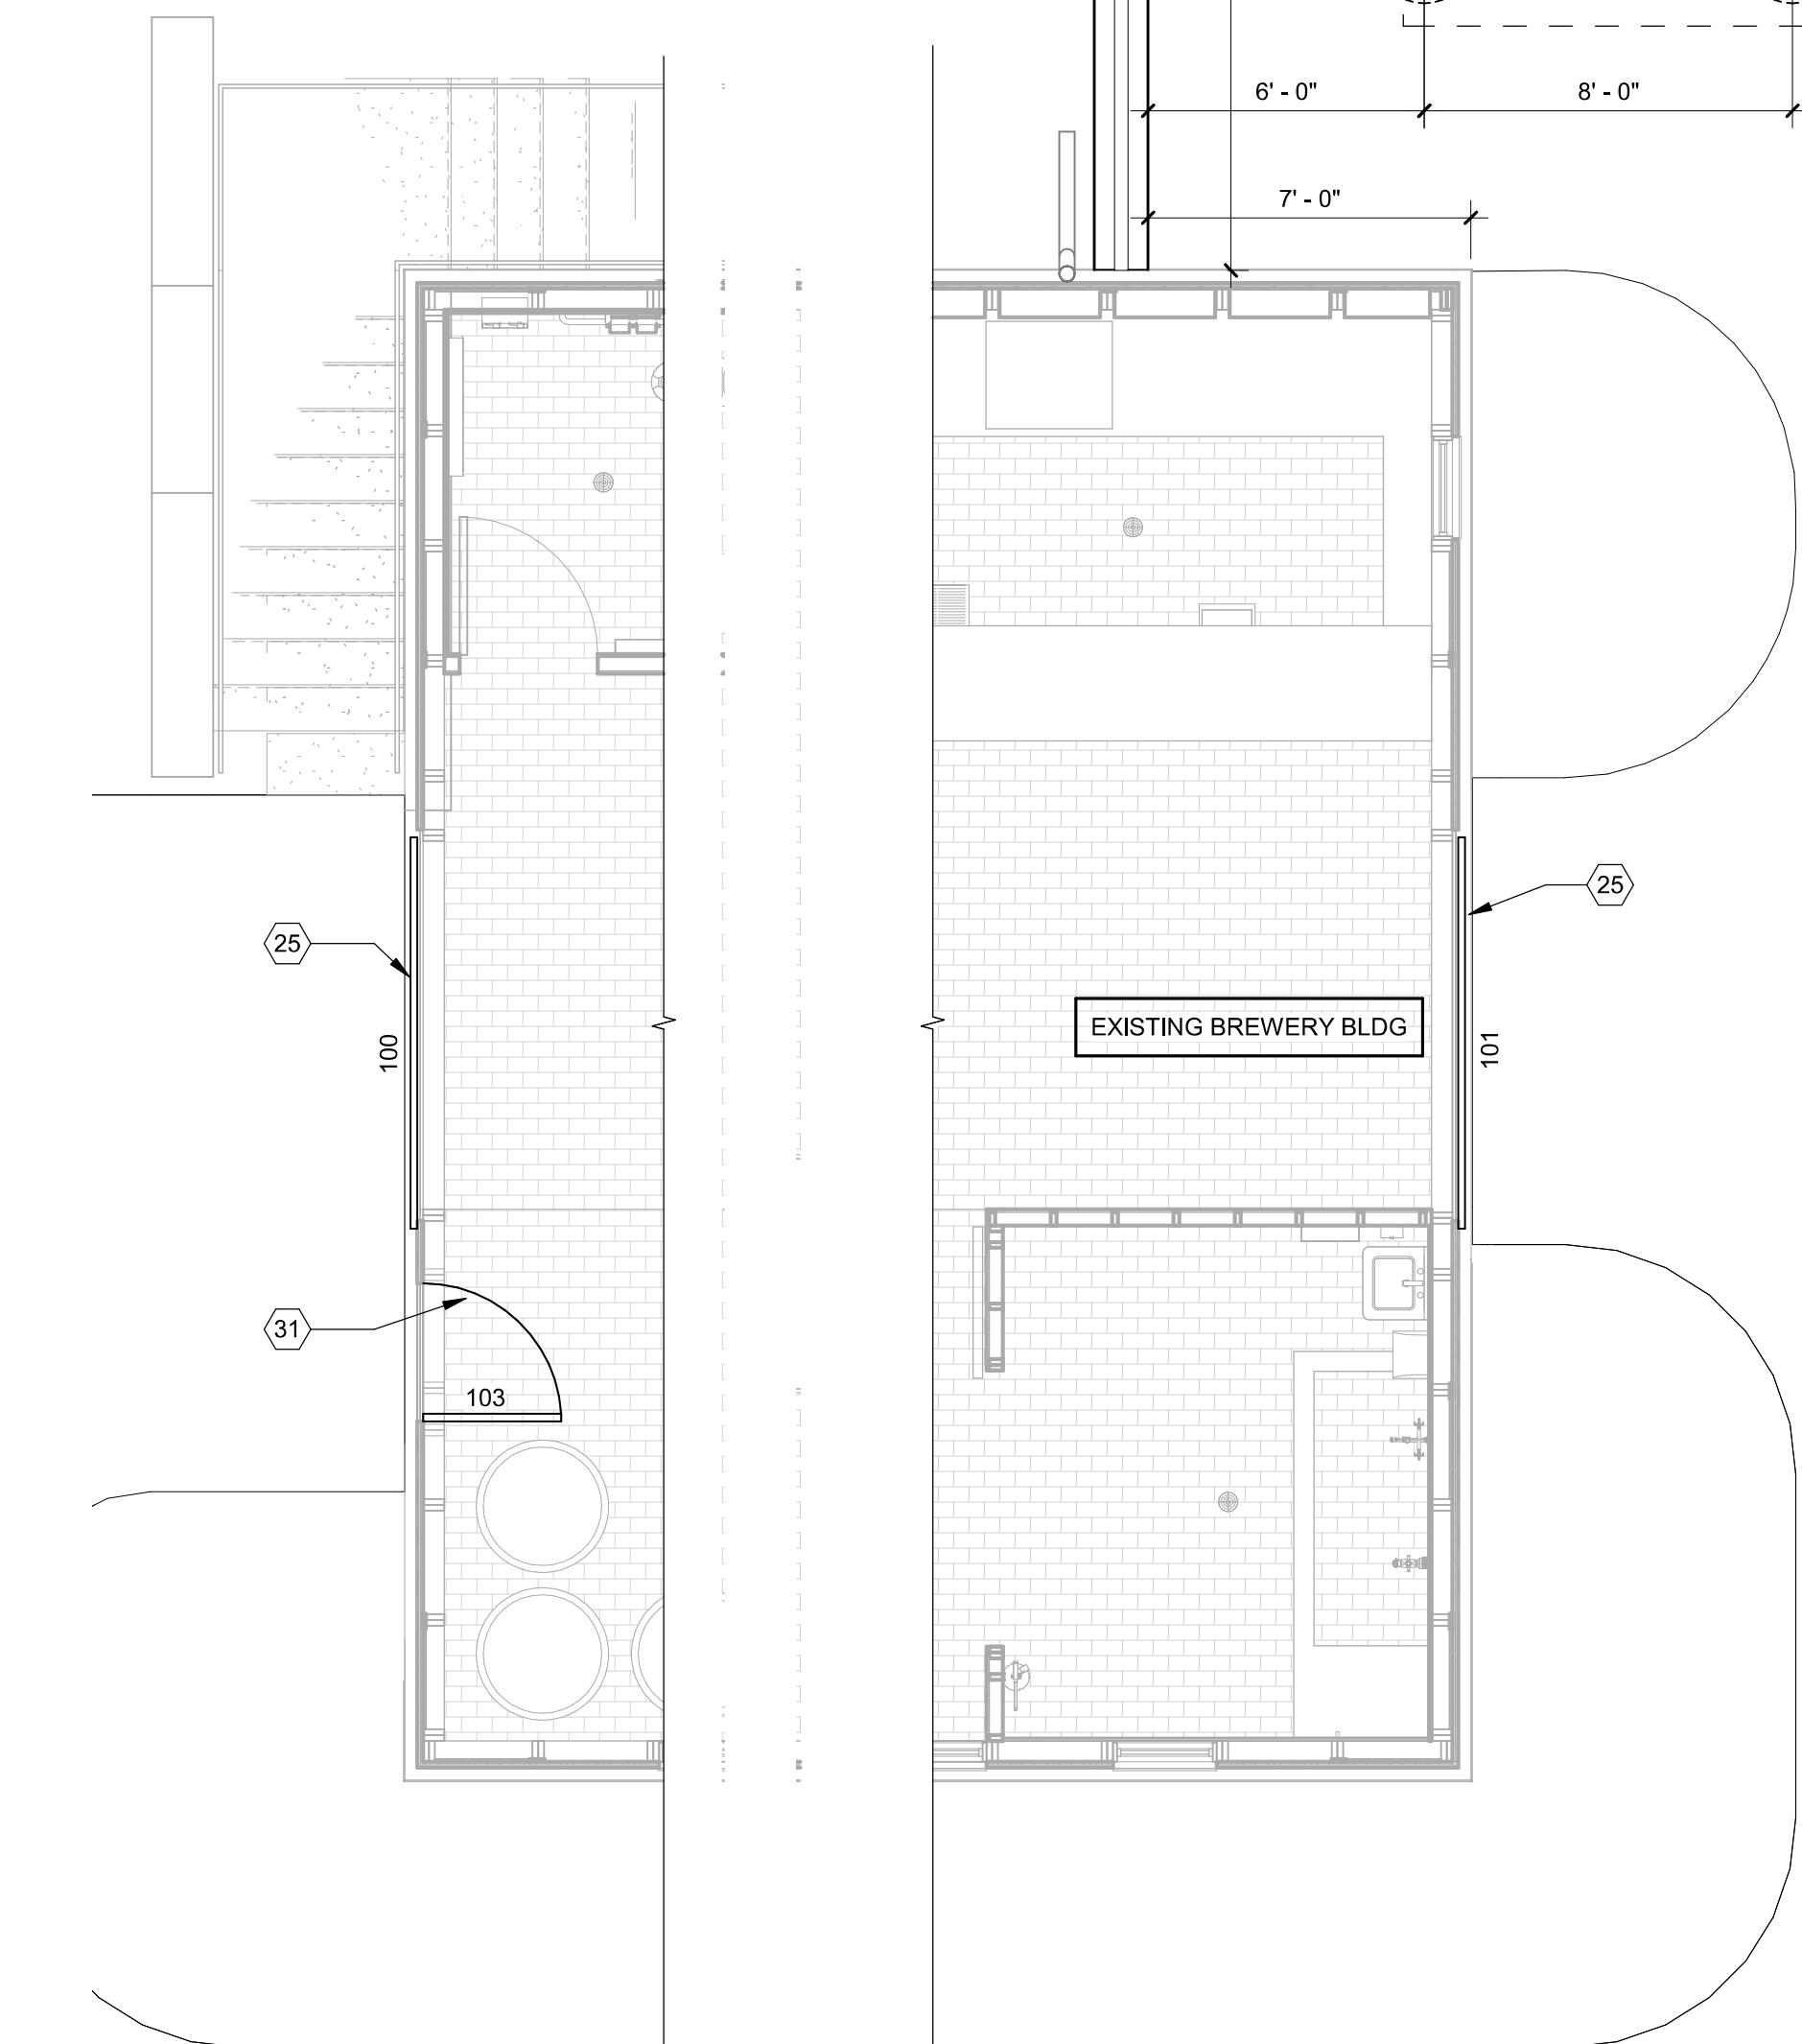

NORTH
1 TAVERN FIRST FLOOR PLAN
1/4" = 1'-0"

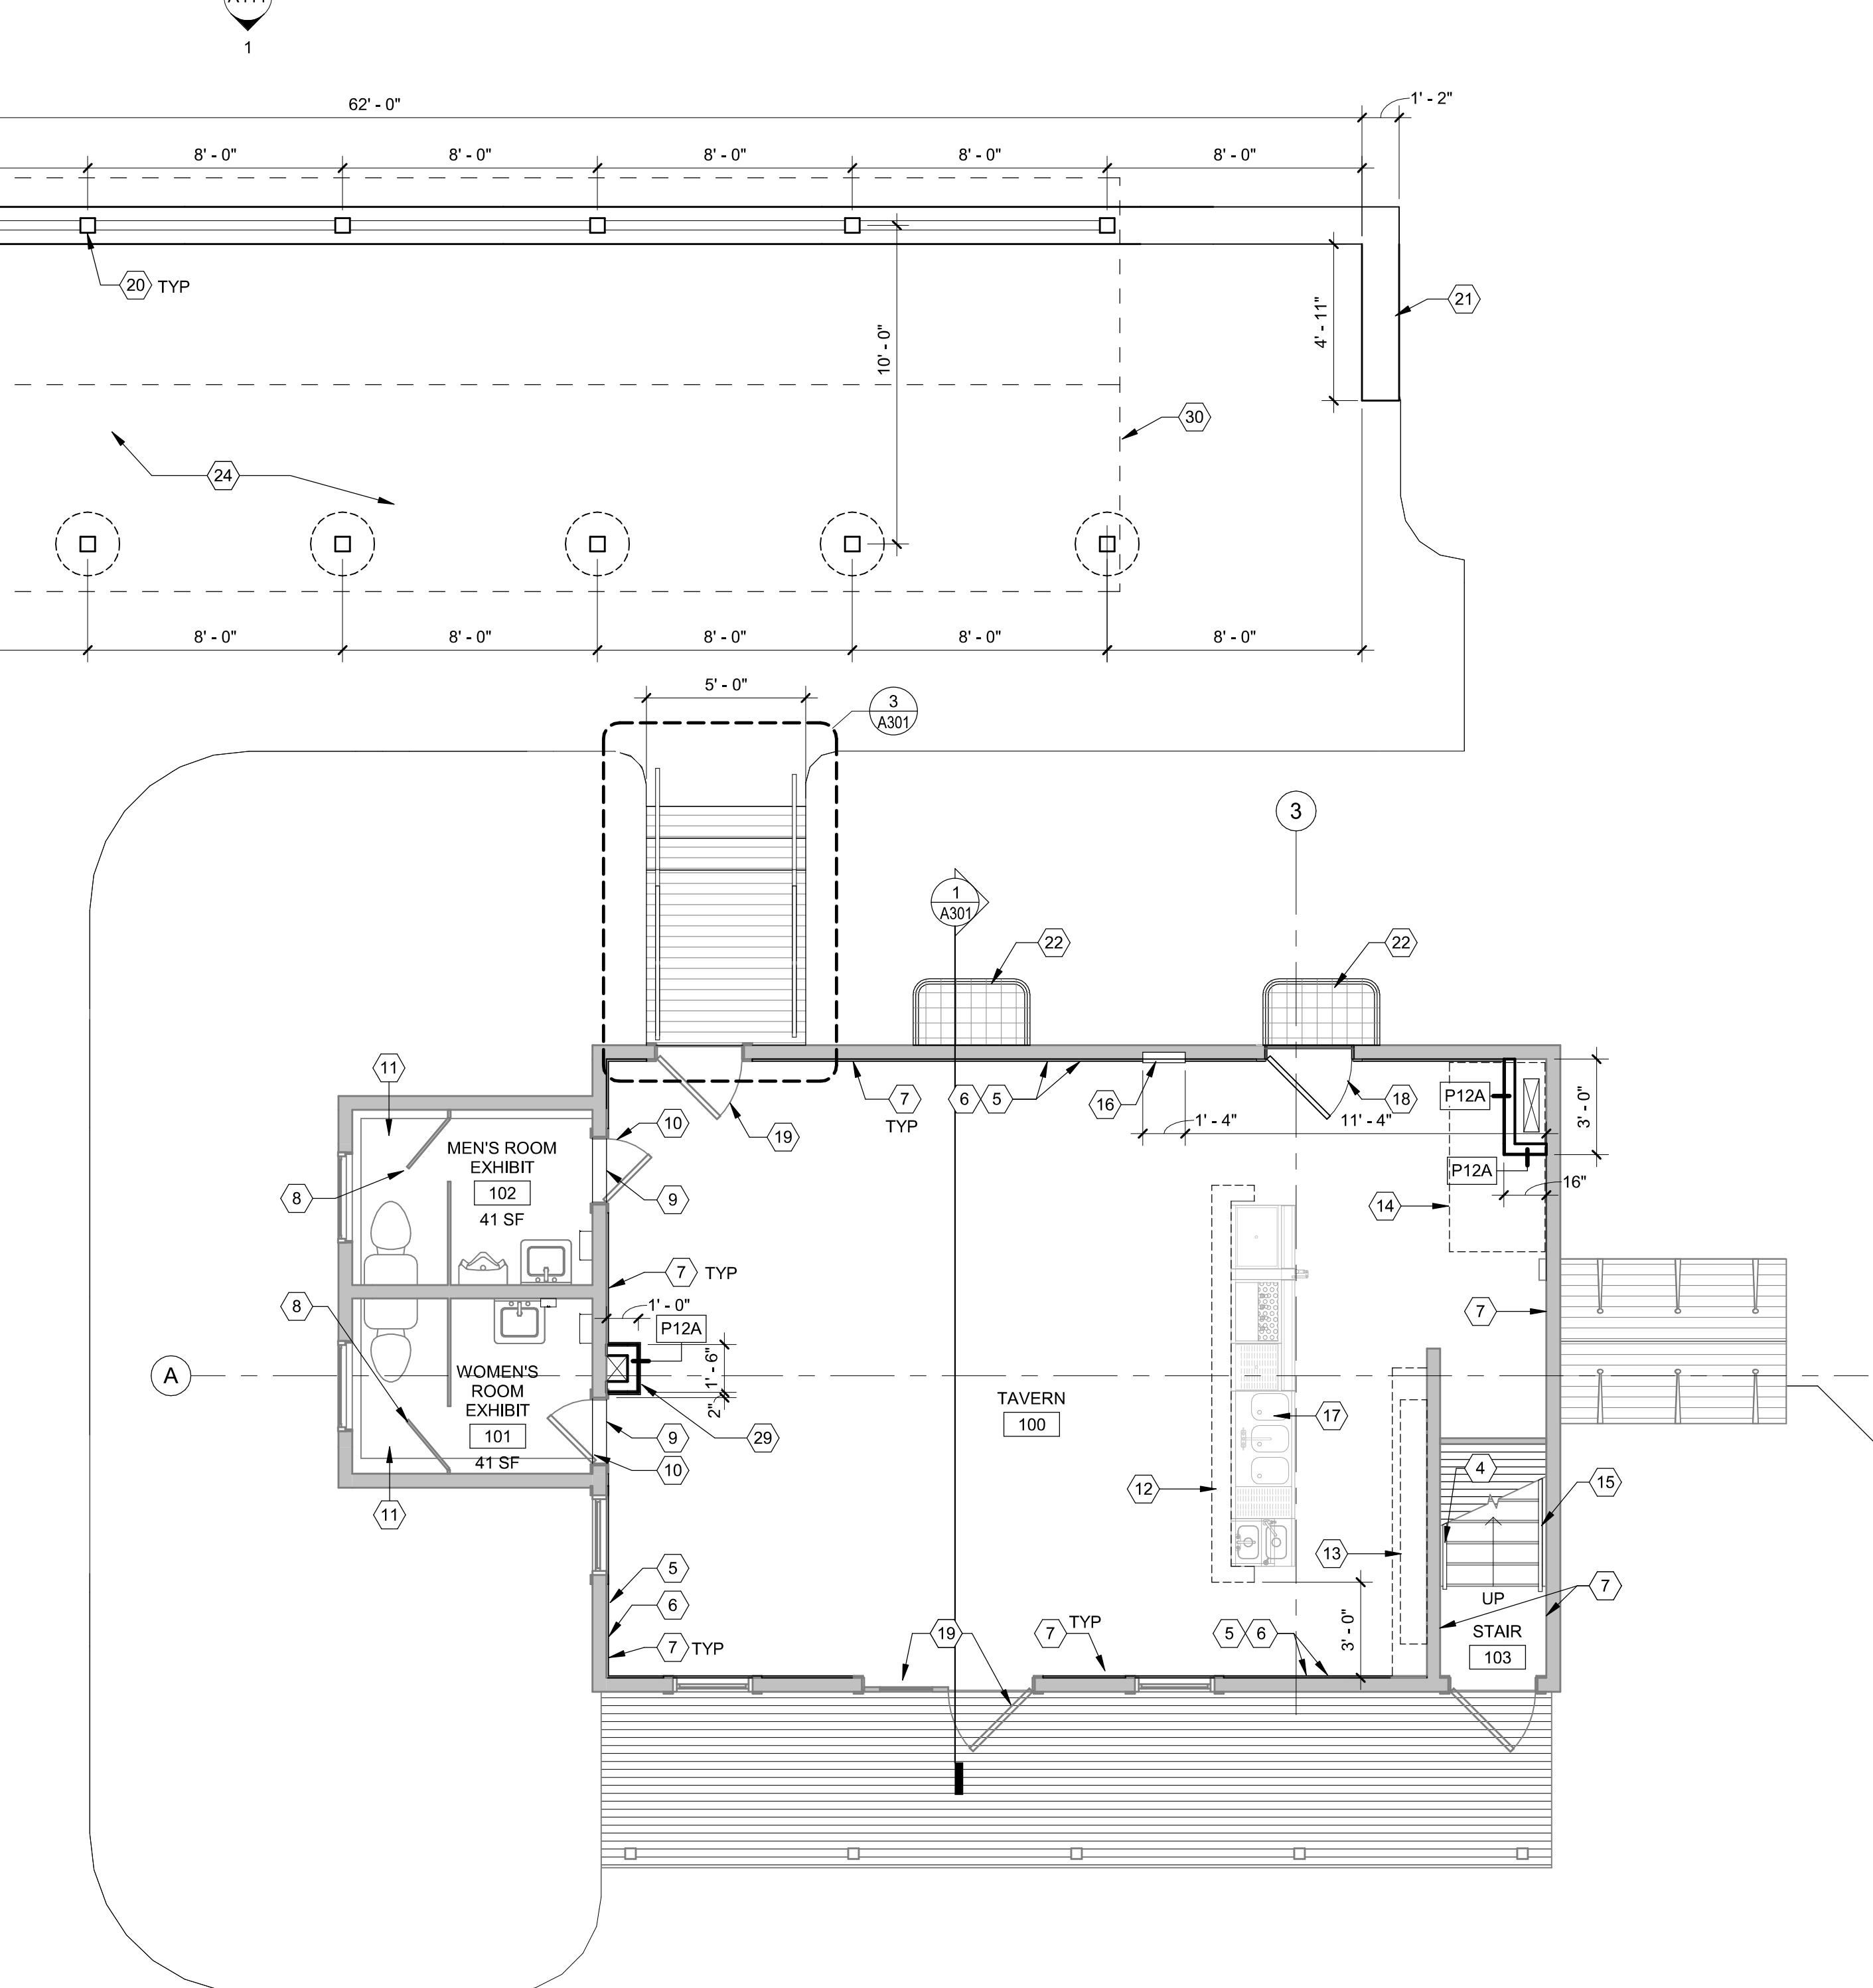

NORTH
1 TAVERN FIRST FLOOR PLAN
1/4" = 1'-0"

ARO EBERLE ARCHITECTS
433 W. Washington Ave.
Suite 400
Madison, WI 53703
(608) 204-7464
AroEberle.com

Consultant:

Old World Wisconsin Ethnic Outdoor Museum
Town of Eagle, Wisconsin

Consultant:

FLOOR PLAN GENERAL NOTES:

1. SITE DATUM OF 859.85' = FLOOR EL. 101'-0" ON ARCHITECTURAL DRAWINGS.
2. FIELD VERIFY ALL DIMENSIONS, BRING ANY DISCREPANCIES TO THE ATTENTION OF THE ARCHITECT / ENGINEER FOR FINAL DECISION.
3. SEE SHEET A001 FOR DOOR SCHEDULE AND PARTITION TYPES.
4. DIMENSIONS ON FLOOR PLAN ARE BASED ON FACE OF FINISH WALL TO FINISHED WALL (NOMINAL).
5. REFER TO DEMOLITION SHEETS FOR COORDINATION OF DEMOLITION SCOPE.
6. REFER TO MECHANICAL, ELECTRICAL, AND PLUMBING DRAWINGS FOR ADDITIONAL ITEMS AND NOTES.




CEILING GENERAL NOTES:

1. REFER TO A115 FOR FINISH PLANS AND MATERIAL SCHEDULES.
2. REFER TO MEP DRAWINGS, SPECIFICATIONS, AND SCHEDULES FOR TYPE AND QUANTITY OF FIXTURES AND EQUIPMENT SHOWN ON THIS PLAN.
3. RCP'S INDICATE LAYOUT ONLY. REFER TO ELECTRICAL DRAWINGS FOR ADDITIONAL INFORMATION.
4. ALL METAL LINEAR DIFFUSERS AND SHOP PRIMED ACCESS PANELS SHALL BE PAINTED TO MATCH SURROUNDING WALL OR CEILING SURFACE.

CEILING LEGEND:

	PLASTER CEILING (PAINTED)
	SURFACE MOUNTED LIGHT FIXTURE
	SUPPLY AIR DIFFUSER
	RETURN AIR DIFFUSER / EXHAUST GRILL
	EXHAUST FAN
	RECESSED CAN LIGHT
	INDUSTRIAL FLUORESCENT
	CEILING MOUNTED EXIT LIGHT
	JUNCTION BOX
	SMOKE DETECTOR
	WIRELESS ACCESS POINT
	9'-0" ACP-1 CEILING HEIGHT / MATERIAL

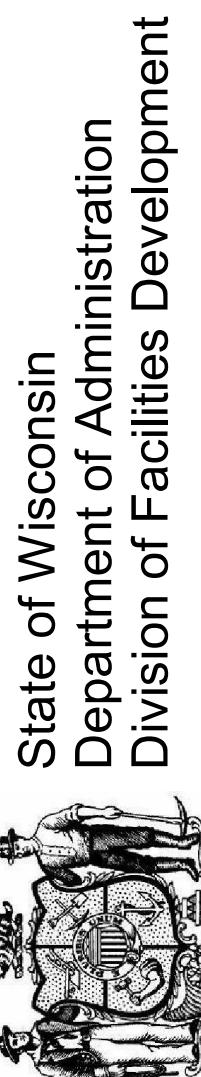

State of Wisconsin
Department of Administration
Division of Facilities Development

Town of Eagle, Wisconsin

Old World Wisconsin Ethnic Outdoor Museum

Tavern Renovations Old World Wisconsin Ethnic Outdoor Museum Wisconsin Historical Society Town of Eagle, Wisconsin

Sheet Title: TAVERN SECOND FLOOR AND ATTIC PLANS

Revisions:

No. Date Description:

Graphic Scale

See Details

DFD Number

1711K-04

Set Type





BD

Date Issued

9/8/2023


Sheet Number

A113

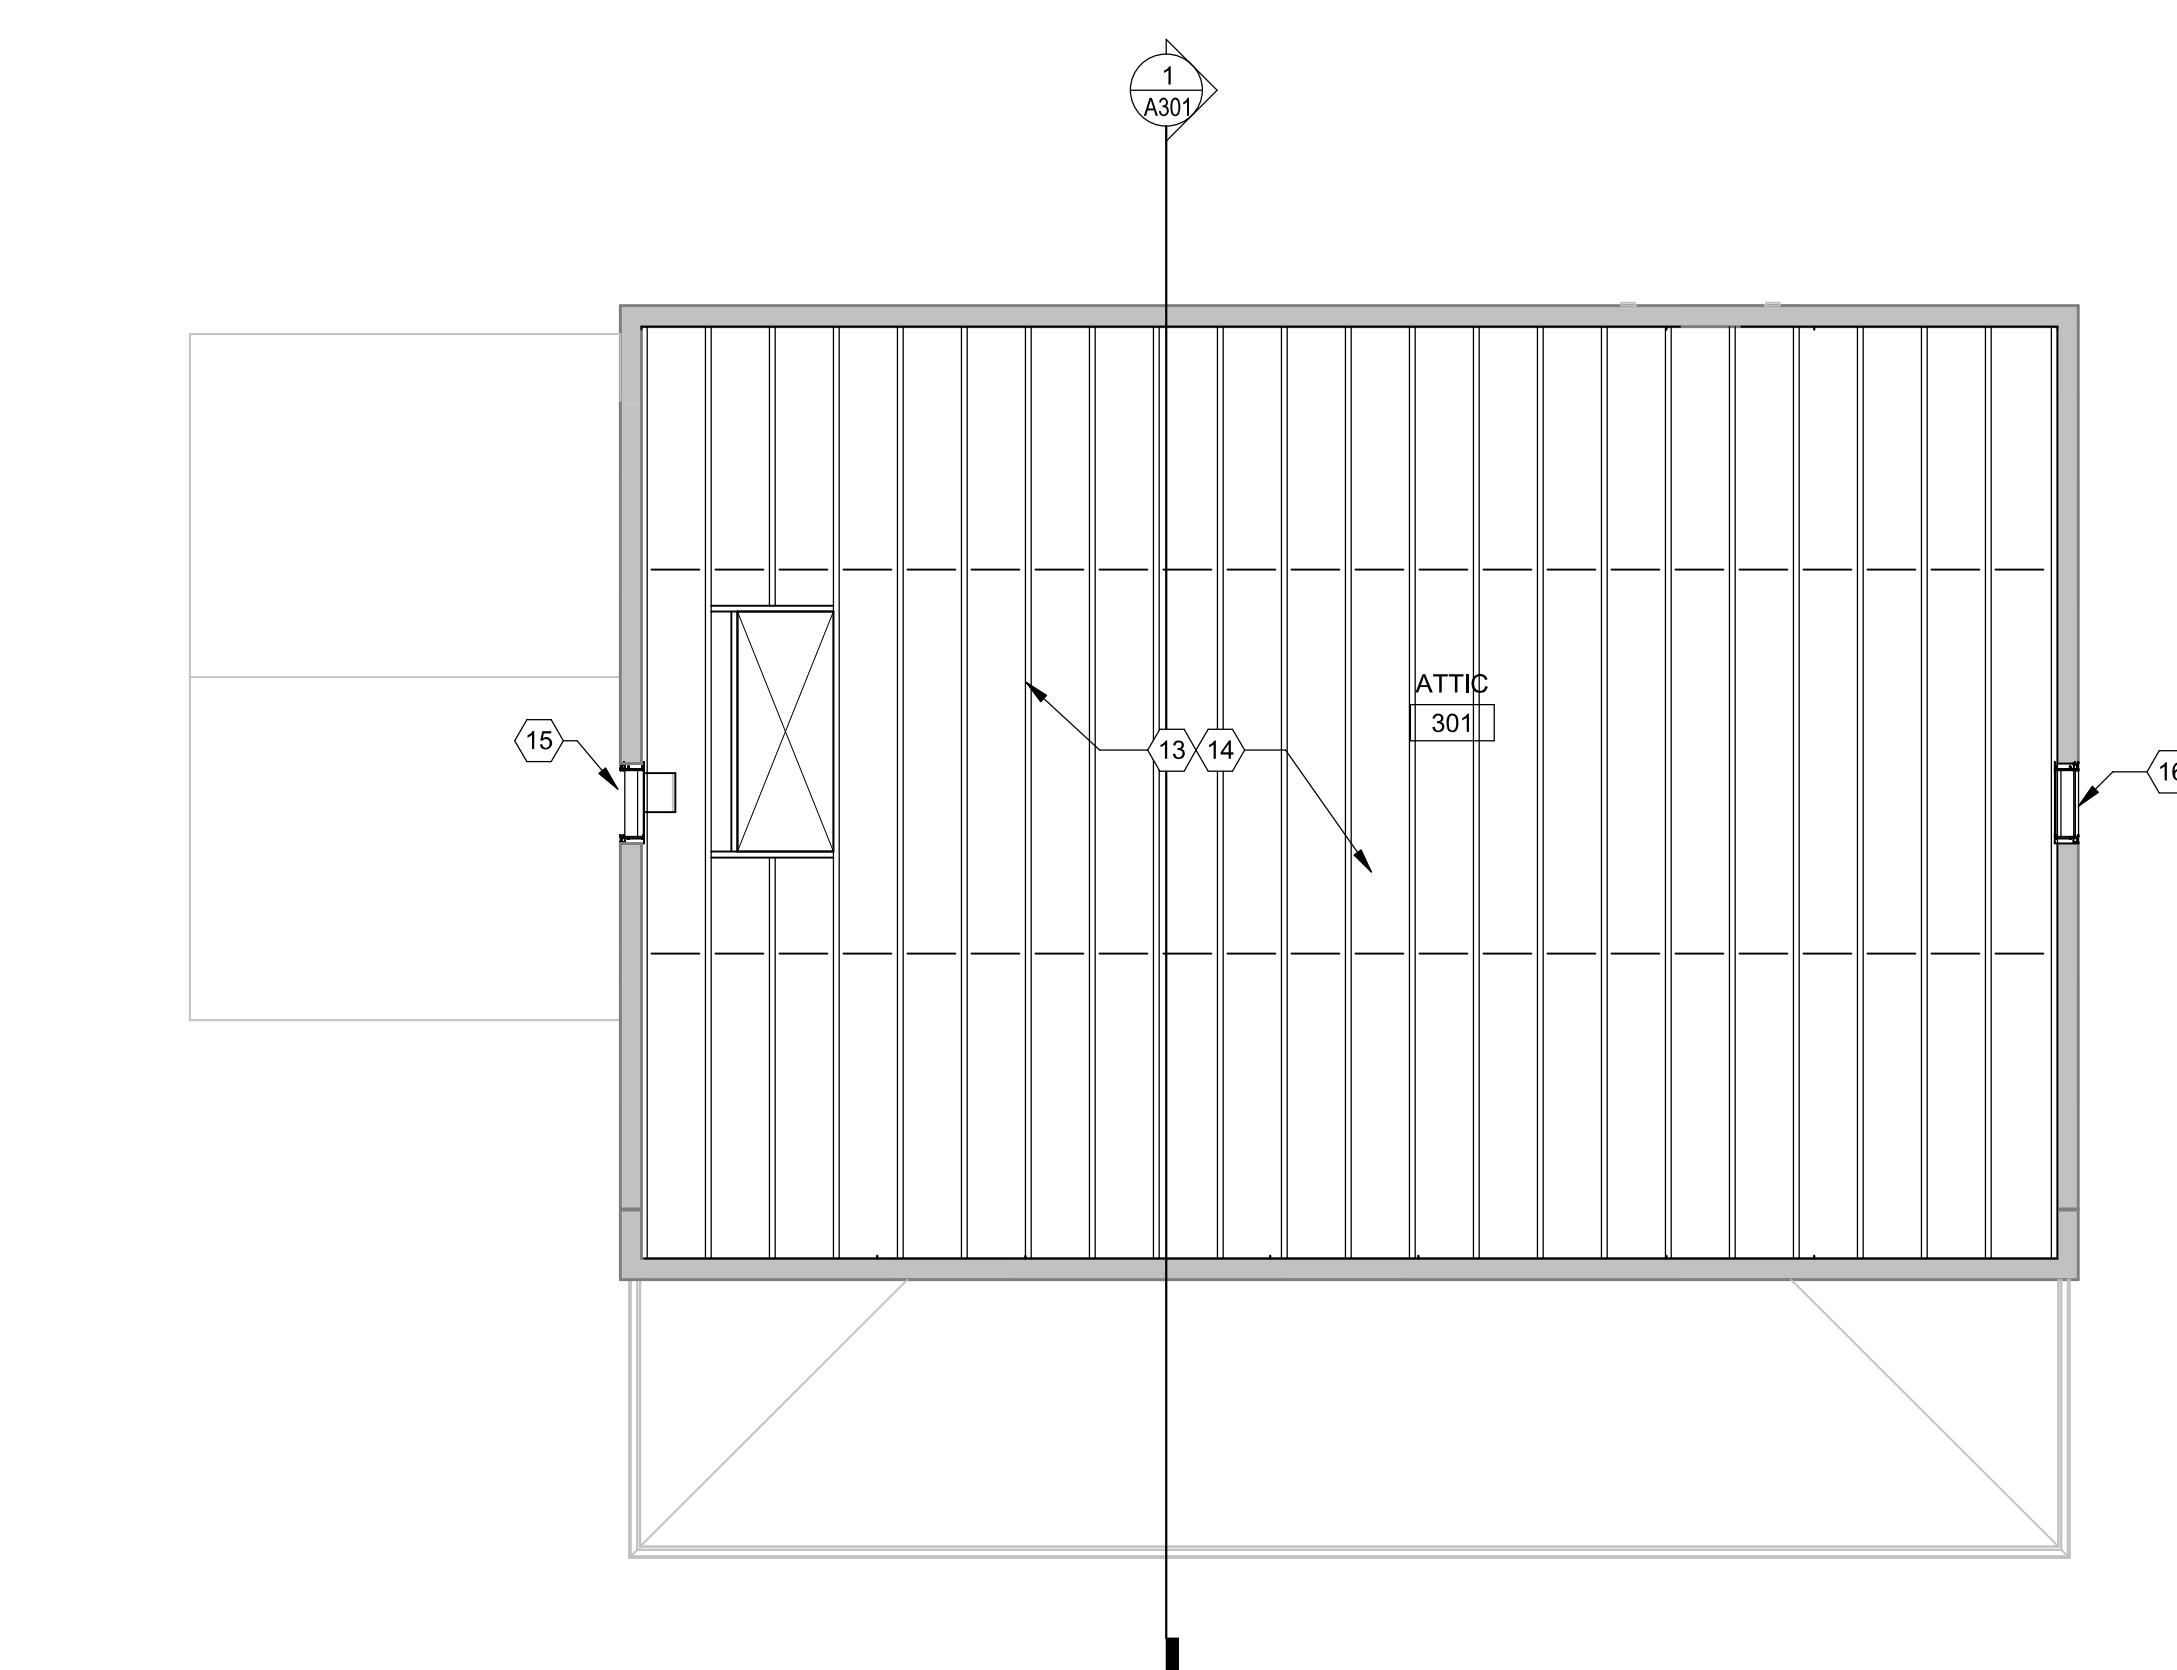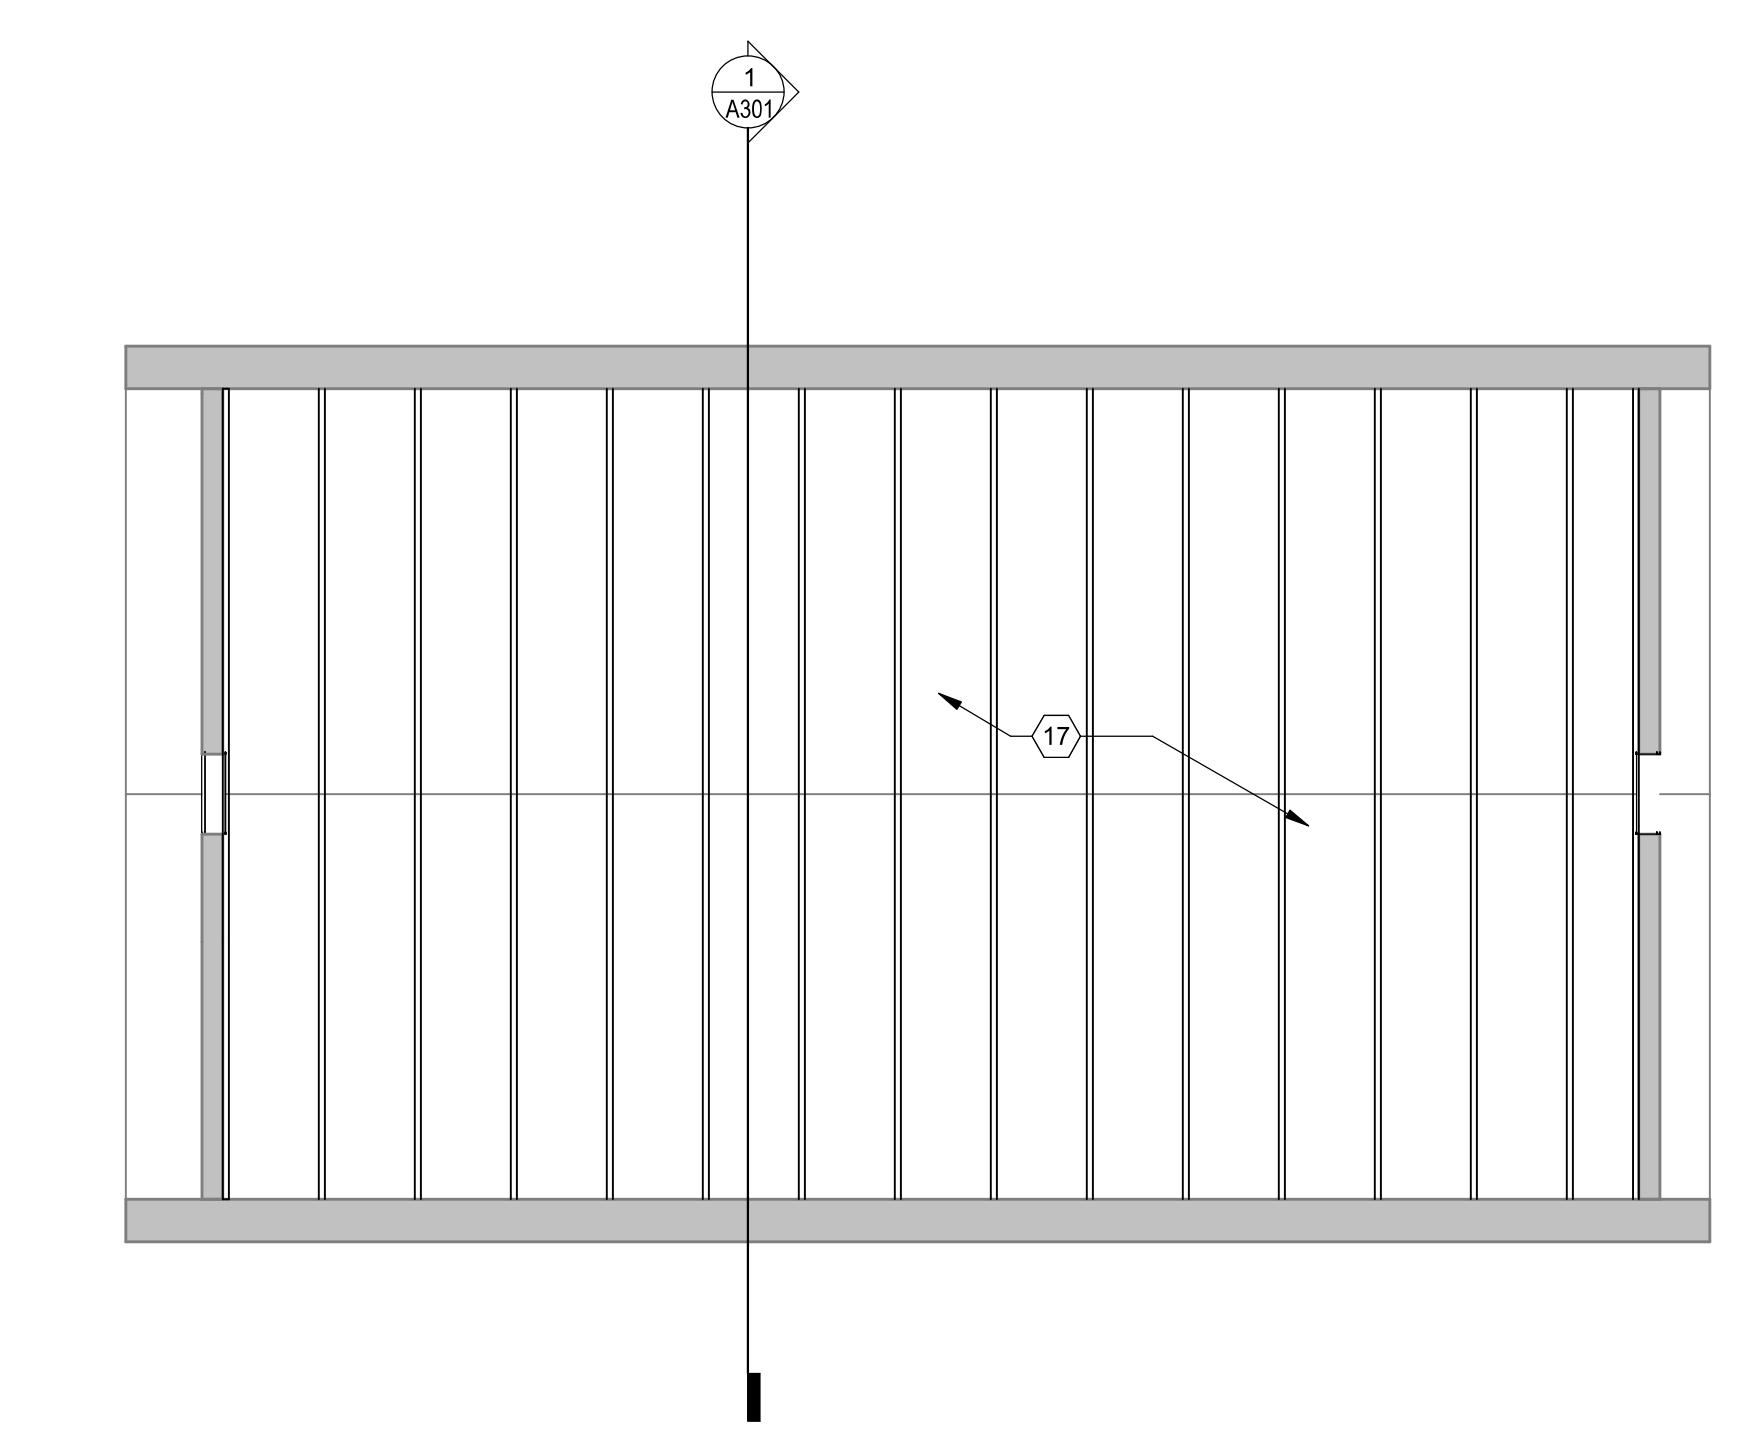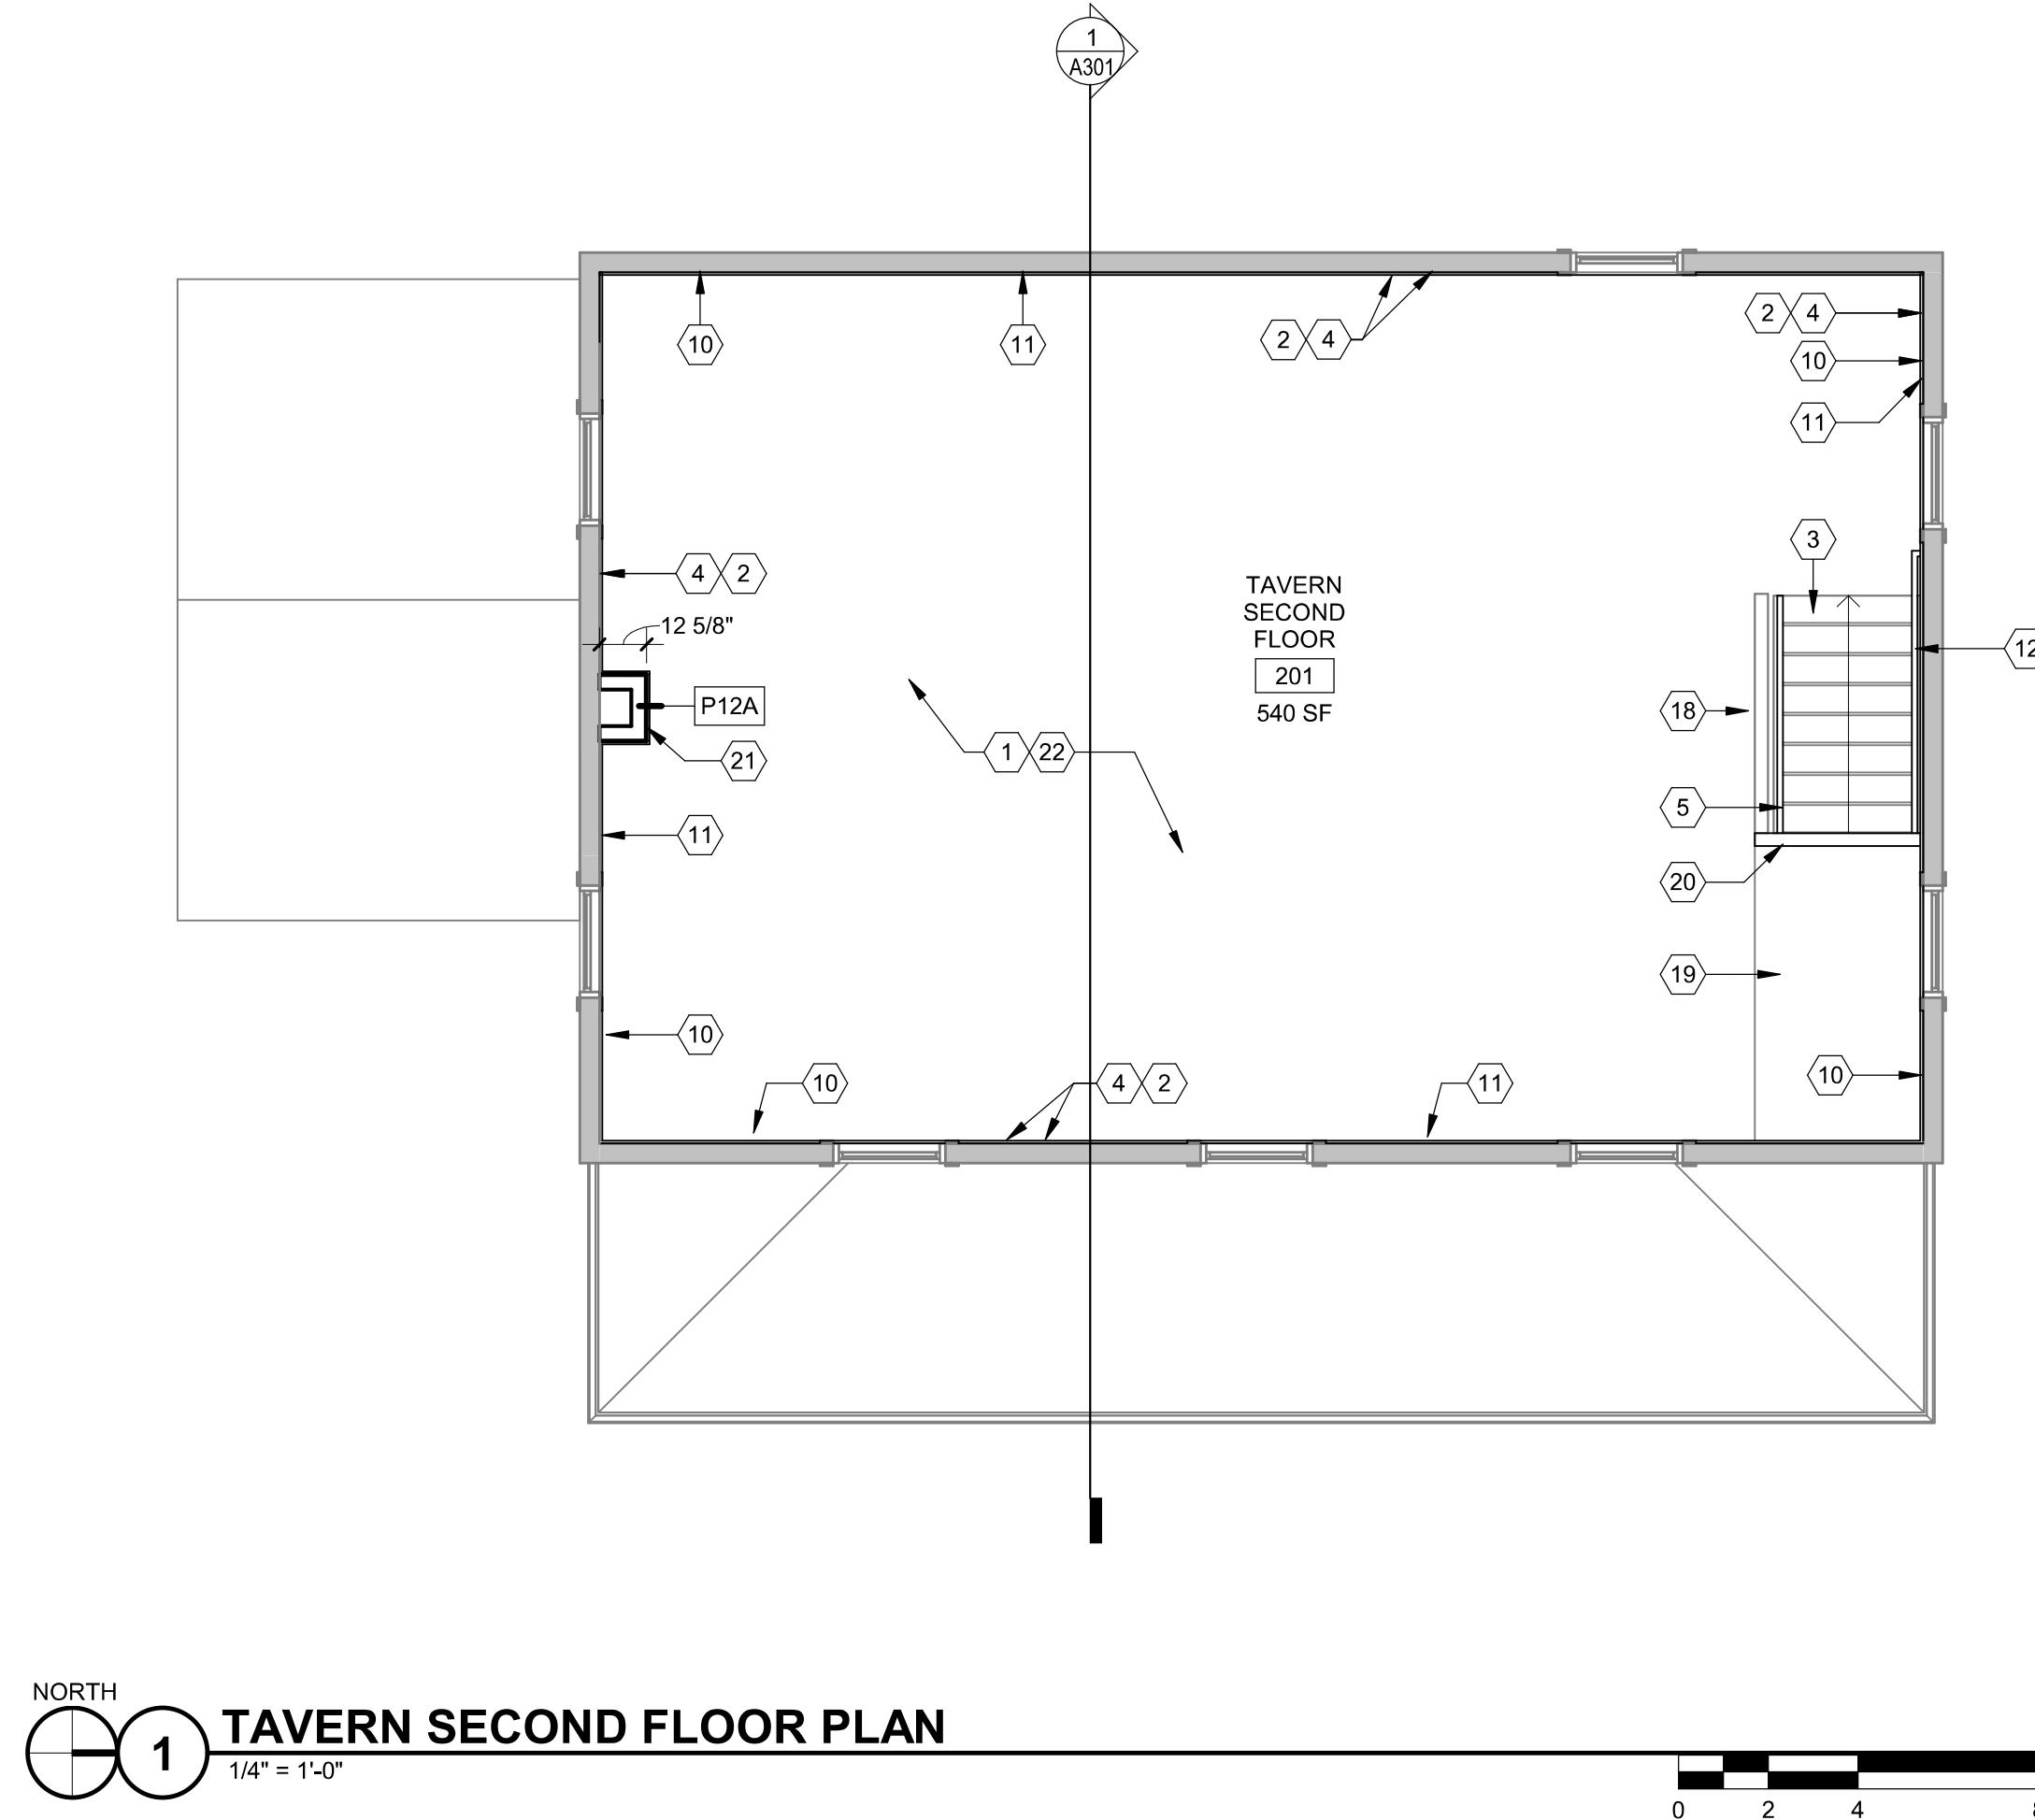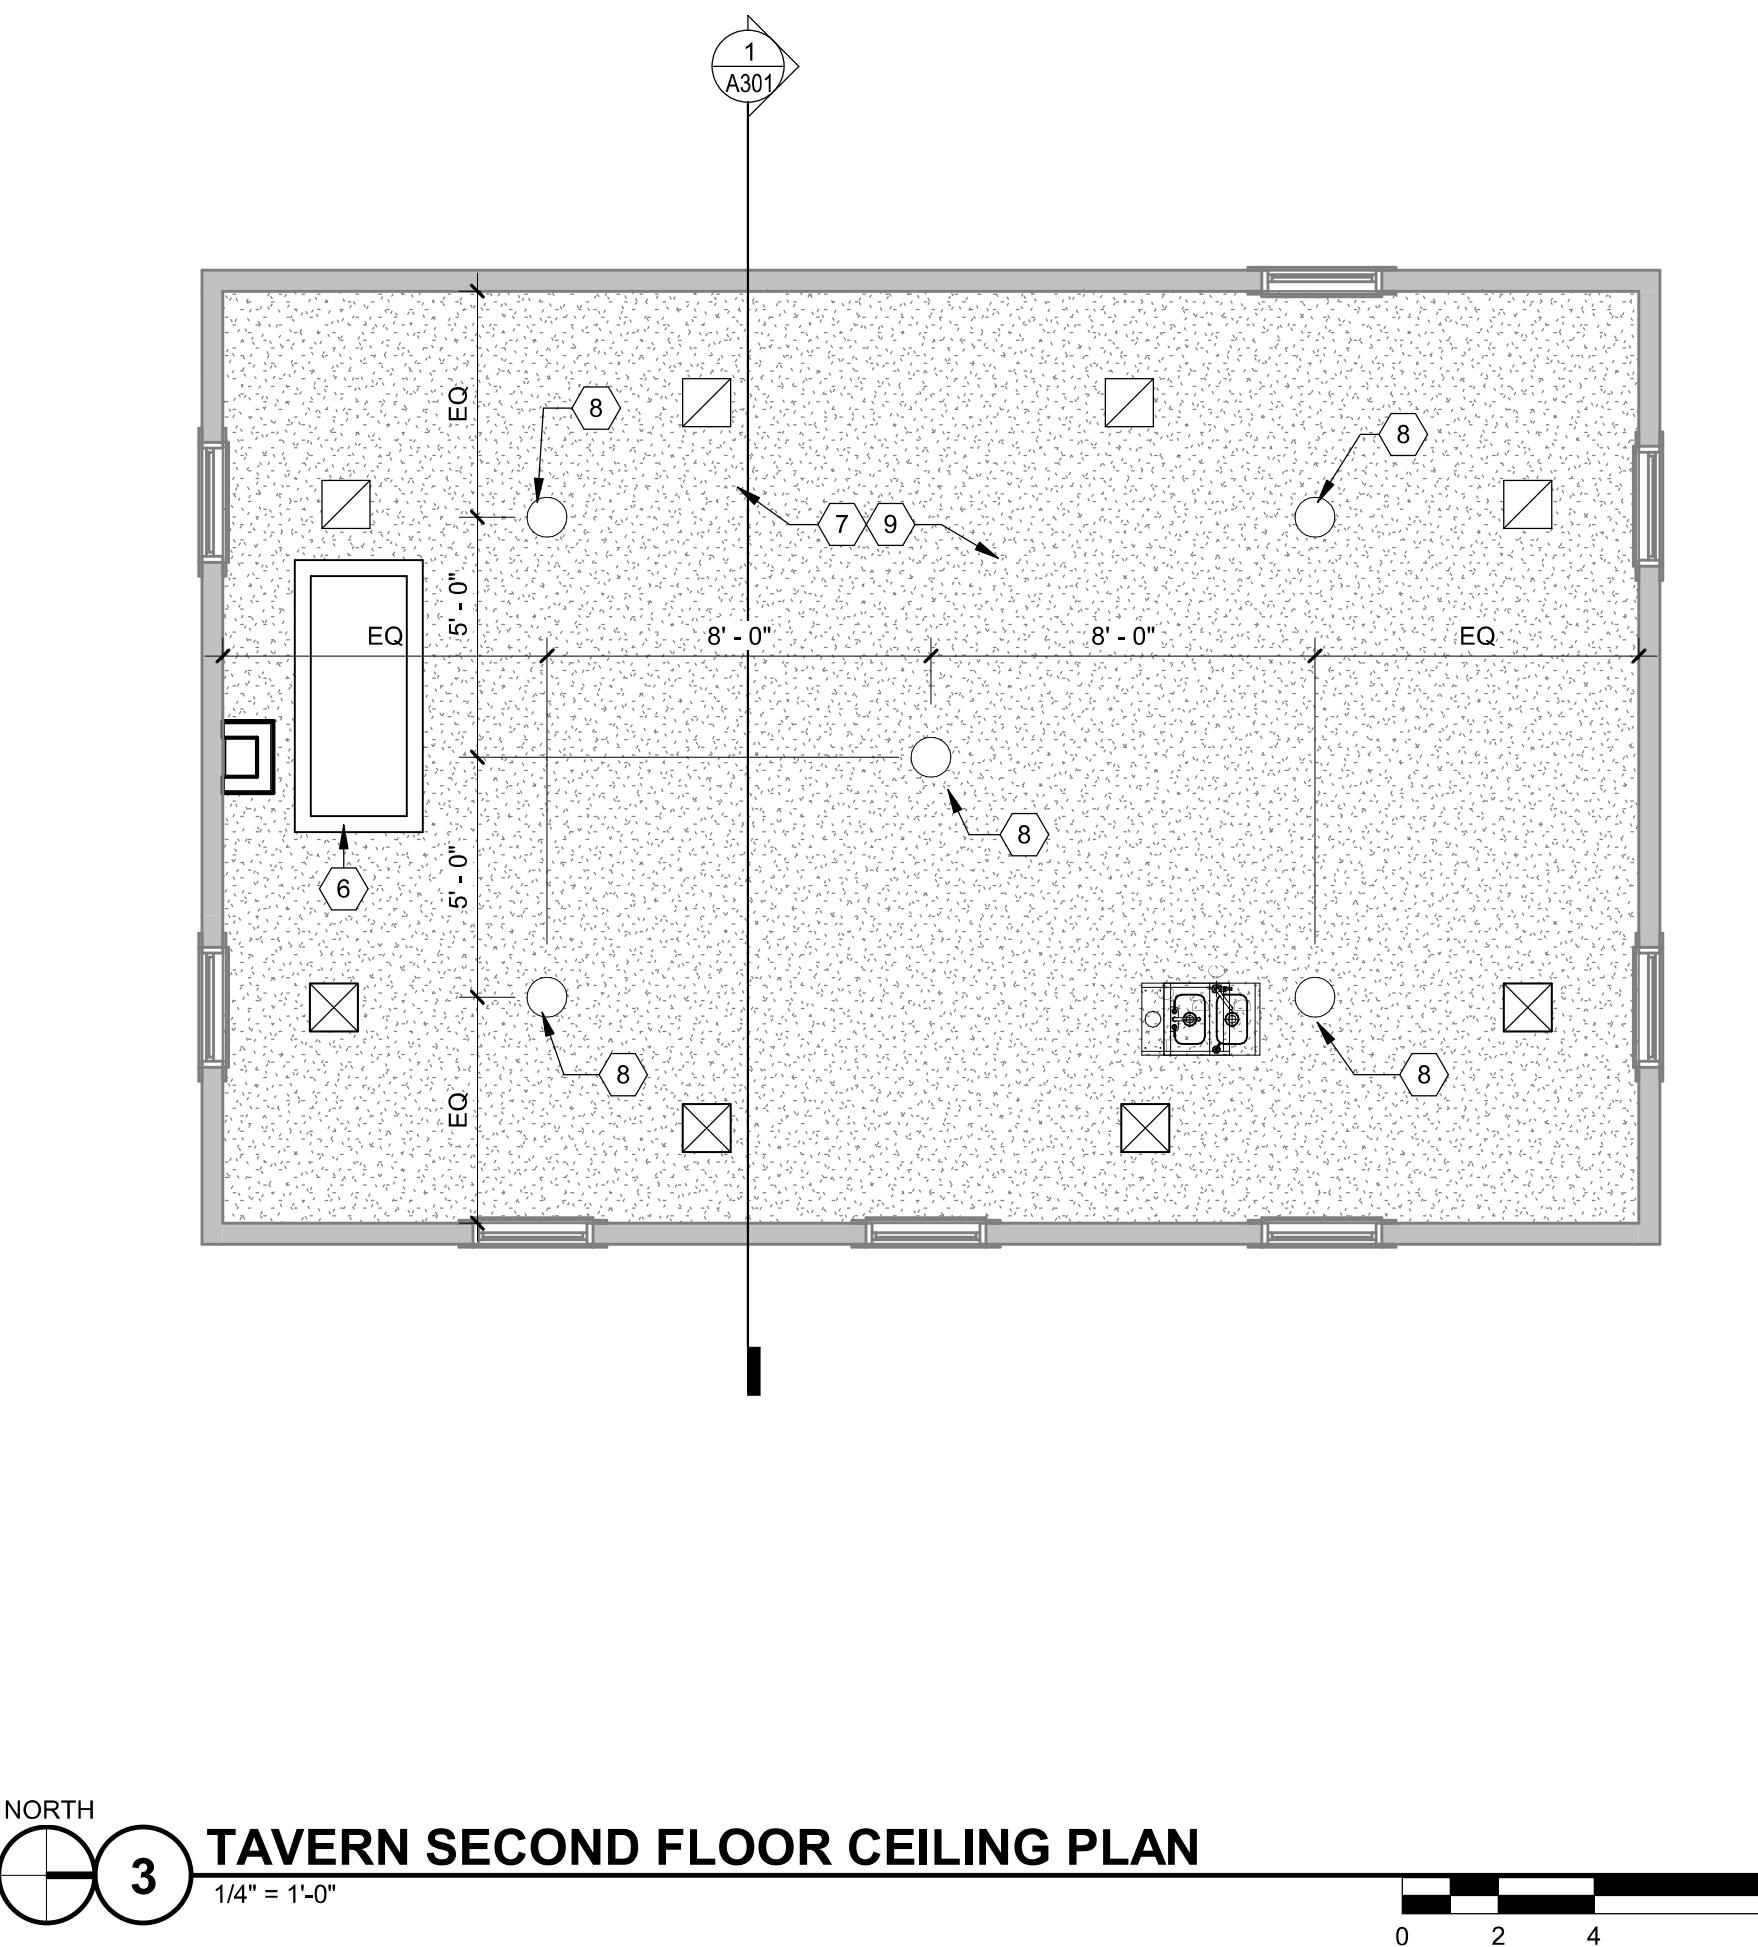

Consultant:

KEYED NOTES	
1	INSTALL 6" THK MINERAL WOOL BOARD INSULATION IN BETWEEN EXISTING 2X WOOD ROOF FRAMING MEMBERS @ 24" O.C. AND IN VERTICAL END WALLS OF ATTIC SPACE TO INSULATE THE ENTIRE ATTIC
2	INSTALL 4" THK MINERAL WOOL BOARD INSULATION IN BETWEEN EXISTING 2X6 FLOOR FRAMING OF ATTIC @ 16" O.C. PRIOR TO PLYWOOD FLOOR INSTALLATION
3	INSTALL 1/2" PLYWOOD SHEATHING ON TOP OF 2X6 WOOD FLOOR FRAMING
4	4" CONCRETE SLAB ON GRADE OVER VAPOR BARRIER AND EXISTING FREE DRAINING FILL
5	PAINTED ALUMINUM 20"WX28"H MECHANICAL LOUVER IN EXISTING WINDOW ROUGH OPENING, SEE DETAIL 2/A511 SIMILAR

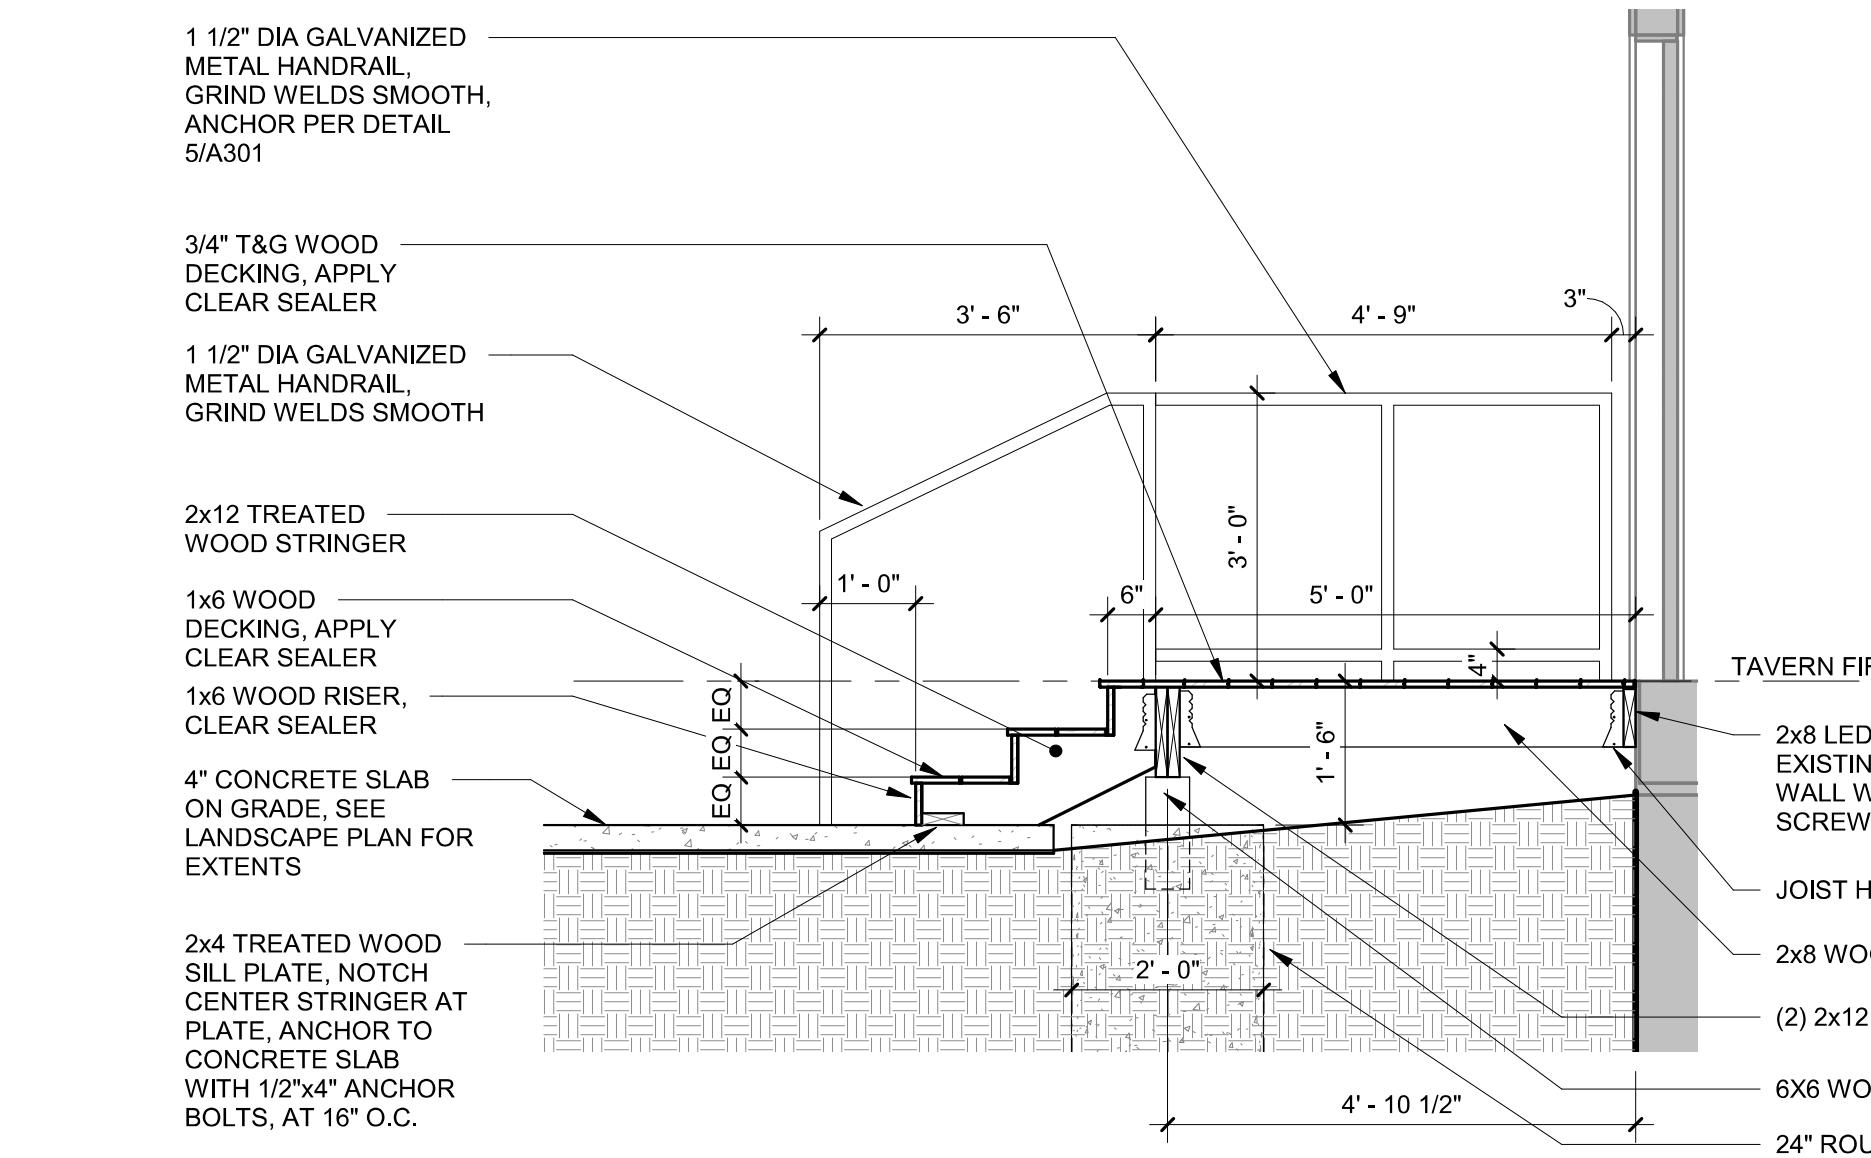

4 STAIR SECTION


1/2" = 1'-0"

0 1 2 4

5 HANDRAIL BASEPLATE

3" = 1'-0"

0 0.25 0.5 0.75

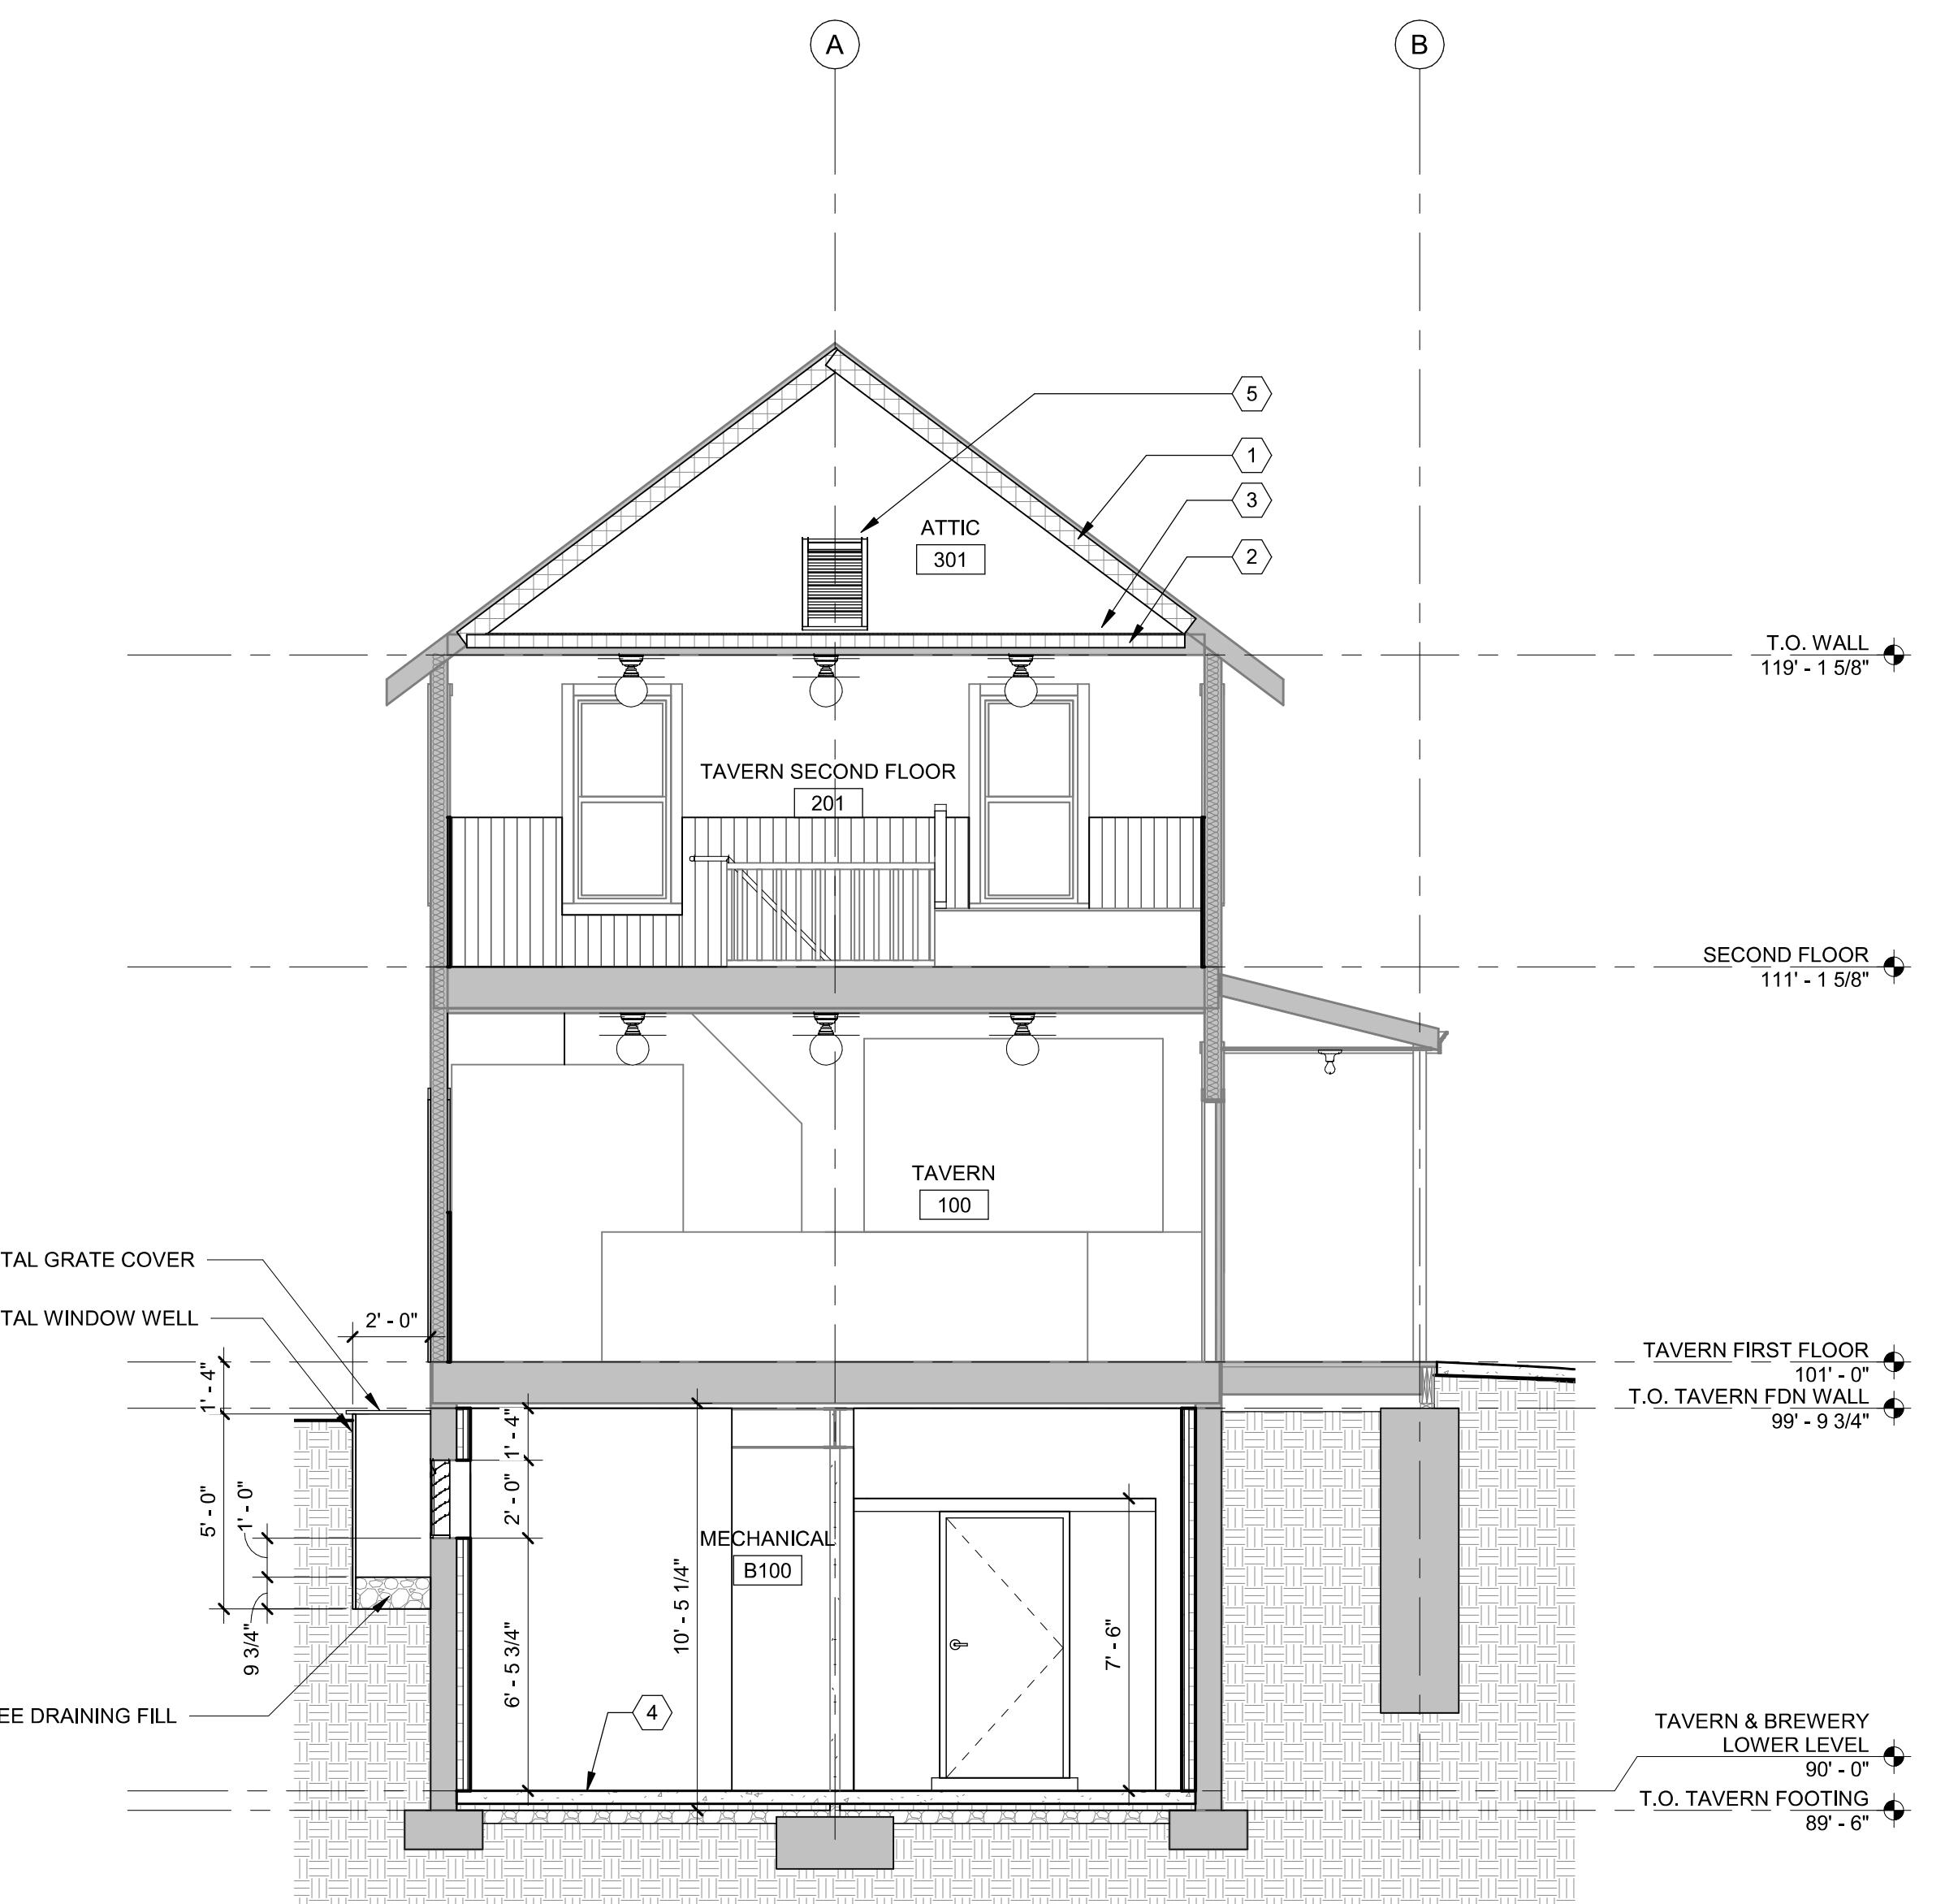

1 TAVERN BUILDING SECTION

1/4" = 1'-0"

0 2 4 8

3 ENLARGED STAIR PLAN

1/2" = 1'-0"


0 1 2 4



2 STAIR FRAMING PLAN

1/2" = 1'-0"

0 1 2 4

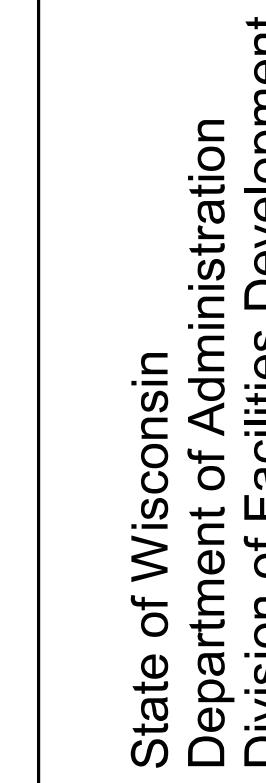

Town of Eagle, Wisconsin

Tavern Renovations
Old World Wisconsin Ethnic Outdoor Museum
Wisconsin Historical Society
Town of Eagle, Wisconsin

Sheet Title: TAVERN SECTION AND STAIR PLAN

Revisions:


No.

Date:

Description:


Graphic Scale	See Details
DFD Number	17I1K-04
Set Type	BD
Date Issued	9/8/2023
Sheet Number	A301

Consultant:

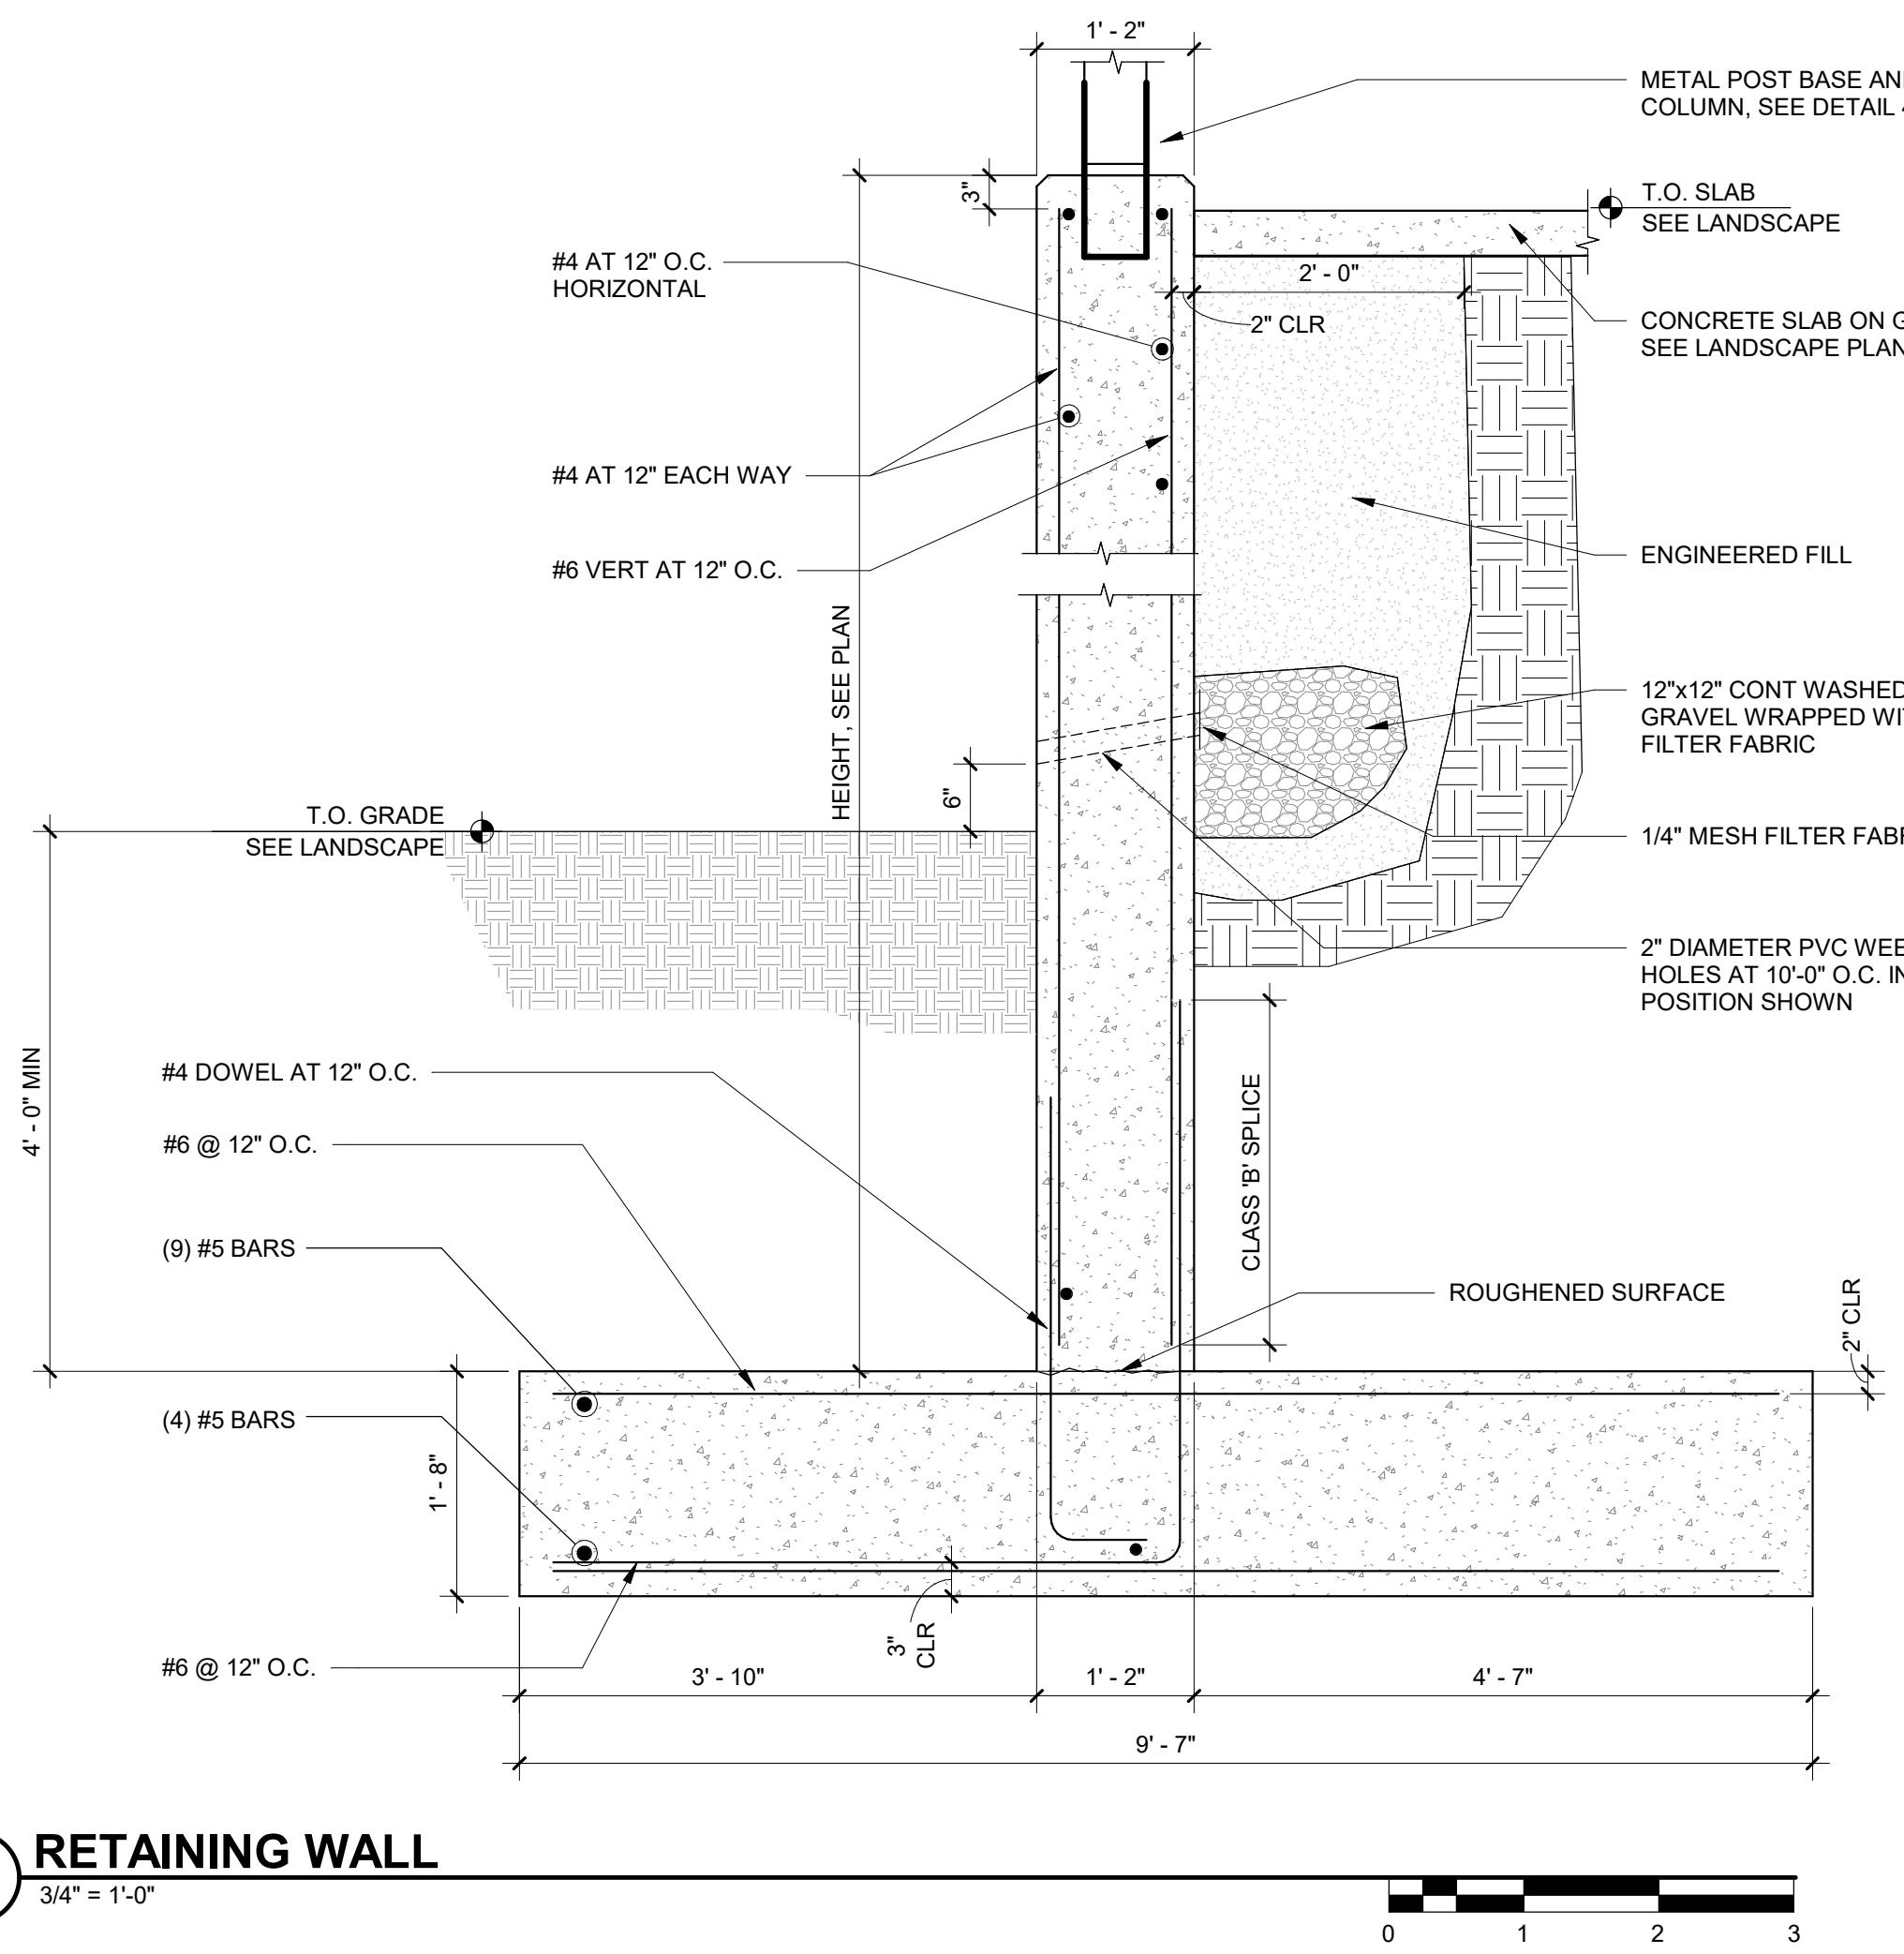


5 RETAINING WALL

3/4" = 1'-0"

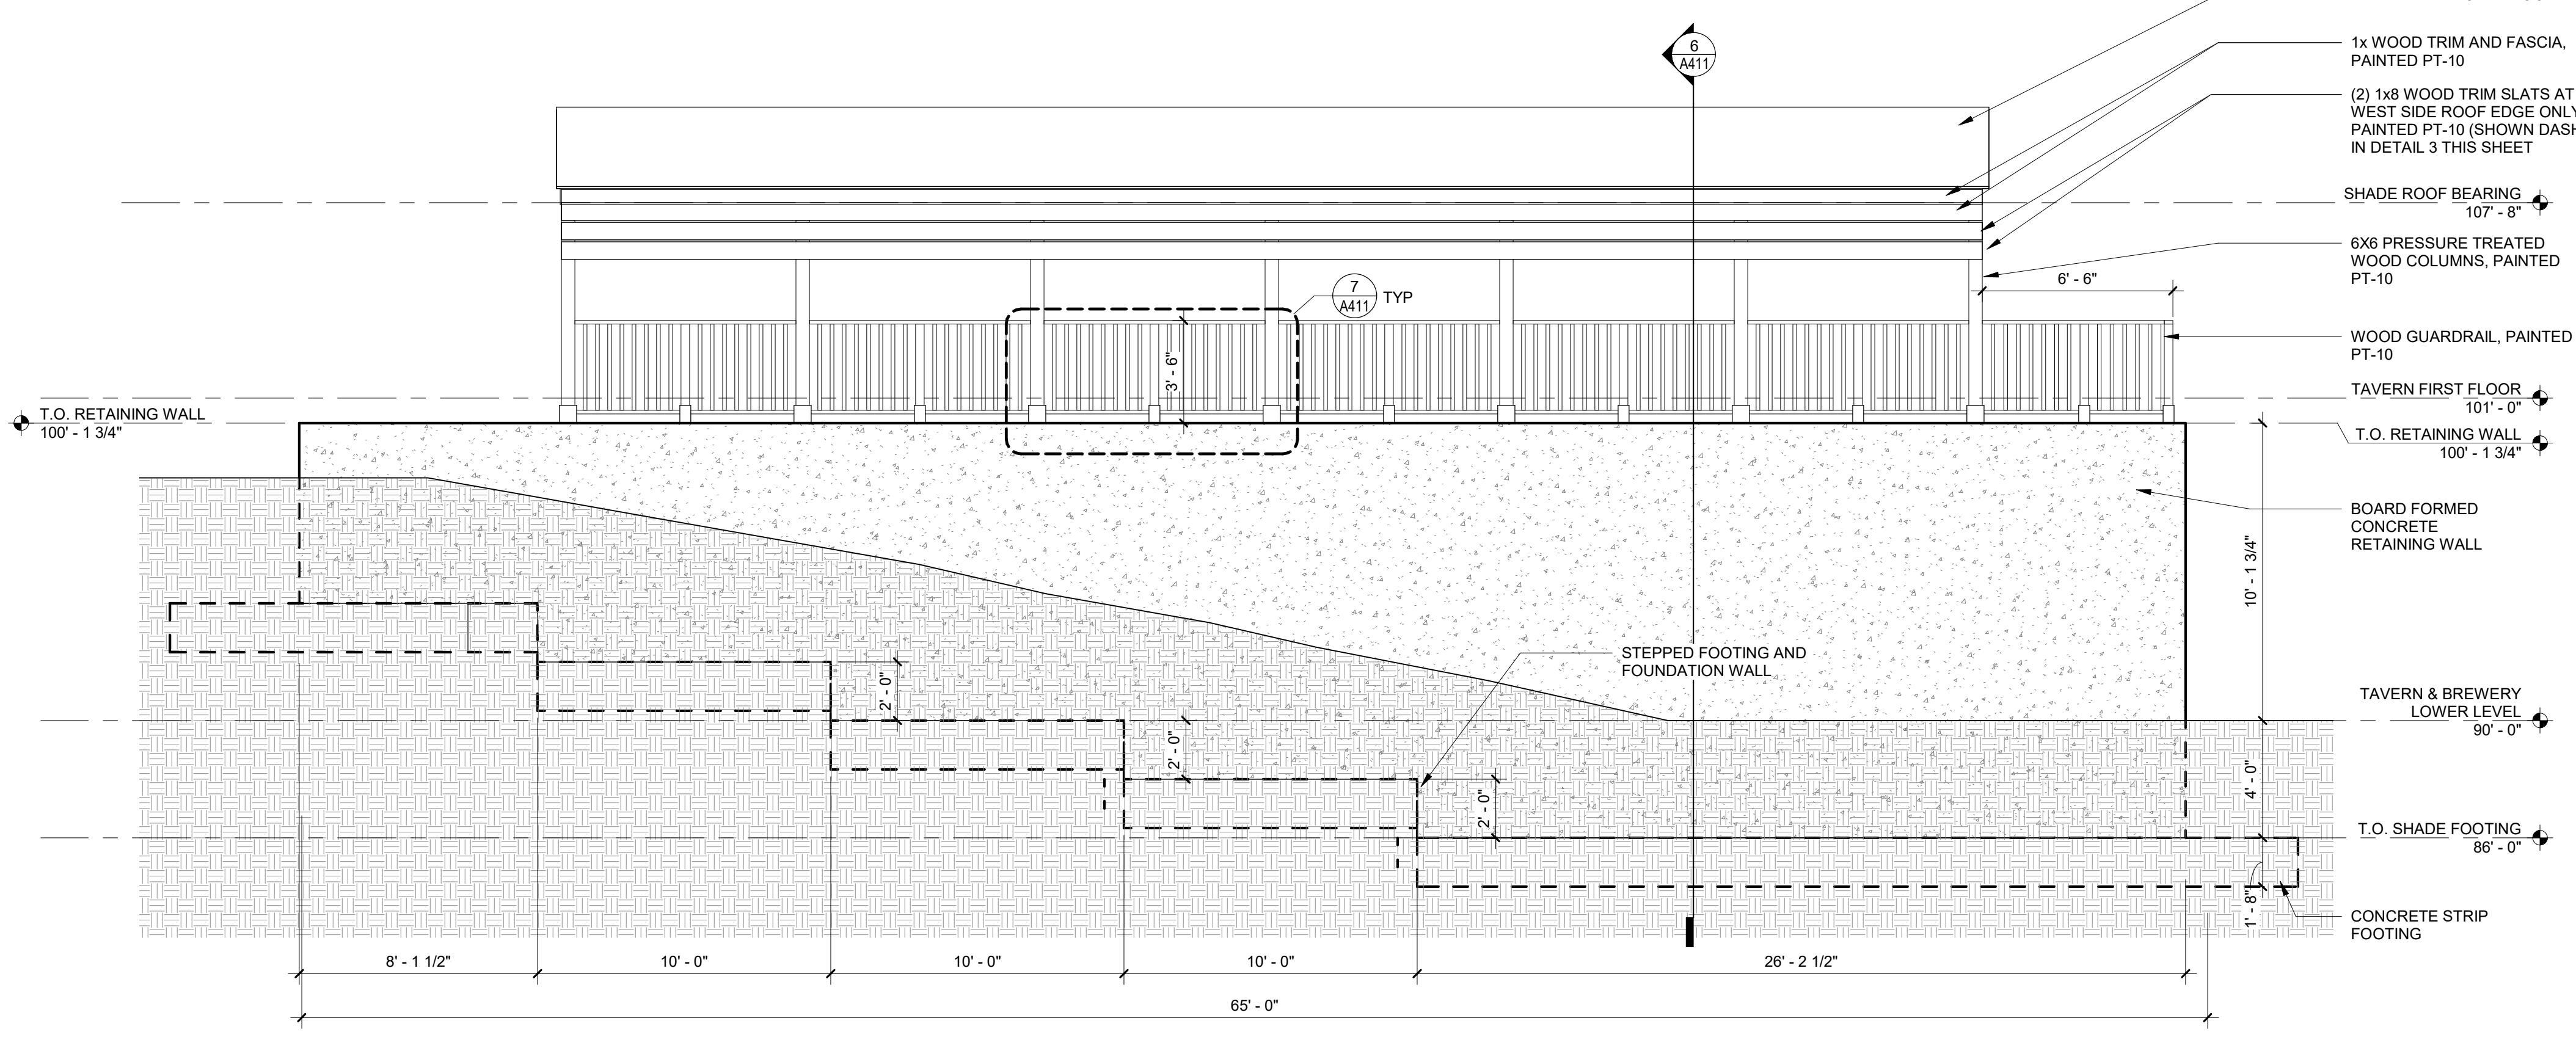


1 WEST SUN SHADE ELEVATION

1/4" = 1'-0"

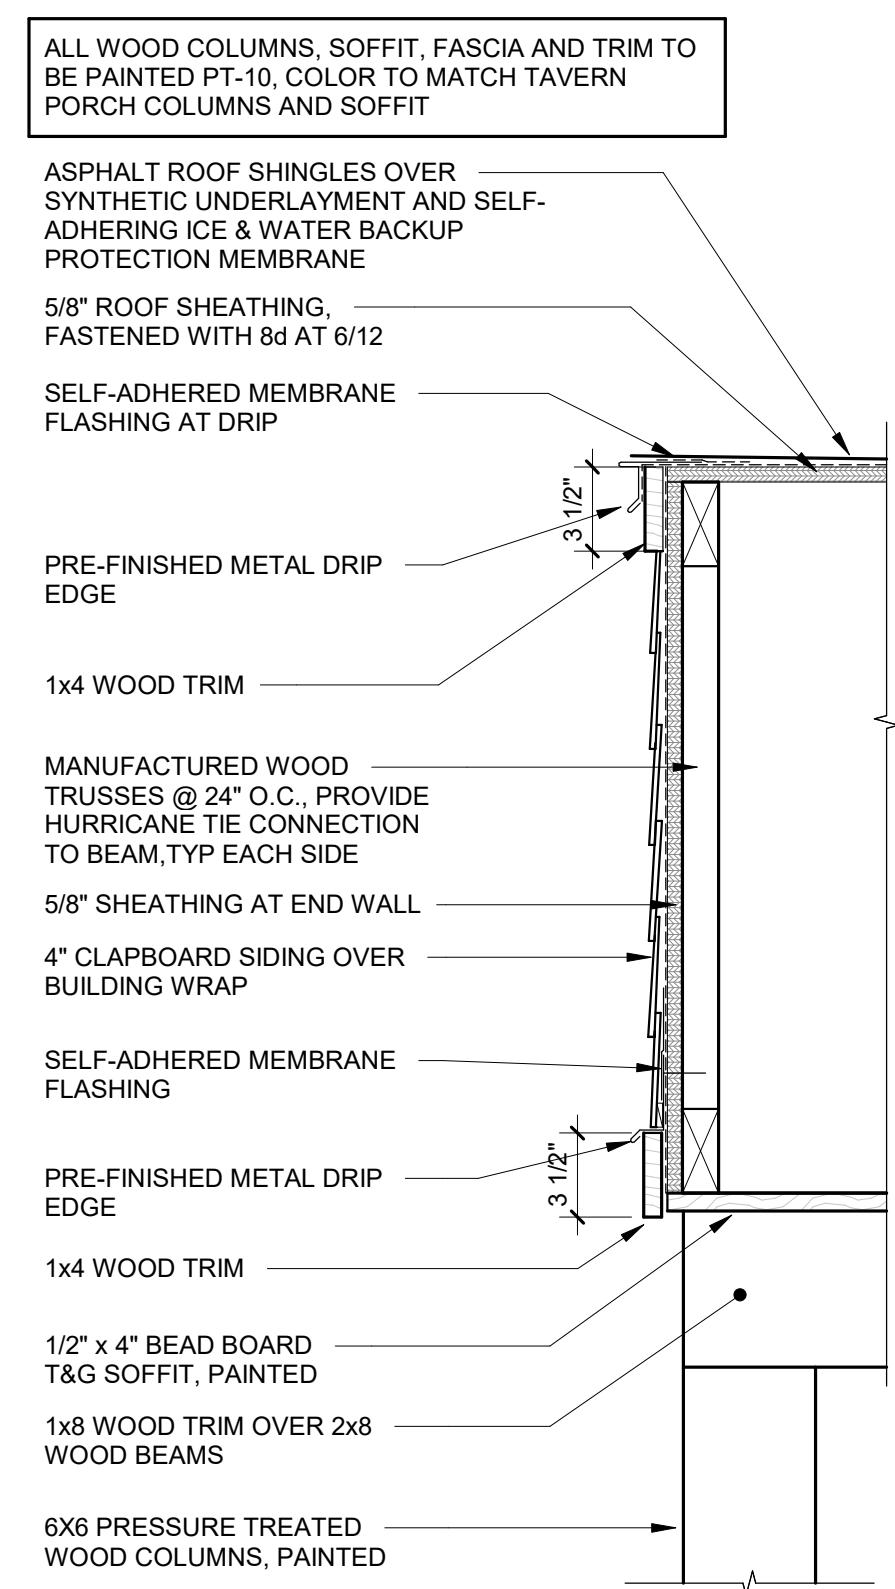


8 SUN SHADE END WALL DETAIL

1 1/2" = 1'-0"

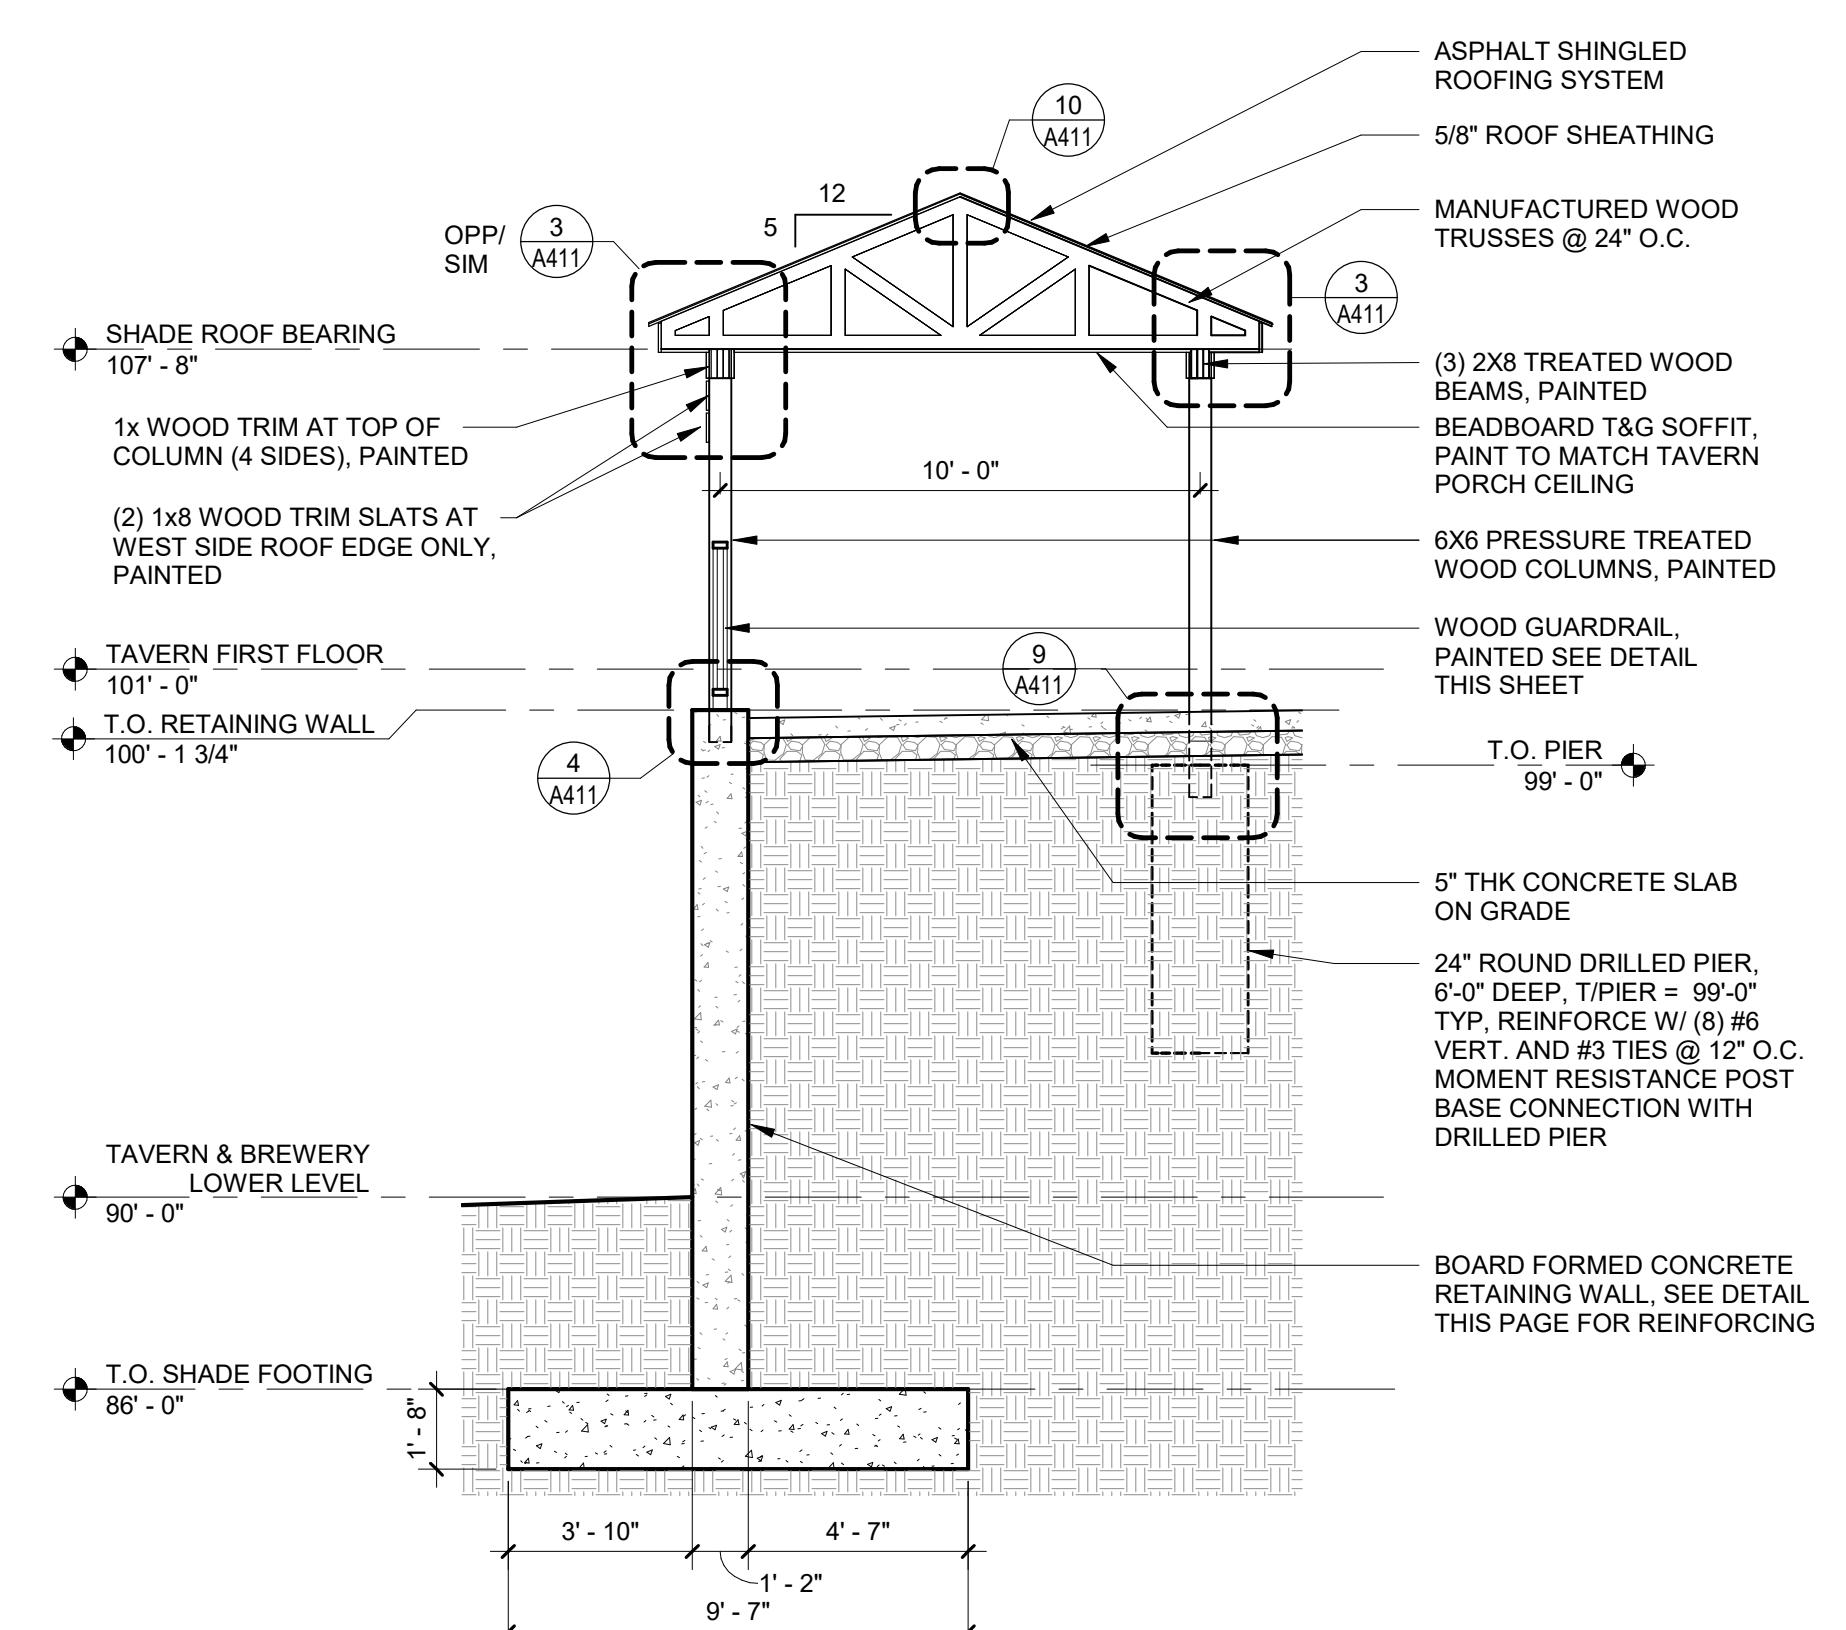


6 SUN SHADE SECTION

1/4" = 1'-0"

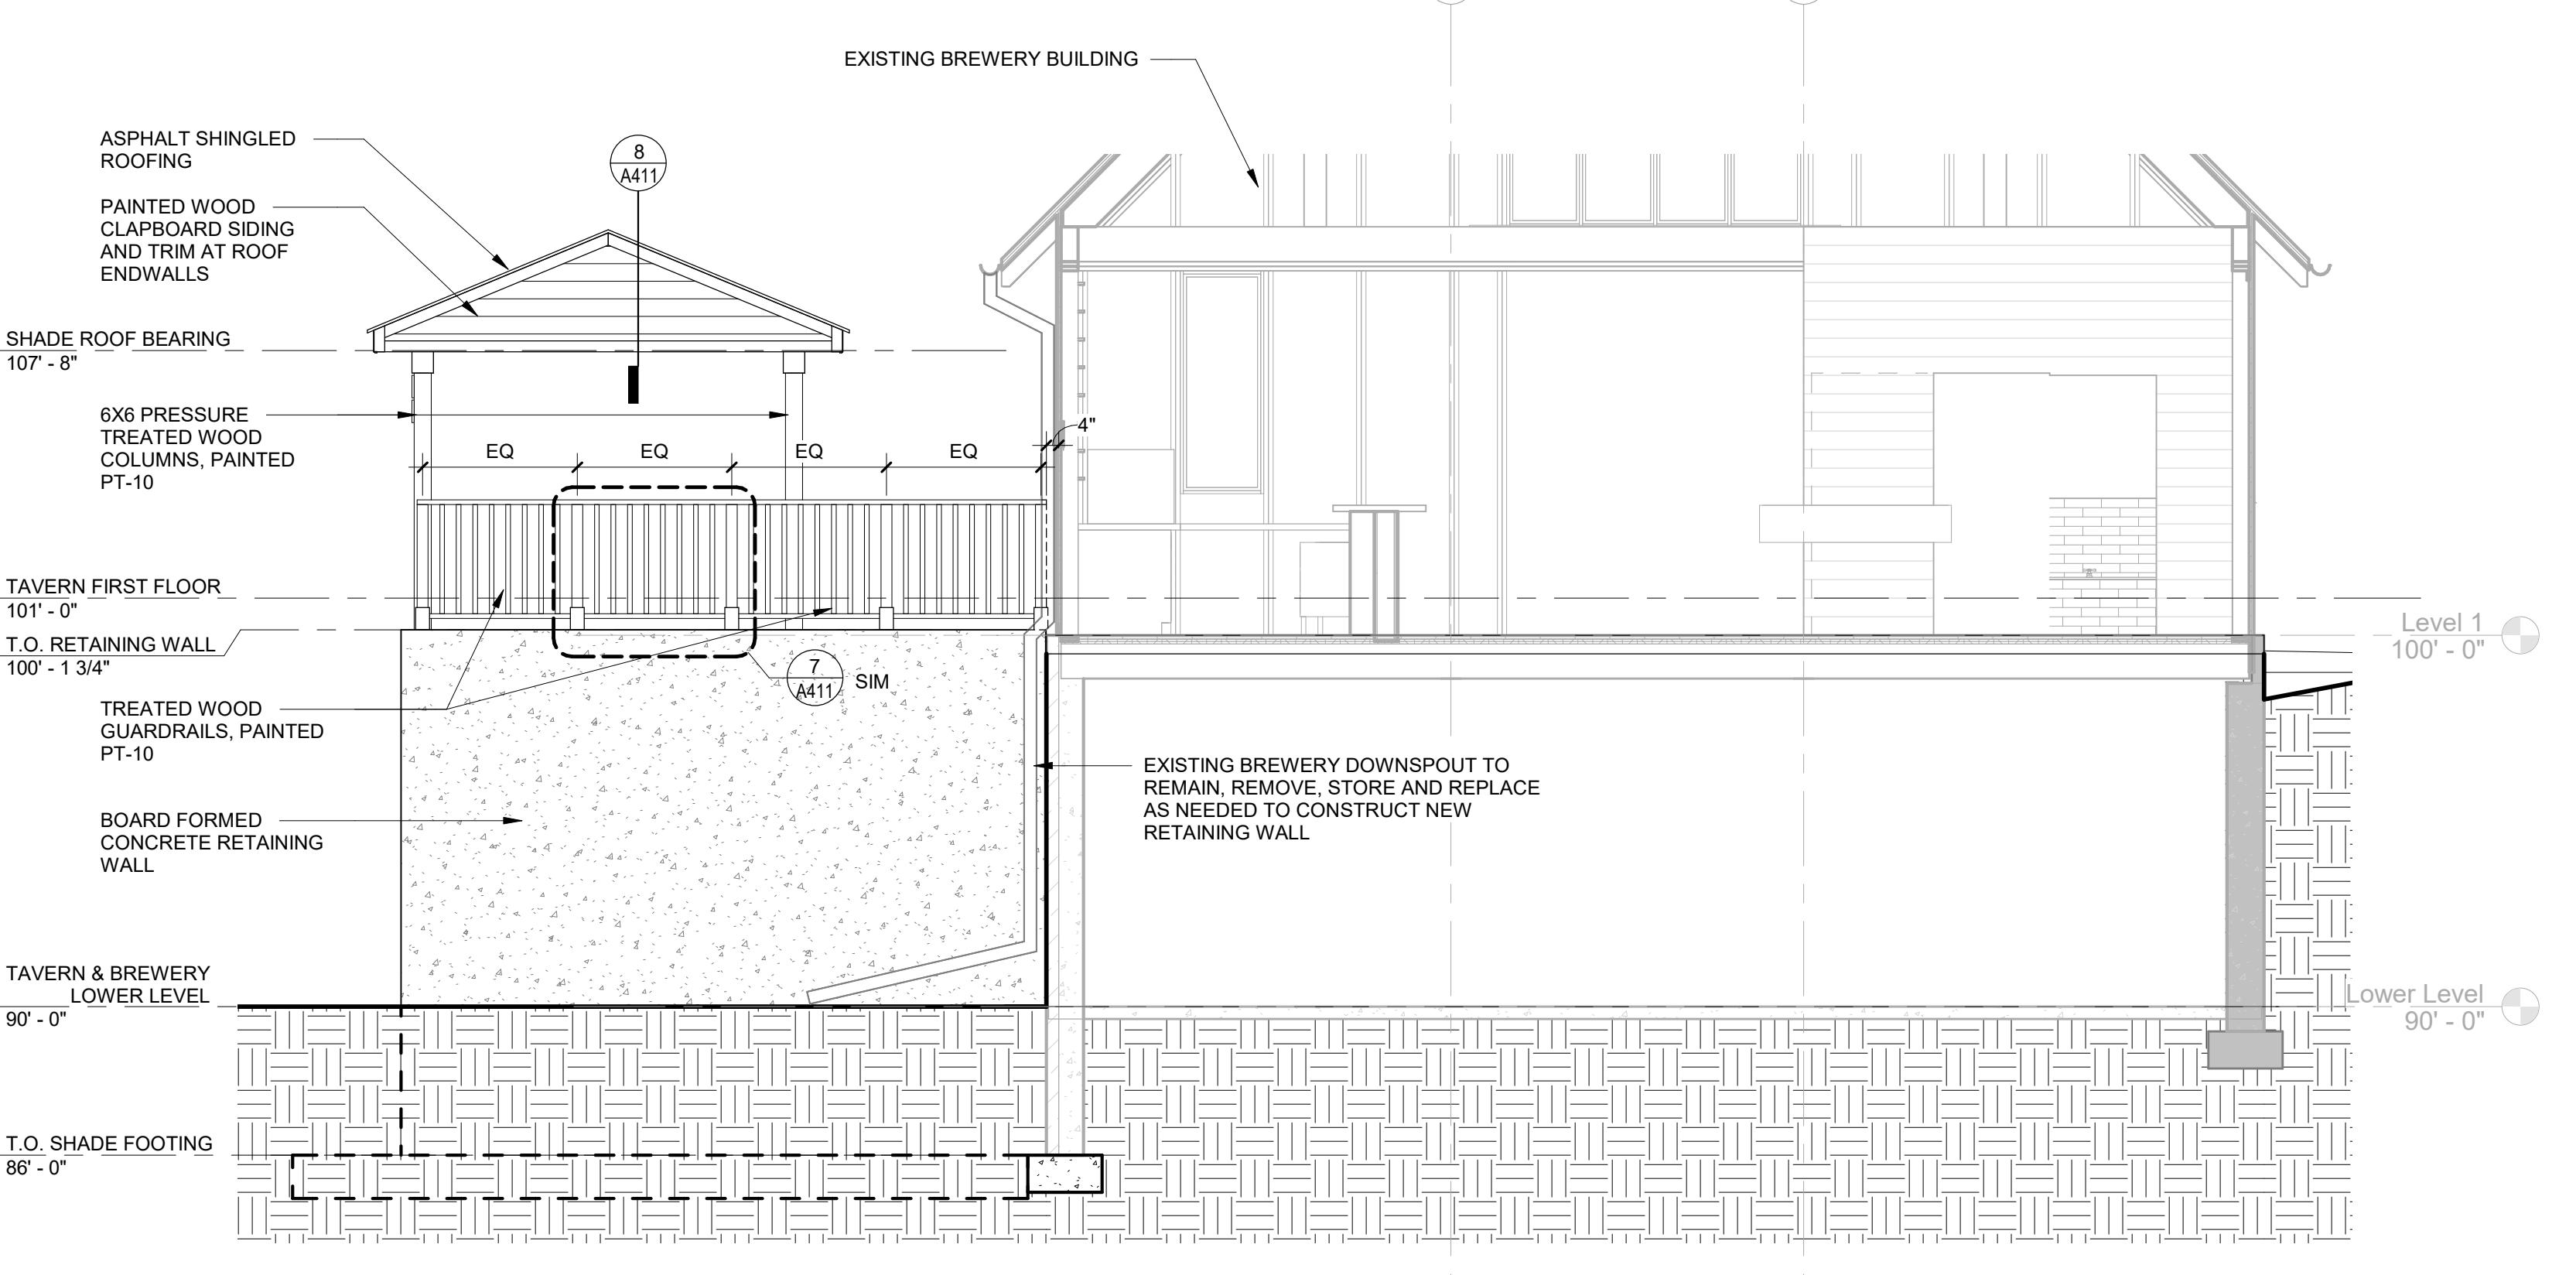


2 SOUTH SUN SHADE ELEVATION

1/4" = 1'-0"

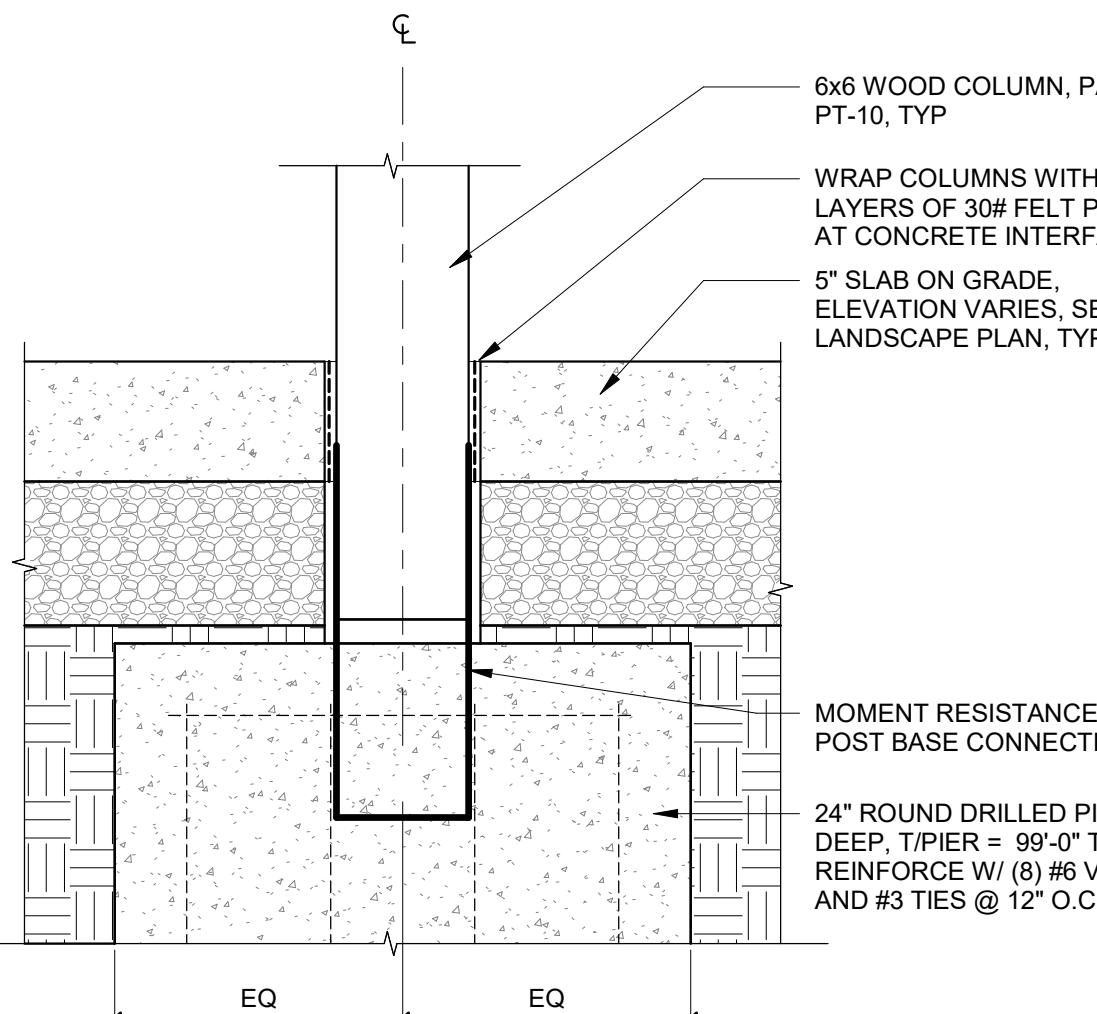


9 WOOD COLUMN AT DRILLED PIERS

1 1/2" = 1'-0"

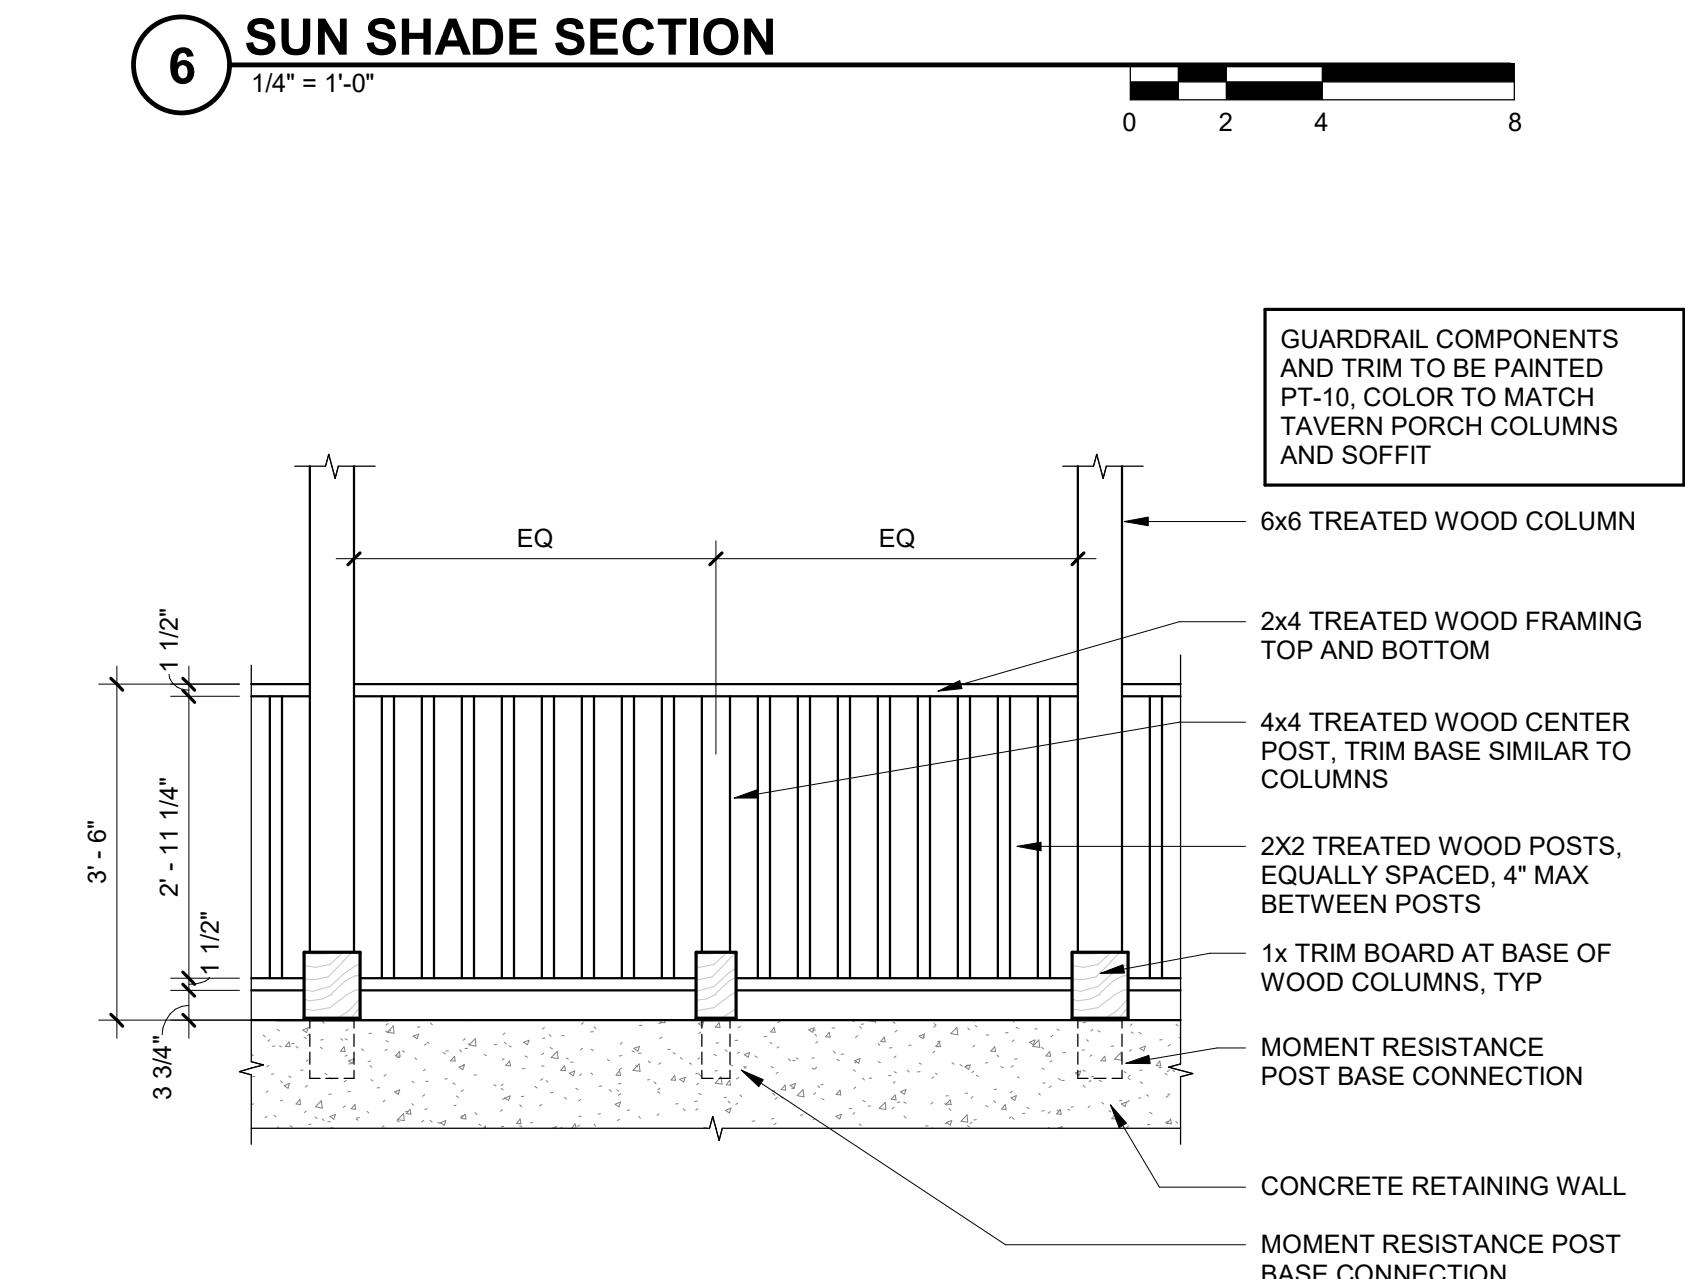


7 WOOD GUARDRAIL AT RETAINING WALL

1/2" = 1'-0"

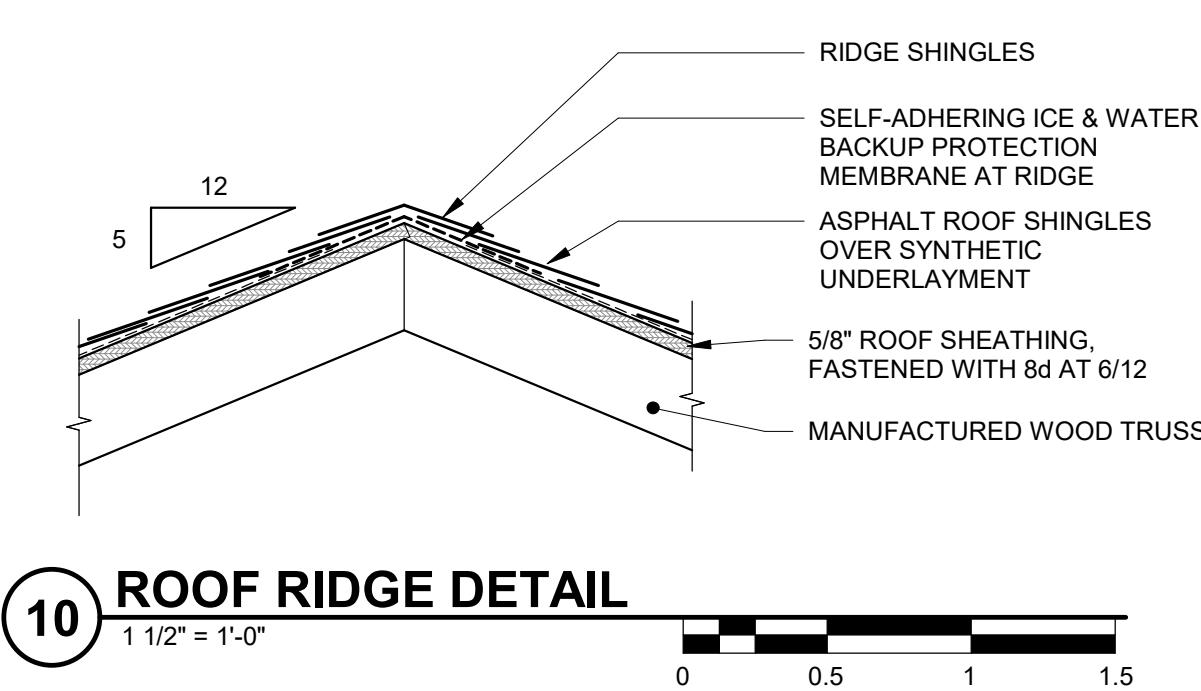


10 ROOF RIDGE DETAIL

1 1/2" = 1'-0"

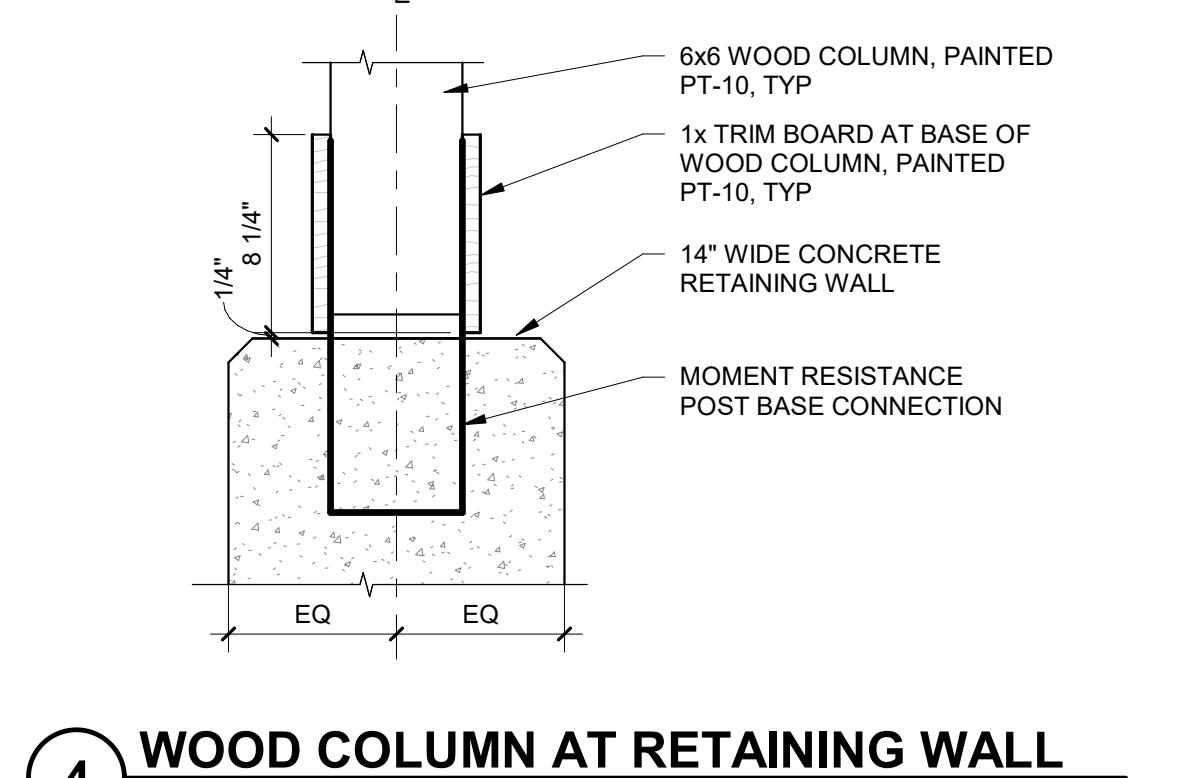

4 WOOD COLUMN AT RETAINING WALL


1 1/2" = 1'-0"

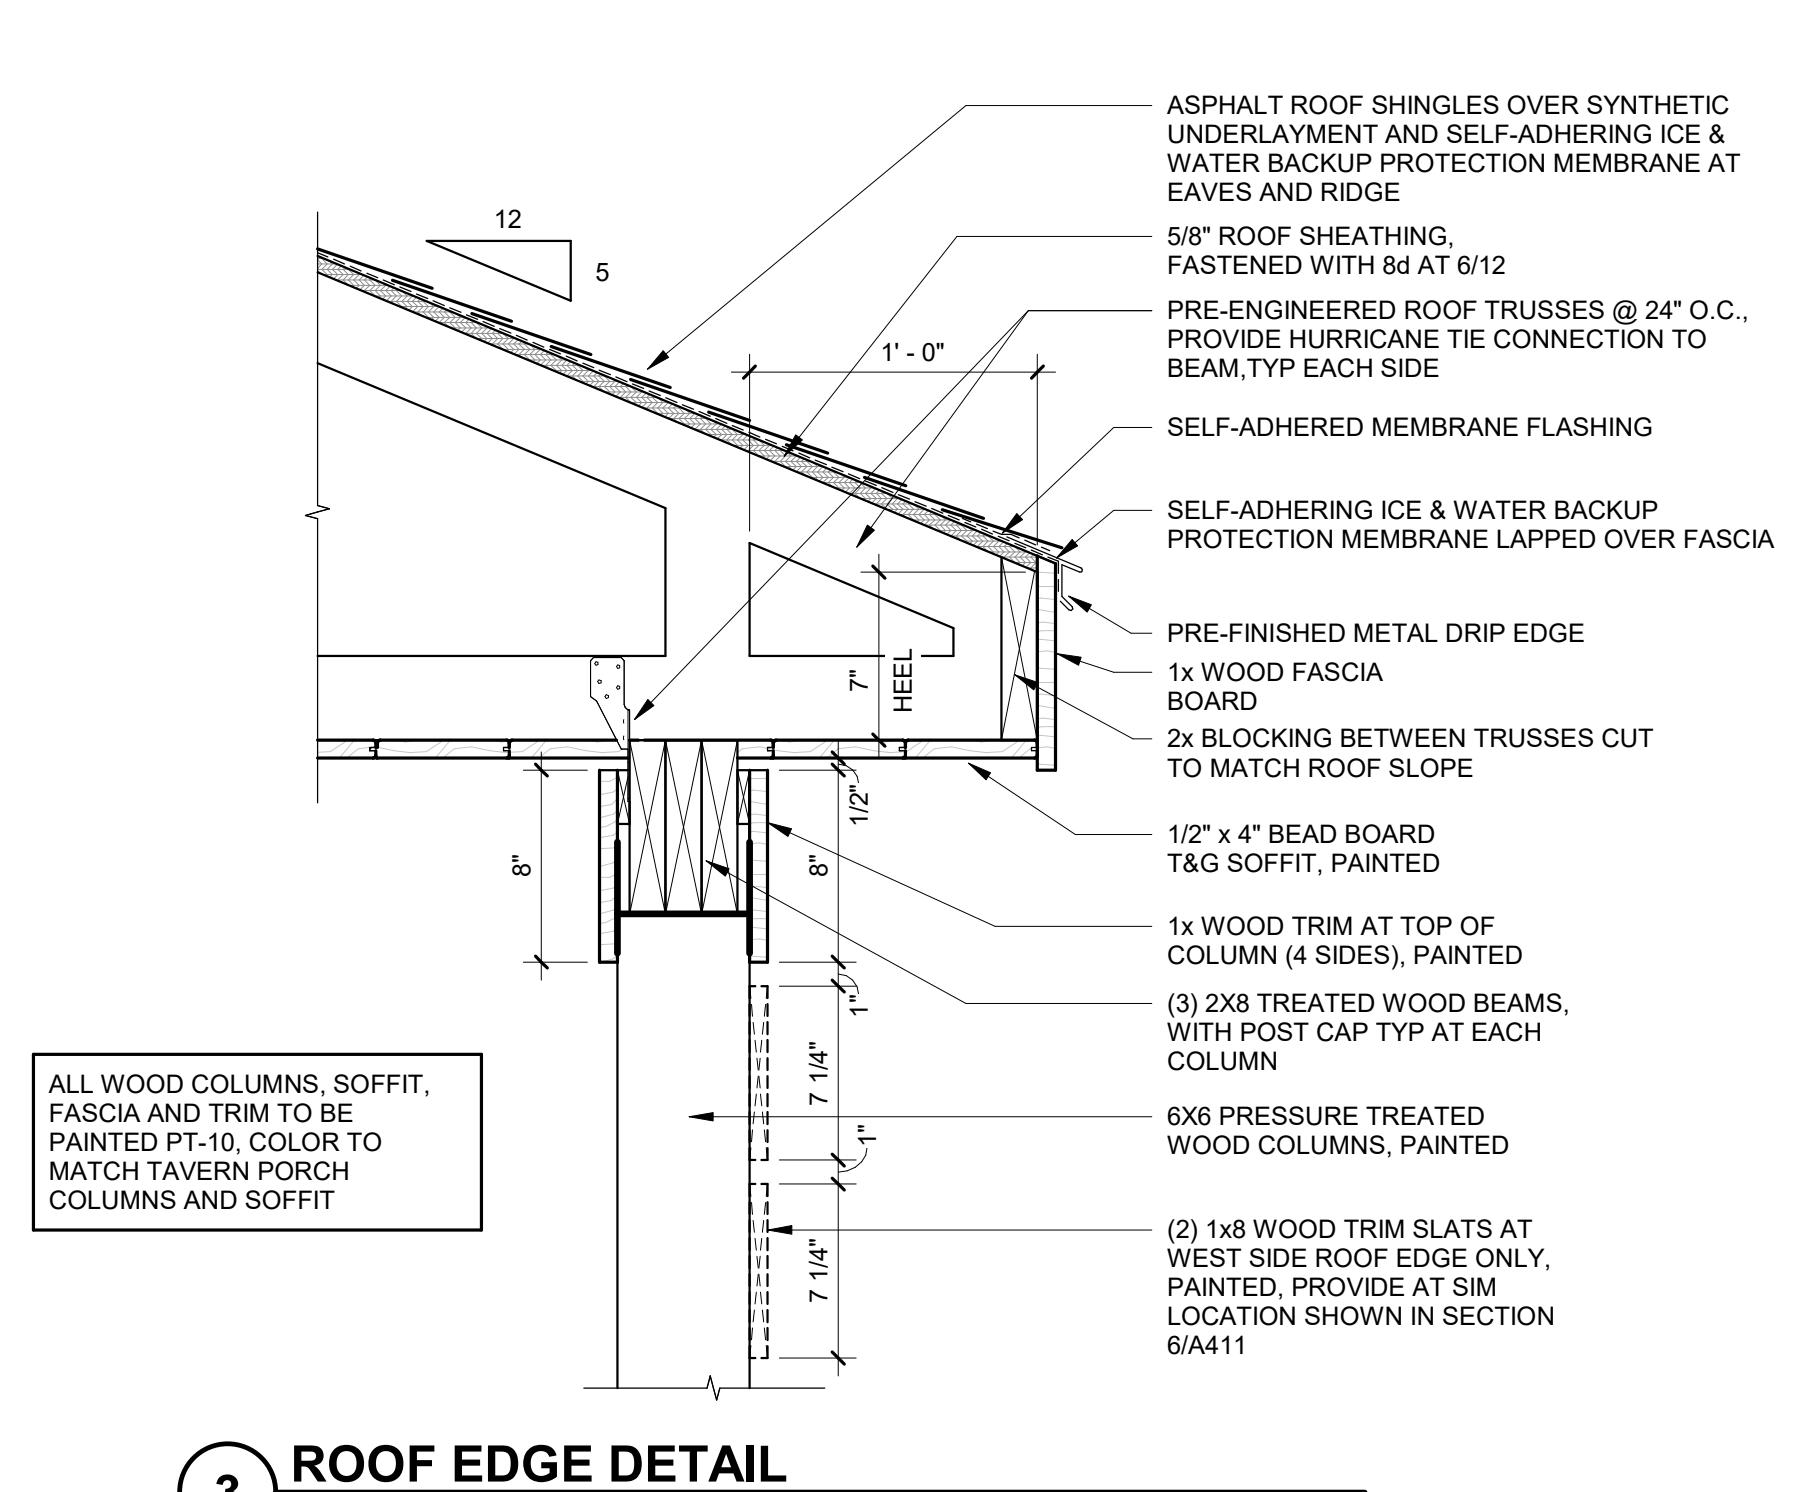

3 ROOF EDGE DETAIL

1 1/2" = 1'-0"

State of Wisconsin
Department of Administration
Division of Facilities Development
Old World Wisconsin Ethnic Outdoor Museum
Town of Eagle, Wisconsin

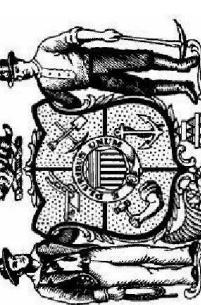

Old World Wisconsin Ethnic Outdoor Museum
Town of Eagle, Wisconsin

Tavern Renovations
Old World Wisconsin Ethnic Outdoor Museum
Wisconsin Historical Society
Town of Eagle, Wisconsin

Sheet Title:

TAVERN SUN SHADE ELEVATIONS, SECTIONS AND DETAILS

Revisions:

No.:

Date:

Description:

Graphic Scale:

See Details

DFD Number:

171K-04

Set Type:

BD

Date Issued:


9/8/2023

Sheet Number:


A411

Consultant:


NOTE:
SEE FLOOR PLAN FOR
LOCATIONS AND LENGTHS.

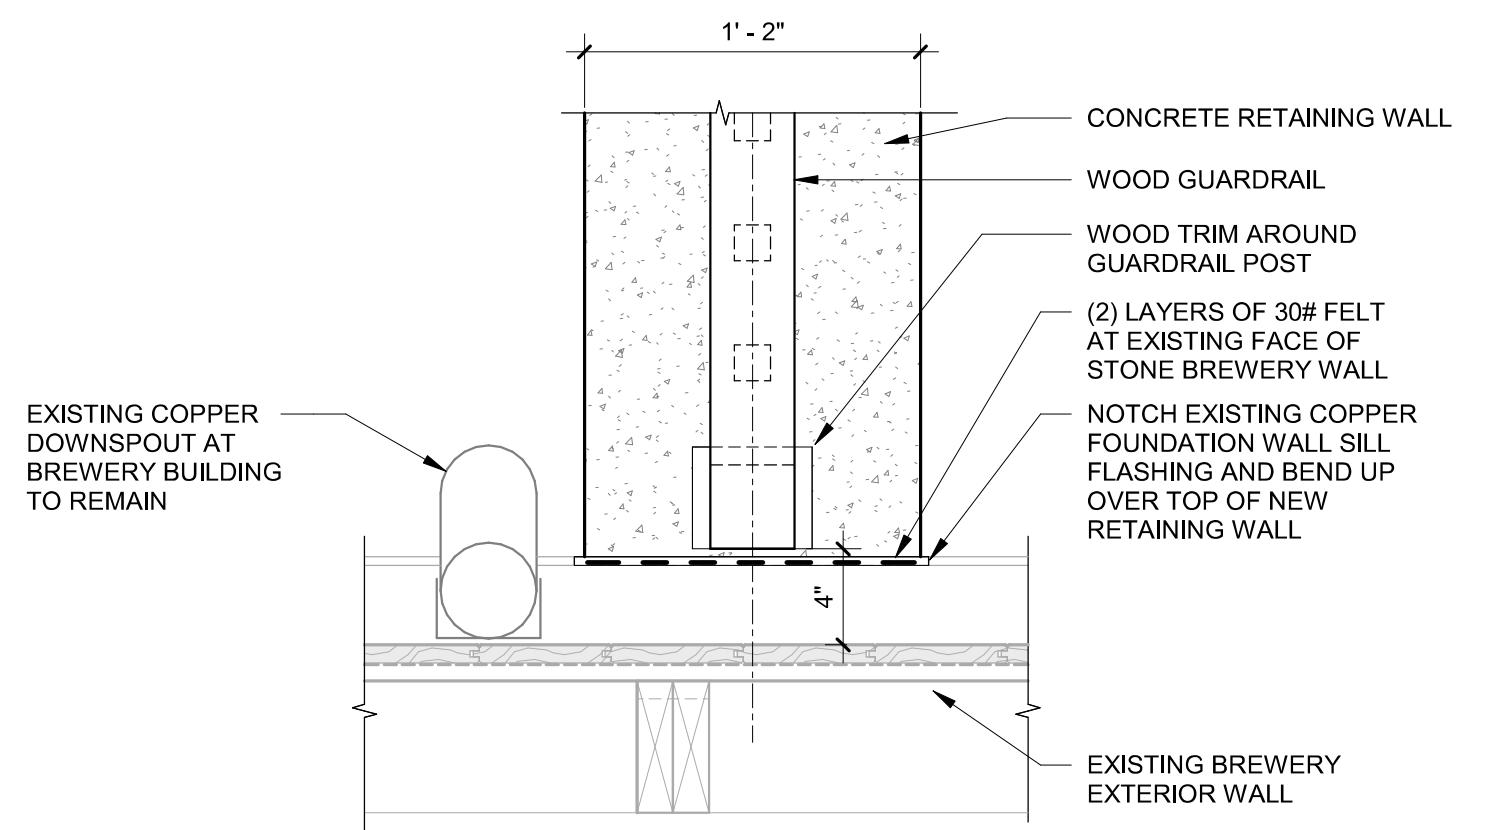


④ RETAINING WALL AT BREWERY

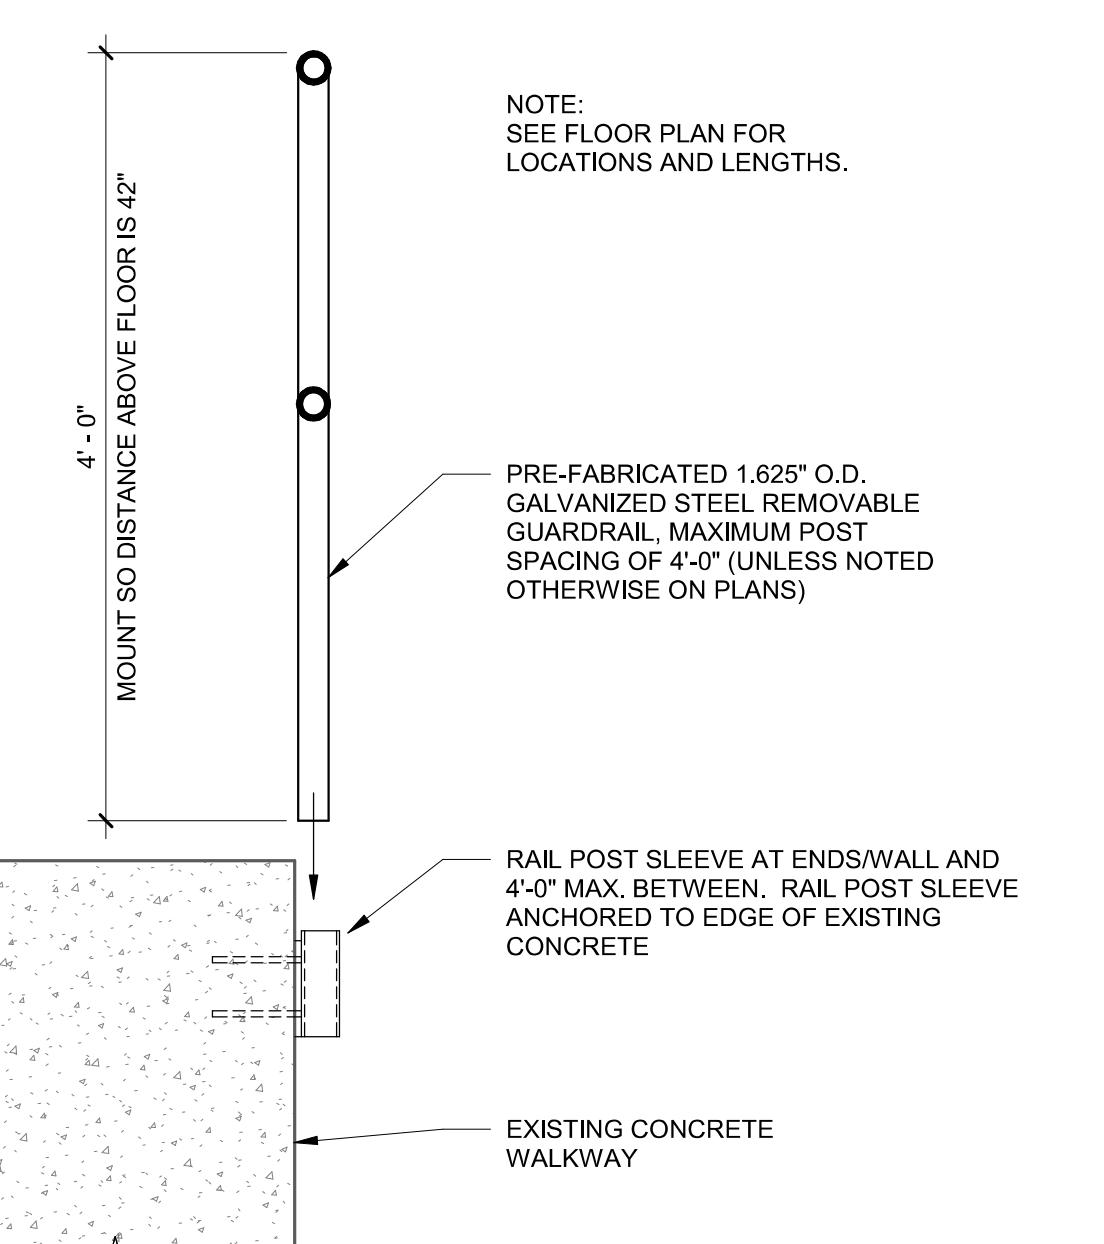


① REMOVABLE GUARDRAIL SECTION

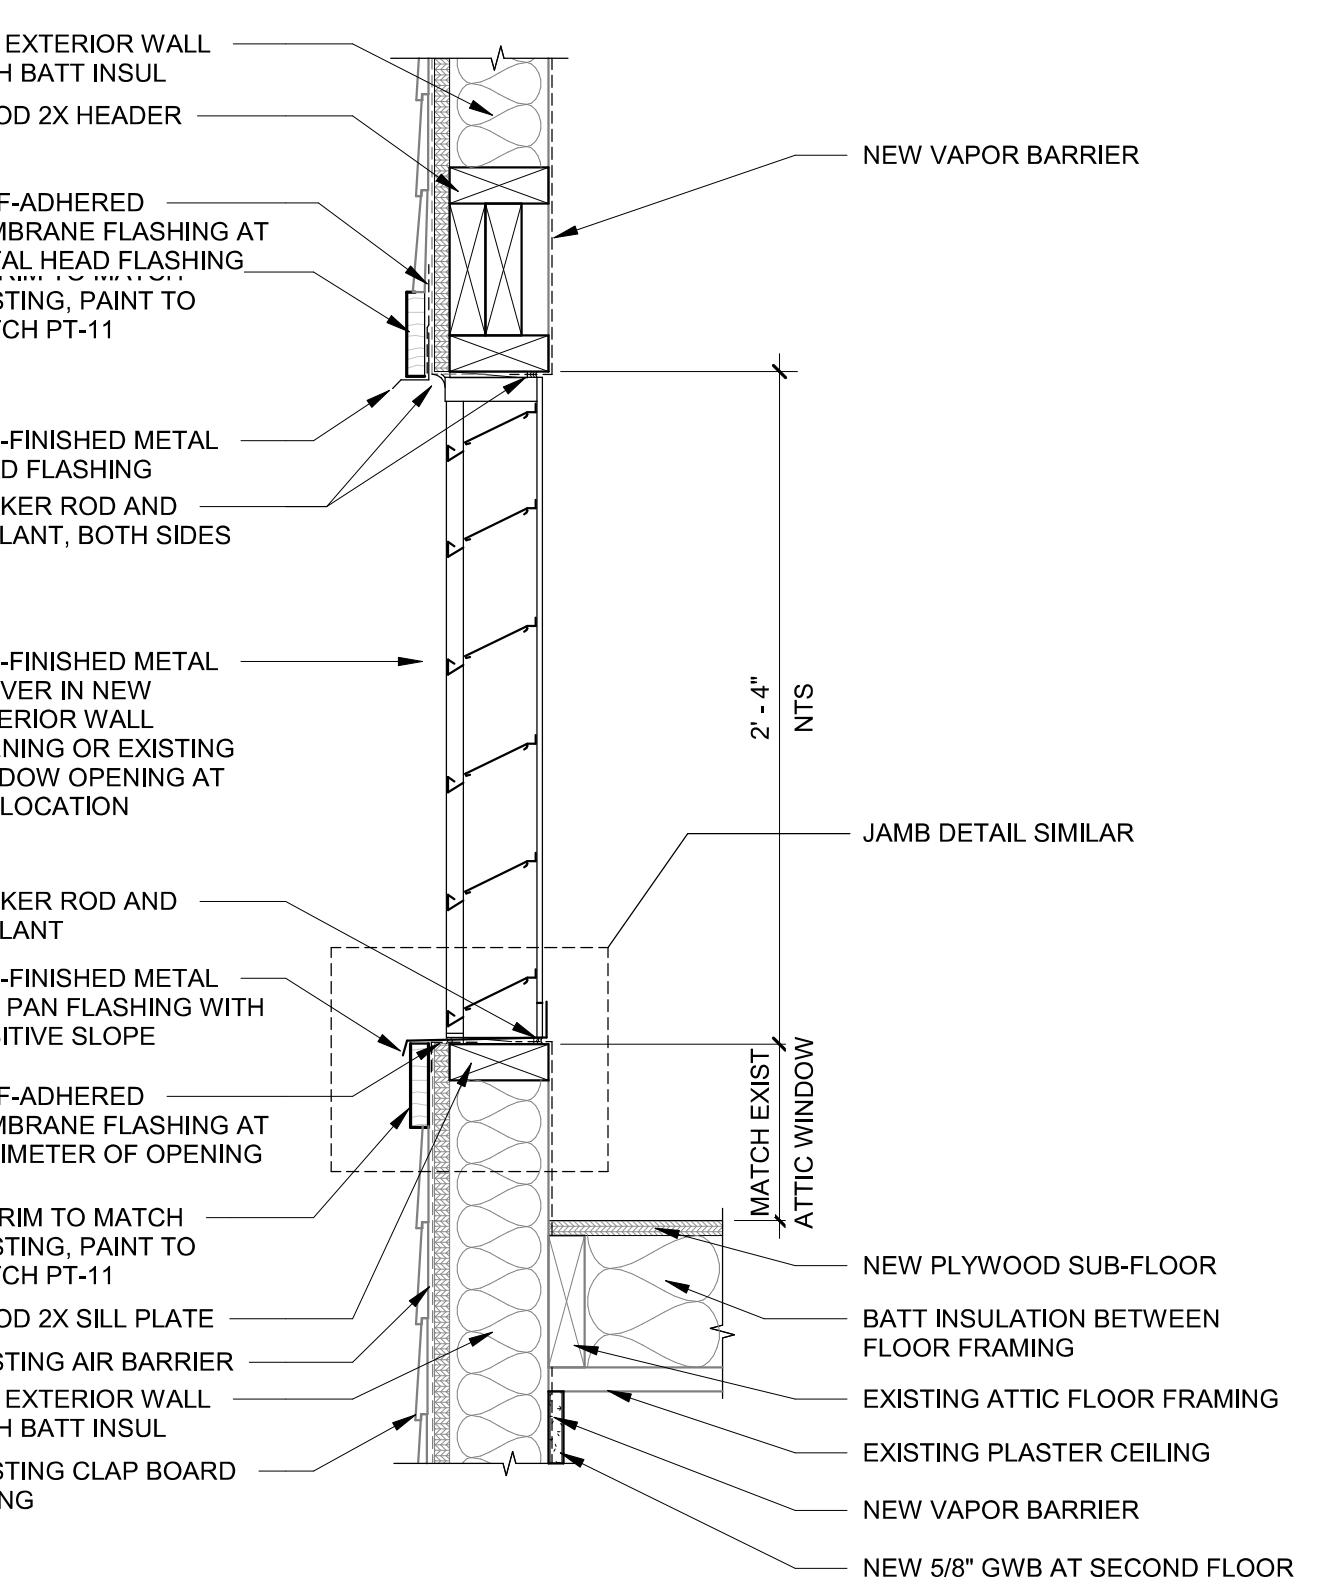

② ATTIC LOUVER DETAIL

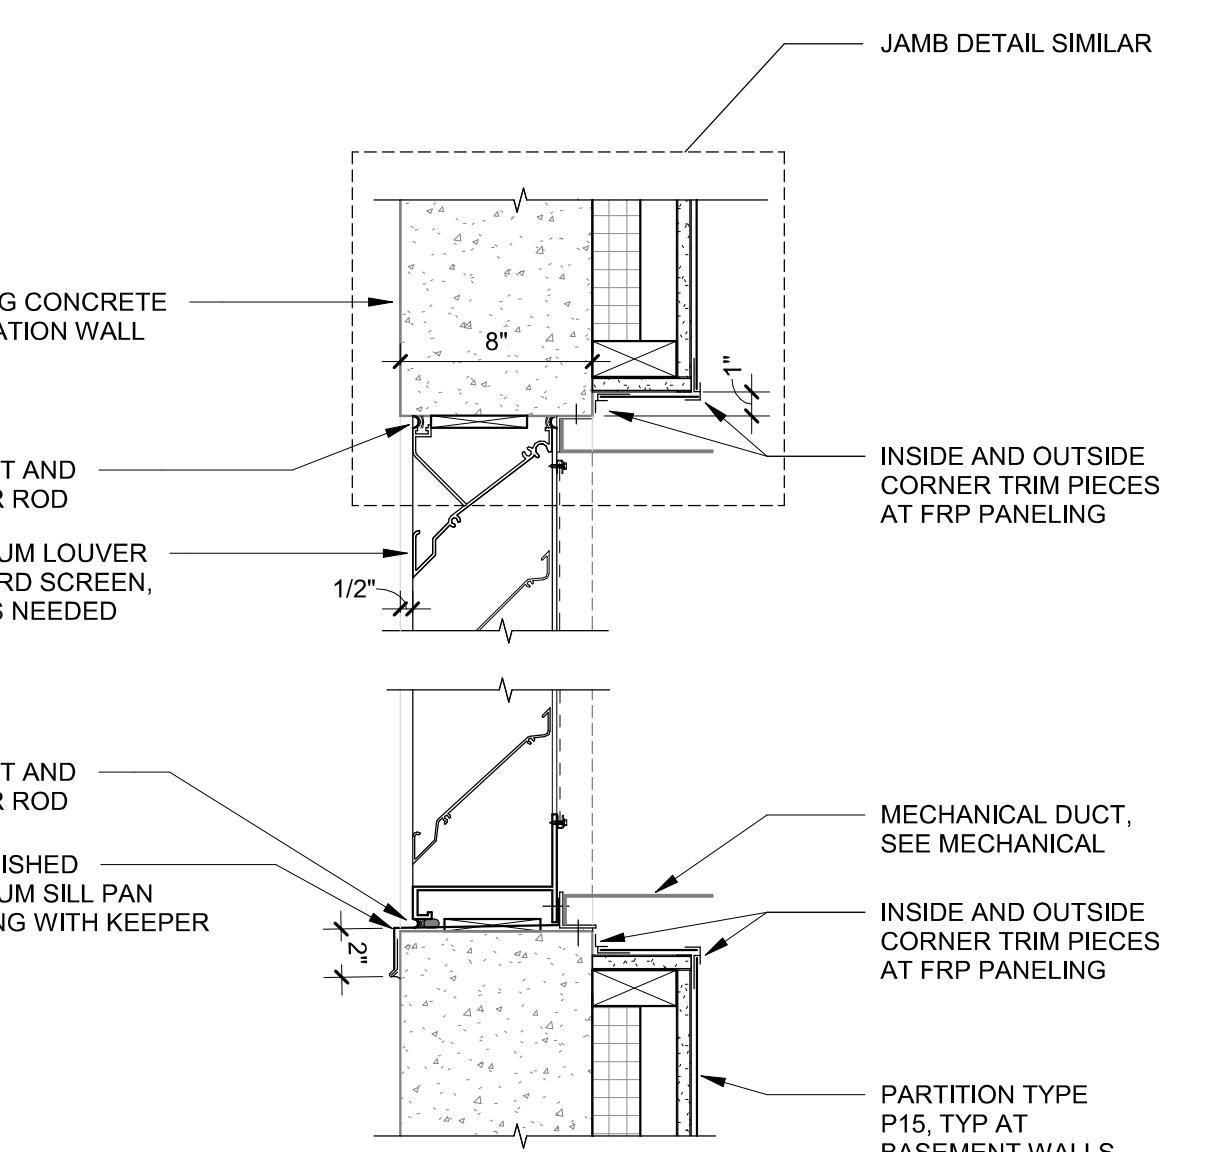

③ BASEMENT LOUVER DETAIL

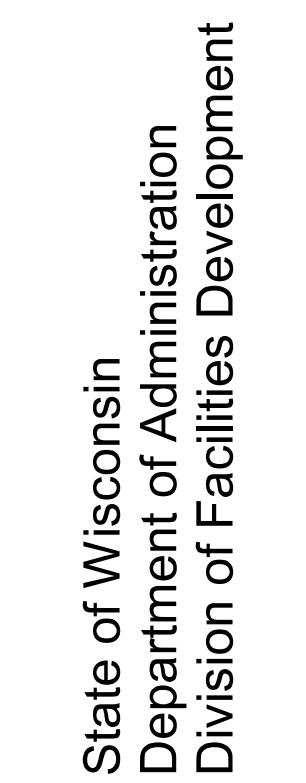


Tavern Renovations
Old World Wisconsin Ethnic Outdoor Museum
Wisconsin Historical Society
Town of Eagle, Wisconsin

Sheet Title: TAVERN DETAILS


Revisions:
No. Date: Description:

Graphic Scale	See Details
DRD Number	171K-04
Set Type	BD
Date Issued	9/8/2023
Sheet Number	A511

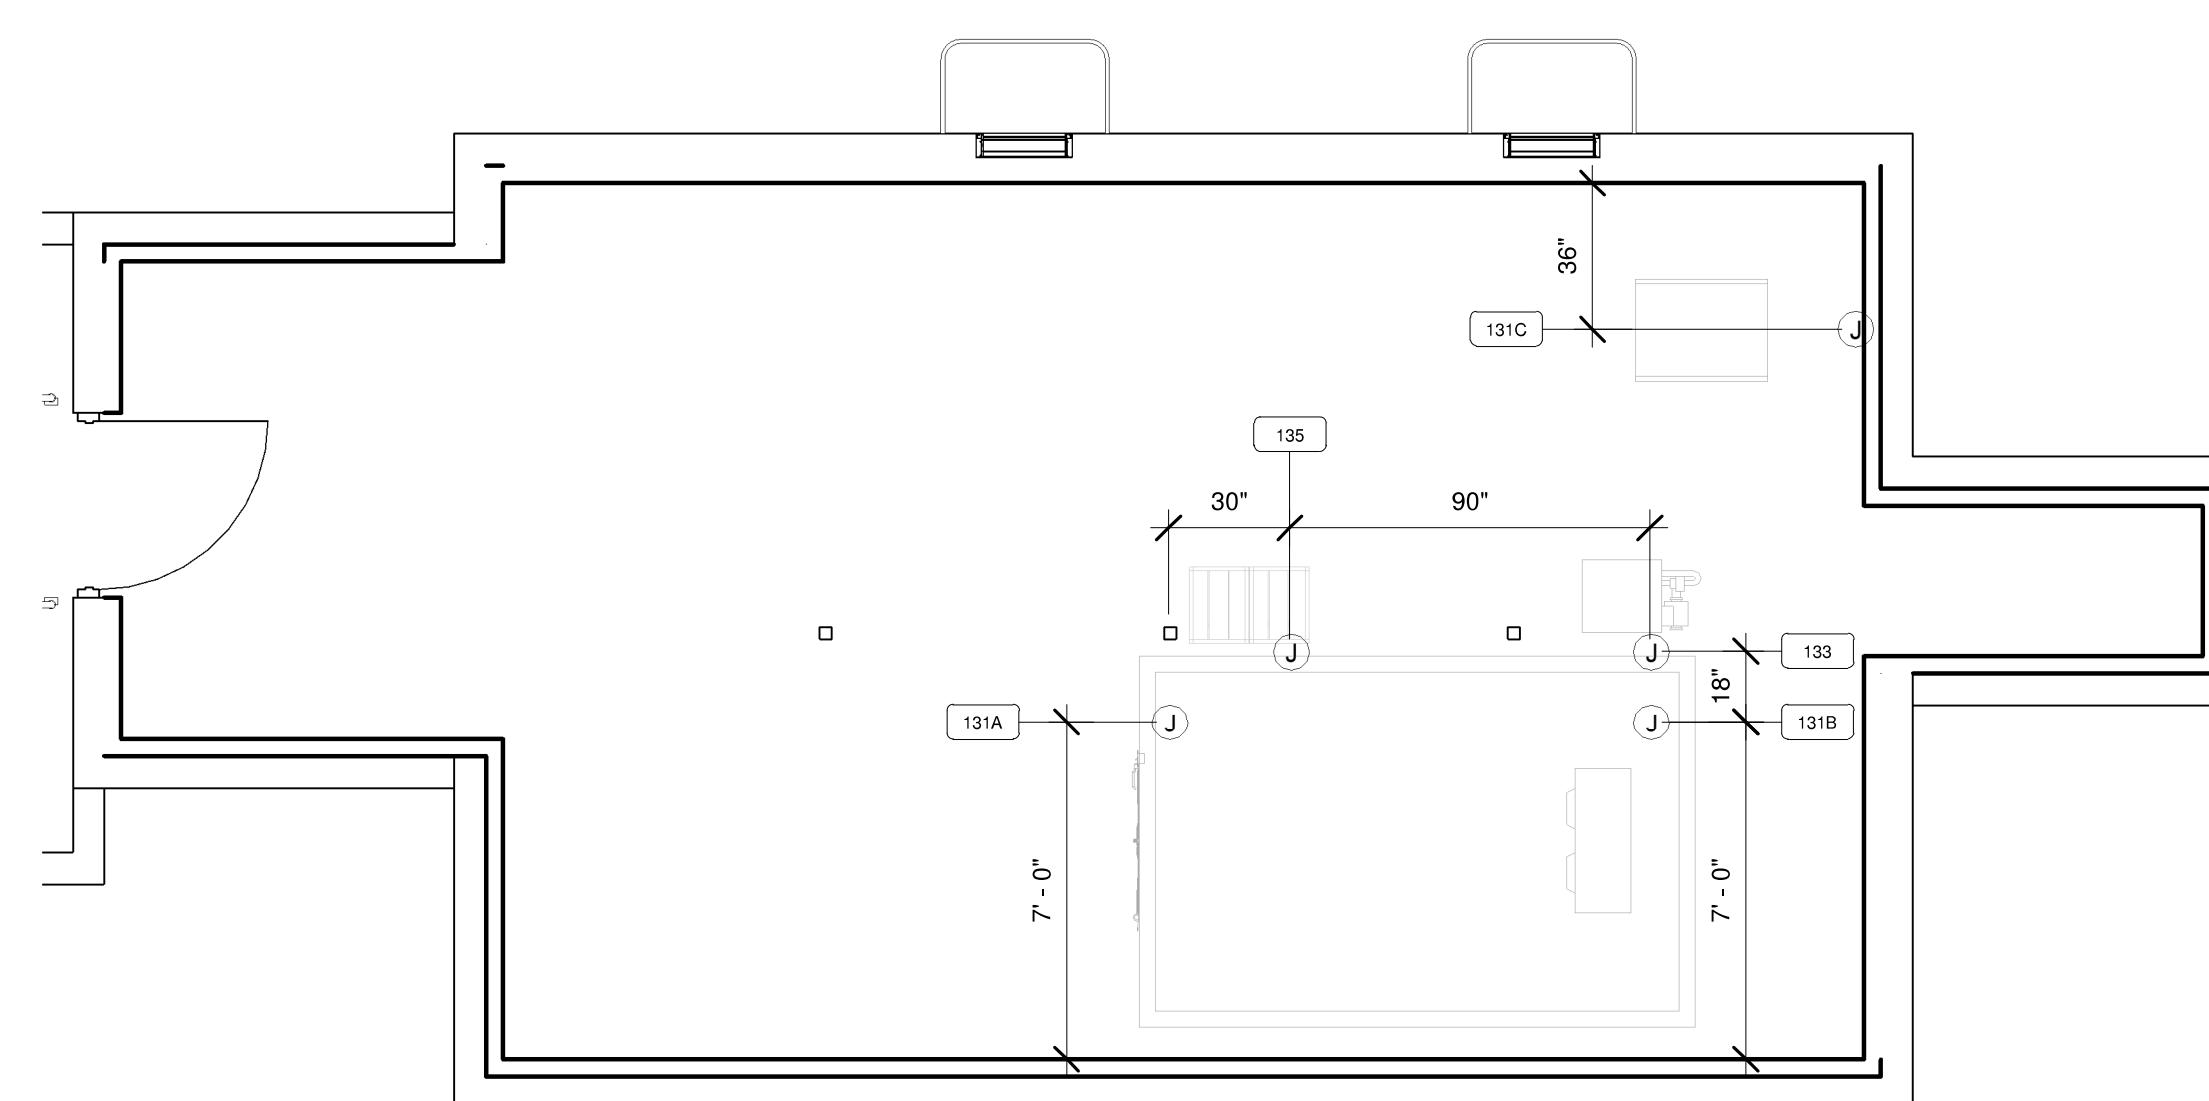

① Electrical Rough-in Plan - Lower Level

1/4" = 1'-0"

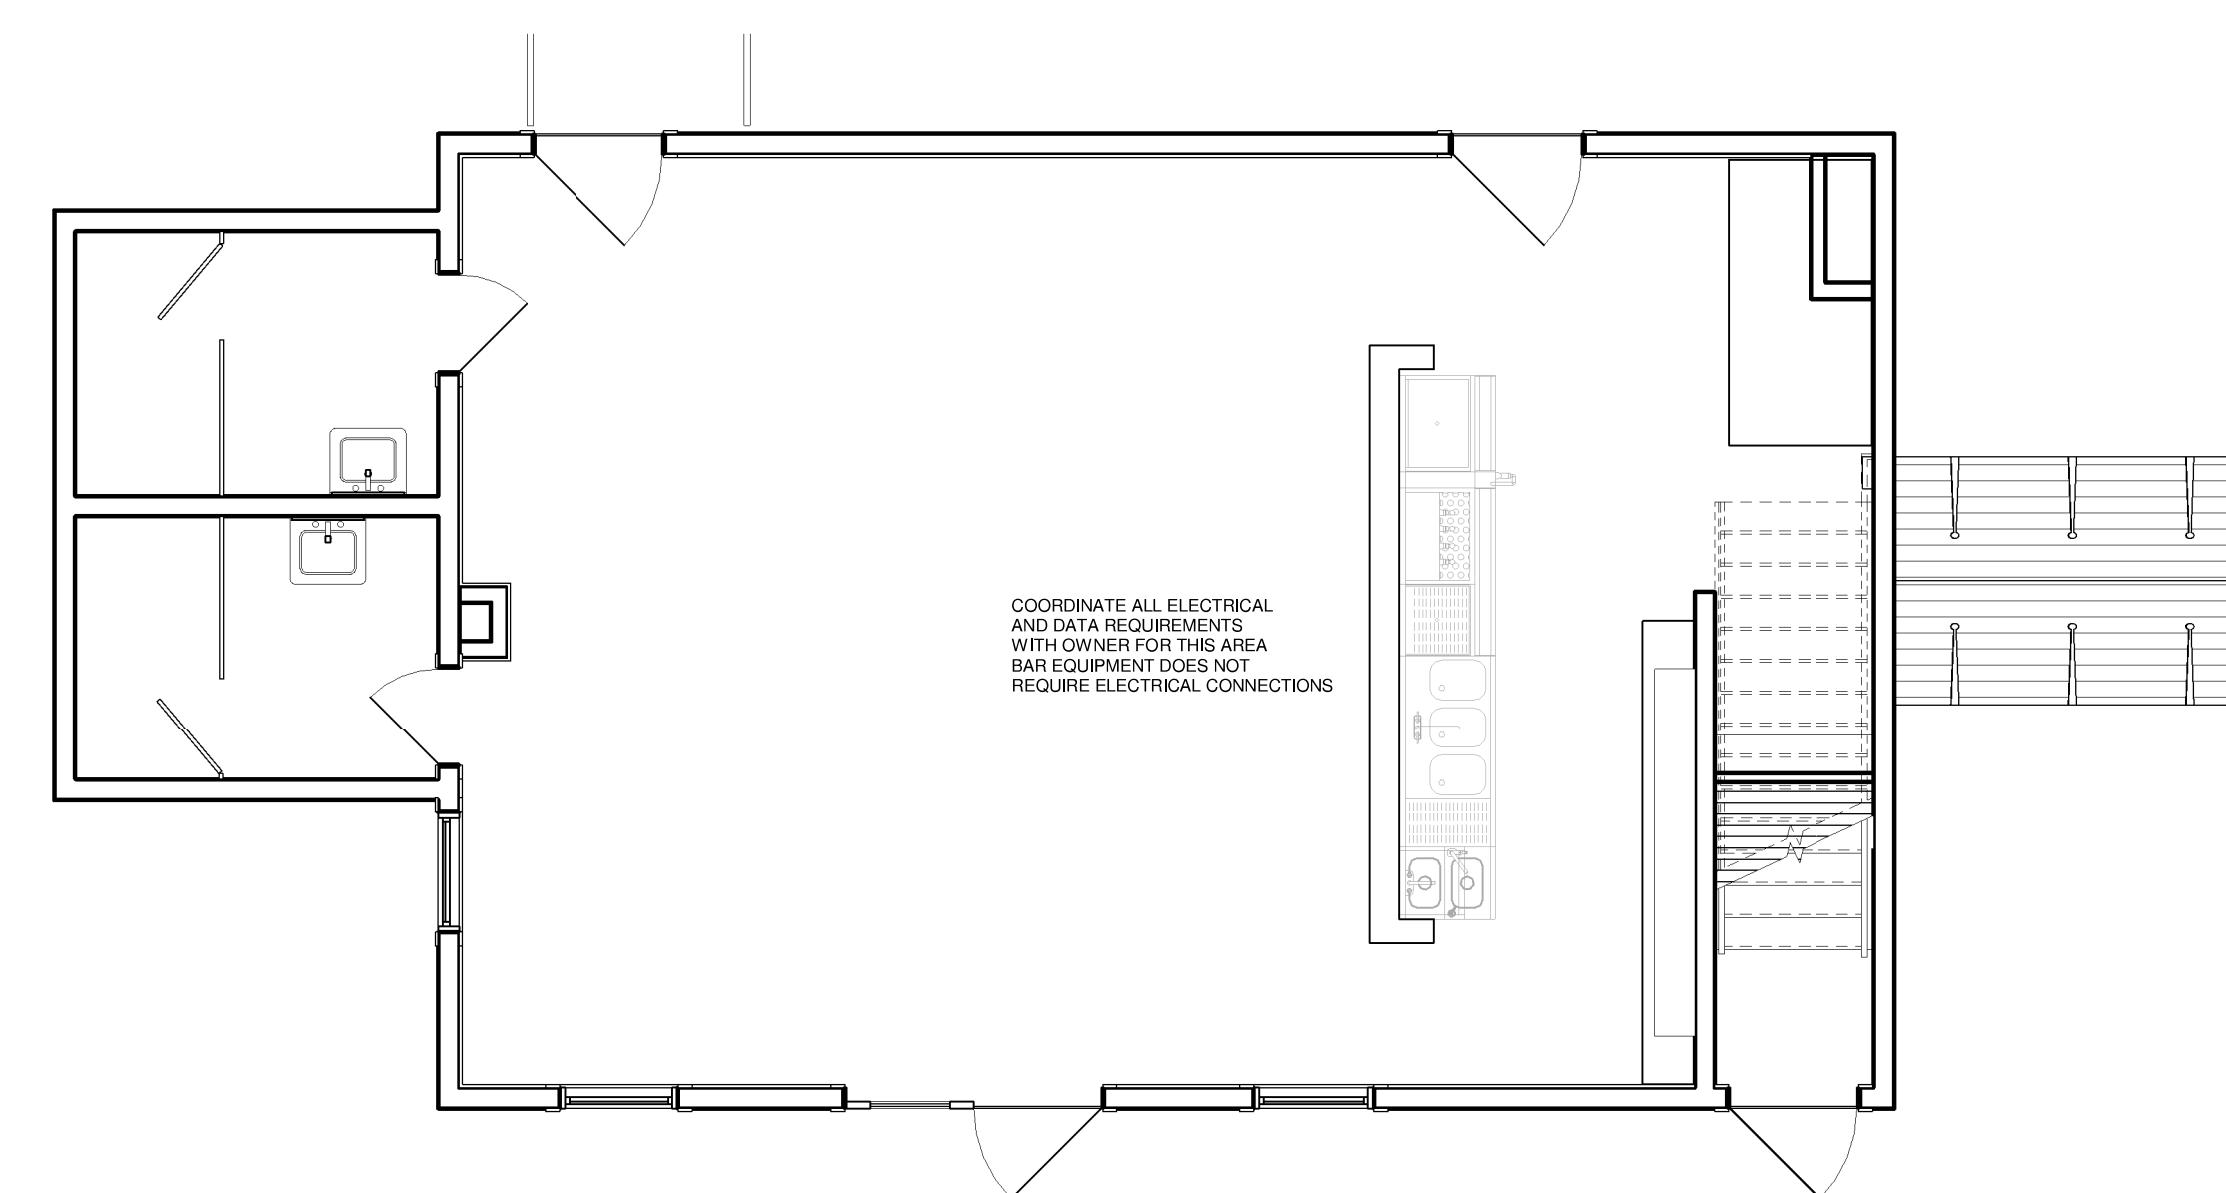


⑤ Electrical Rough-in Plan - First Floor

1/4" = 1'-0"

ELECTRICAL CONNECTION SCHEDULE

- 131A 115/1 J-BOX FROM ABOVE.
EC TO WIRE FROM ROUGH-IN TO DOOR PANEL CONNECTION AND TO LIGHTS.
- 131B 115/1 J-BOX FROM ABOVE - 8 AMPS
EC TO WIRE TO EVAPORATOR COIL CONNECTION POINT.
- 131C 208/3 J-BOX DISCONNECT - VERIFY LOCATION - 5.7 AMPS RLA
EC TO WIRE FROM DISCONNECT TO CONDENSING UNIT.
COORDINATE EXACT LOCATION WITH GC. 15.0 AMP MAXIMUM CIRCUIT.
- 133 115/1 J-BOX FROM ABOVE - 16.0 AMPS
EC TO FURNISH AND INSTALL GFCI D.O. IN STAINLESS STEEL HOUSING @ 48" AFF.
SECURE CONDUIT AND OUTLET TO EXTERIOR OF WALK-IN COOLER.
- 135 115/1 J-BOX FROM ABOVE - 16.0 AMPS
EC TO FURNISH AND INSTALL GFCI D.O. IN STAINLESS STEEL HOUSING @ 48" AFF.
SECURE CONDUIT AND OUTLET TO EXTERIOR OF WALK-IN COOLER.

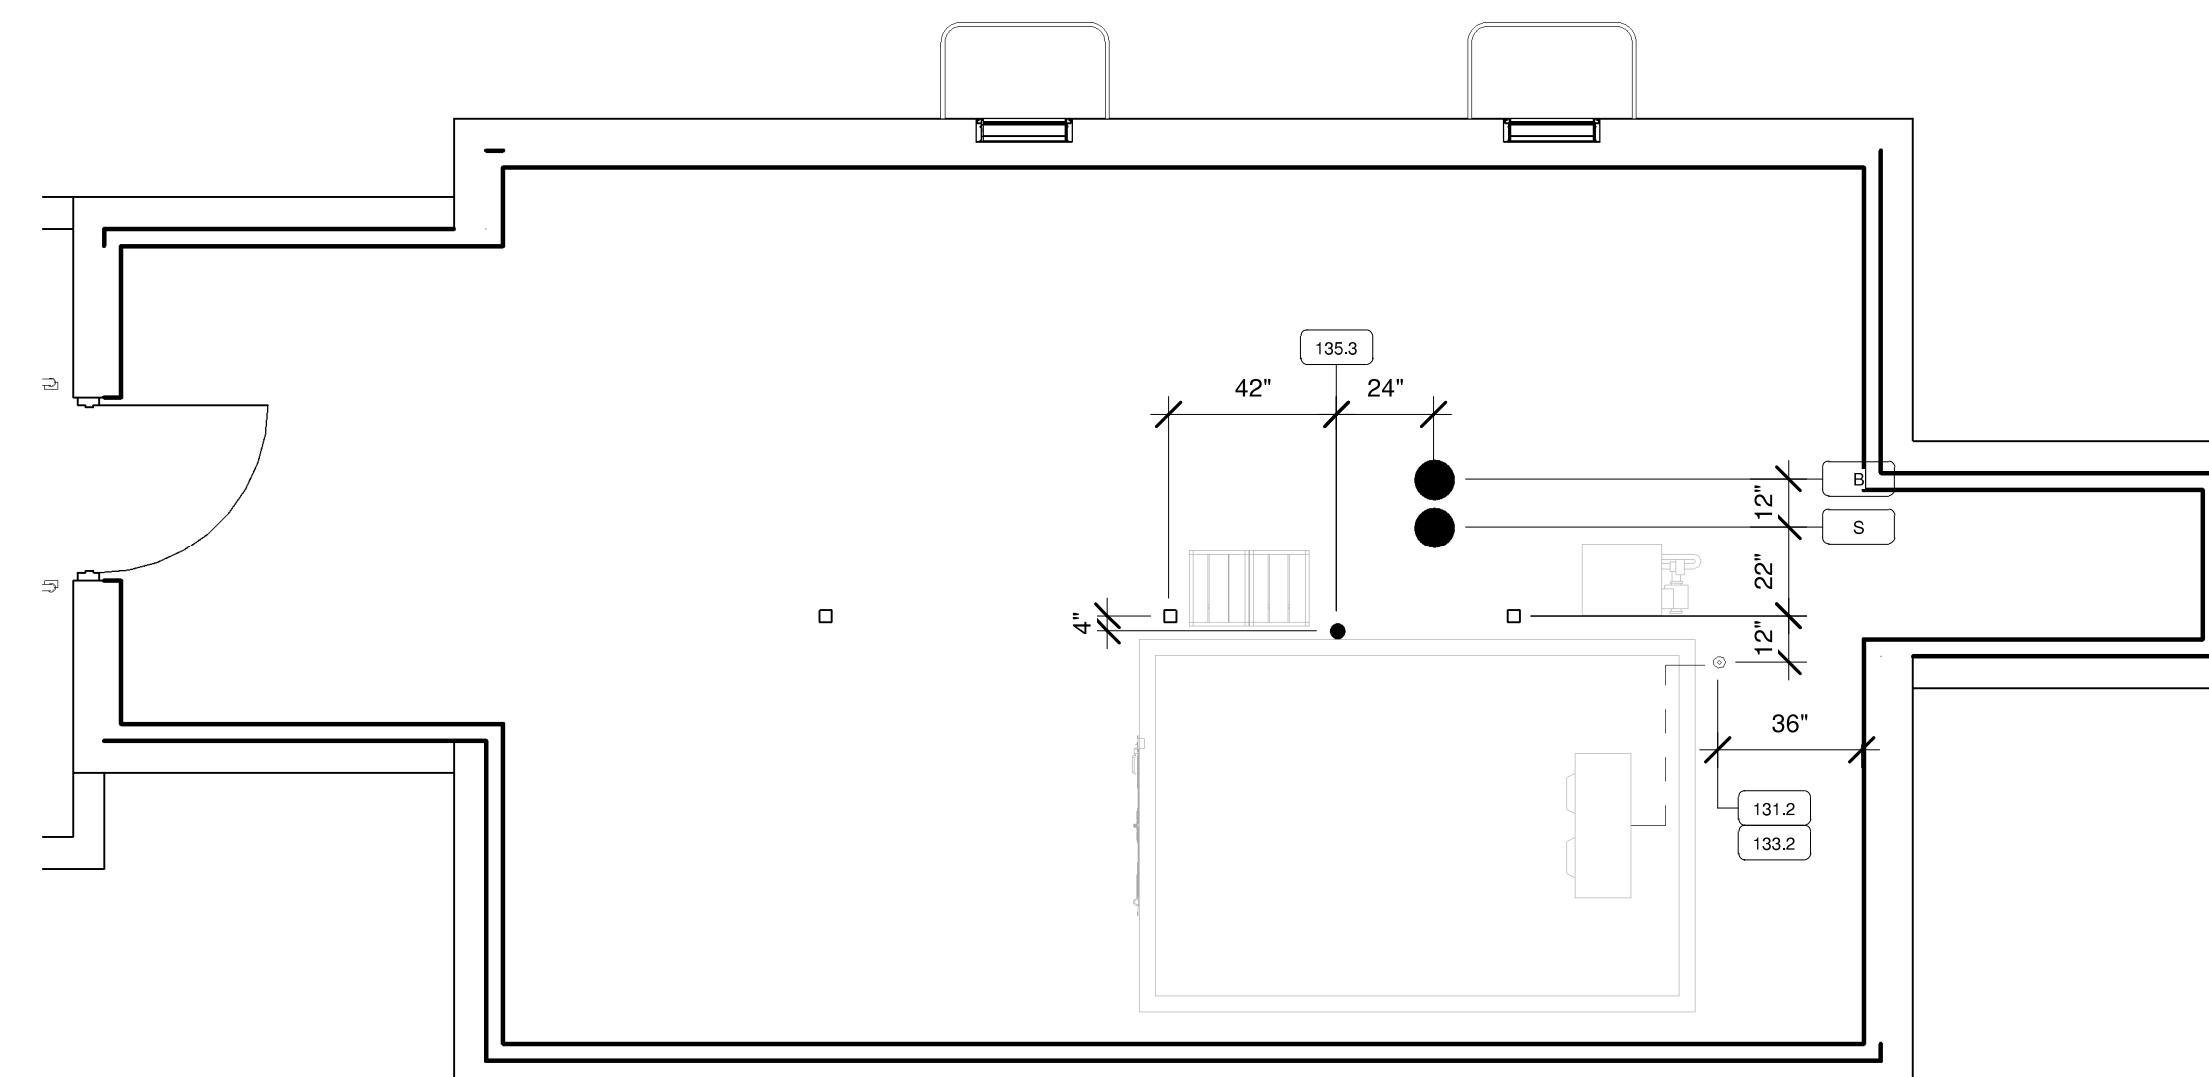


② Plumbing Rough-in Plan - Lower Level

1/4" = 1'-0"

PLUMBING CONNECTION SCHEDULE

- 131.2 3" HUB DRAIN STUB UP 3" AFF.
PC TO CONNECT FROM COIL CONDENSATE DRAIN TO HUB DRAIN.
AIR GAP REQUIRED. TRAP OUTSIDE OF BOX. COPPER PIPING.
- 133.2 CONNECT TO HUB DRAIN LISTED AS 131.2
PC TO CONNECT FROM BEER SYSTEM TO HUB DRAIN.
DRAIN HOSE BY FEC. SECURE HOSE OVER HUB DRAIN.
- 135.3 1/2" CW FROM ABOVE TO 68" AFF.
SECURE PIPING TO EXTERIOR OF WALK-IN COOLER.
VERIFY REQUIREMENTS WITH SODA SUPPLIER.

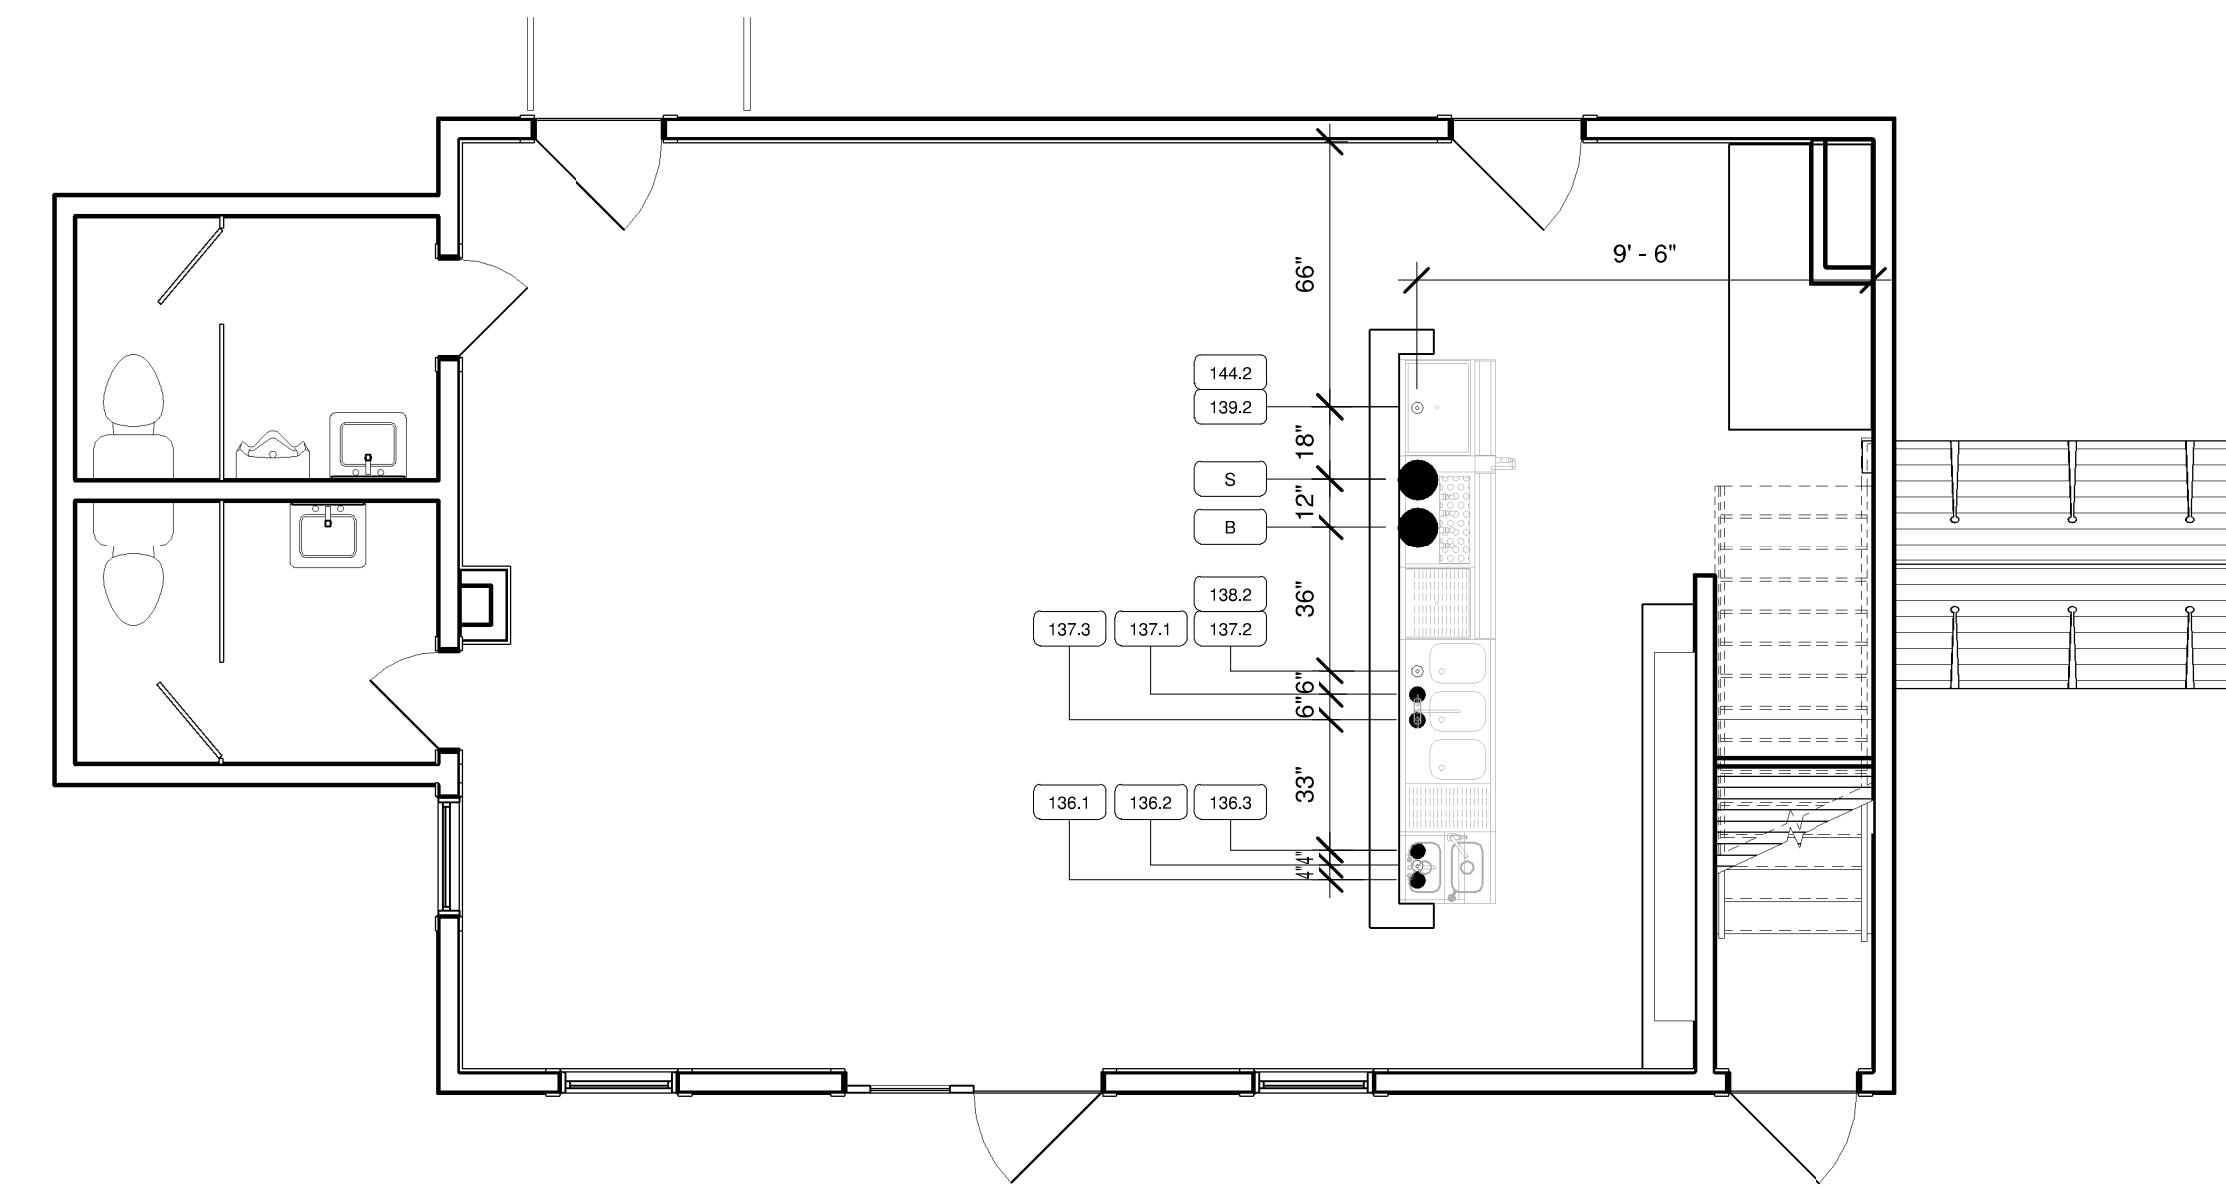

⑥ Plumbing Rough-in Plan - First Floor

1/4" = 1'-0"

PLUMBING CONNECTION SCHEDULE

- 136.1 1/2" HW STUB UP 8" AFF.
PC TO CONNECT TO FAUCET.
- 136.2 3" HUB DRAIN STUB UP 3" AFF.
PC TO CONNECT FROM SINK DRAINS TO HUB DRAIN.
AIR GAP REQUIRED.
- 136.3 1/2" CW STUB UP 8" AFF.
PC TO CONNECT TO FAUCET.
- 137.1 1/2" HW STUB UP 8" AFF.
PC TO CONNECT TO FAUCET.
- 137.2 3" HUB DRAIN STUB UP 3" AFF.
PC TO CONNECT FROM SINK DRAINS TO HUB DRAIN.
AIR GAP REQUIRED.
- 137.3 1/2" CW STUB UP 8" AFF.
PC TO CONNECT TO FAUCET.
- 138.2 CONNECT TO HUB DRAIN LISTED AS 137.2
PC TO CONNECT TO FROM DRAIN BOARD TO HUB DRAIN.
AIR GAP REQUIRED.
- 139.2 1/2" HB STUB UP 3" AFF.
PC TO CONNECT FROM BEER TROUGH TO HUB DRAIN.
AIR GAP REQUIRED.
- 144.2 CONNECT TO HUB DRAIN LISTED AS 139.2
PC TO CONNECT TO FROM ICE BIN TO HUB DRAIN.
AIR GAP REQUIRED.

Tavern Renovations
Old World Wisconsin Ethnic Outdoor Museum
Wisconsin Historical Society
Town of Eagle, Wisconsin

Sheet Title:
TAVERN FOODSERVICE UTILITY ROUGH-IN PLANS

Revisions:
No. Date: Description:

Graphic Scale	See Details
DRD Number	171K-04
Set Type	BD
Date Issued	9/8/2023
Sheet Number	K112

PLUMBING SYMBOL SCHEDULE		
	AFF	ABOVE FINISHED FLOOR
	AP	ACCESS PANEL
	ANB	ACID NEUTRALIZATION BASIN
	BFP/ RPB	BACKFLOW PREVENTER
		BALL VALVE
	BT	BATHTUB
		BUTTERFLY VALVE
		CALIBRATED BALANCE VALVE, INLINE FLOW SIGHT INDICATOR & CHECK VALVE
		CAP EXISTING PIPE
		CHECK VALVE
	CP	CIRCULATING PUMP
	CO/WCO	CLEANOUT OR WALL CLEANOUT (AS NOTED)
	CLVTR	CLEARWATER VENT THRU ROOF
	WCL	COMBINATION WATER CLOSET LAVATORY
	DD	DECK DRAIN
		DETAIL AND ISOMETRIC REFERENCE
	DN	DOWN
	DSN	DOWNSPOUT NOZZLE
		DRAINAGE/WATER FIXTURE UNIT TAG
	DBT	DRAINBACK TANK
	DTR	DRAIN TILE RECEIVER
	DF	DRINKING FOUNTAIN
	EWC	ELECTRIC WATER COOLER
	EEW	EMERGENCY EYE WASH
	EEWS	EMERGENCY EYE WASH SHOWER
		EQUIPMENT / FIXTURE DEMOLITION
	EXIST	EXISTING
	ET	EXPANSION TANK
	FFE=100.00	FINISHED FLOOR ELEVATION
	FCO	FLOOR CLEANOUT
	FD	FLOOR DRAIN
	FS	FLOOR SINK
	FFD	FLUSHING FLOOR DRAIN
	FSEC	FOOD SERVICE EQUIPMENT CONTRACTOR (DIVISION 11)
		FOOD SERVICE EQUIPMENT TAG
	HS	HAND SINK
	HB/WH	HOSE BIB OR WALL HYDRANT (AS NOTED)
	HD	HUB DRAIN
	HPT	HYDRO PNEUMATIC TANK
	IW	INDIRECT WASTE


NOTE: ALL SYMBOLS MAY NOT BE USED FOR THIS PROJECT

PLUMBING SYMBOL SCHEDULE		
IE=000.00	IE	INVERT ELEVATION OF SEWER OR DRAIN
	LT	LAUNDRY TRAY
	LAV	
	LI	LINT INTERCEPTOR
	MB	MOP BASIN
		NATURAL GAS SHUT-OFF VALVE
		NEW PIPE CONNECTION TO EXISTING
		PIPE CAP
	PC	PLUMBING (DIVISION 22) CONTRACTOR
	PRV	PRESSURE REDUCING VALVE
	RV	RELIEF VENT
		RISING STEM GATE VALVE
(○)	RD/OD	ROOF DRAIN / OVERFLOW DRAIN
	SE	SEWAGE EJECTOR
	SH	SHOWER
	S	SINK
	SV	STACK VENT
	ST	STORAGE TANK
	COND	STORM / CLEARWATER CONDUCTOR
	SP	SUMP PUMP
	TMV	TEMPERATURE MIXING VALVE
	TT	TEMPERING TANK
	TD	TRENCH DRAIN
	TYP	TYPICAL
	UR	URINAL
	VS	VENT STACK
	VTR	VENT THRU ROOF
	AWC	WASHING MACHINE WALL BOX
	WS	WASTE STACK
	WC	WATER CLOSET
	WHA	WATER HAMMER ARRESTOR
	EWH	WATER HEATER ELECTRIC
	GWH	WATER HEATER GAS
	HWX	WATER HEATER STEAM
⊗		WATER MAIN VALVE AND BOX
	WS	WATER SOFTENER

NOTE: ALL SYMBOLS MAY NOT BE USED FOR THIS PROJECT

PLUMBING PIPE TYPES SCHEDULE		
EXISTING	NEW	
-140° -----	-140° -----	140° 140° HOT WATER
-140° -----	-140° -----	140° 140° HOT WATER RETURN
—CLV—	—CLV—	CLV CLEAR WATER VENT ABOVE FLOOR
—CLW—	—CLW—	CLW CLEAR WATER WASTE ABOVE FLOOR
—CSW—	—CSW—	CSW COLD SOFT WATER PIPING
—	—	CW COLD WATER
—A—	—A—	A COMPRESSED AIR
—	—	DEMO CLEAR WATER WASTE BELOW GROUND / FLOOR
—DT—	—DT—	DT DRAINTILE
—D—	—D—	D DRAIN PIPING
—GW—	—GW—	GW GREASE WASTE
—	—	HW HOT WATER
—	—	HWR HOT WATER RETURN
G	G	G NATURAL GAS
NP	NP	NP NON-POTABLE WATER
PD	PD	PD PUMP DISCHARGE EFFLUENT / SANITARY
PD	PD	PD PUMP DISCHARGE STORM / CLEAR WATER
—	—	STM STORM DRAIN ABOVE FLOOR
—	—	V VENT PIPE ABOVE FLOOR
—	—	W WASTE / SANITARY DRAIN ABOVE FLOOR

NOTE: ALL PIPE TYPES MAY NOT BE USED FOR THIS PROJECT

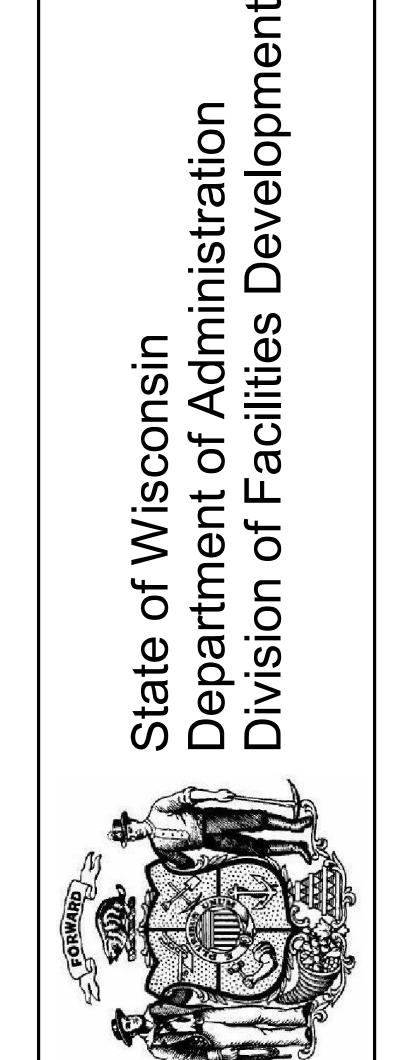


Tavern Renovations
Old World Wisconsin Ethnic Outdoor Museum
Wisconsin Historical Society
Town of Eagle, Wisconsin

Sheet Title:


TAVERN PLUMBING NOTES, SYMBOLS AND ABBREVIATIONS

Graphic Scale	See Details
DFD Number	171K-04
Set Type	BD
Date Issued	9/8/2023
Sheet Number	P001

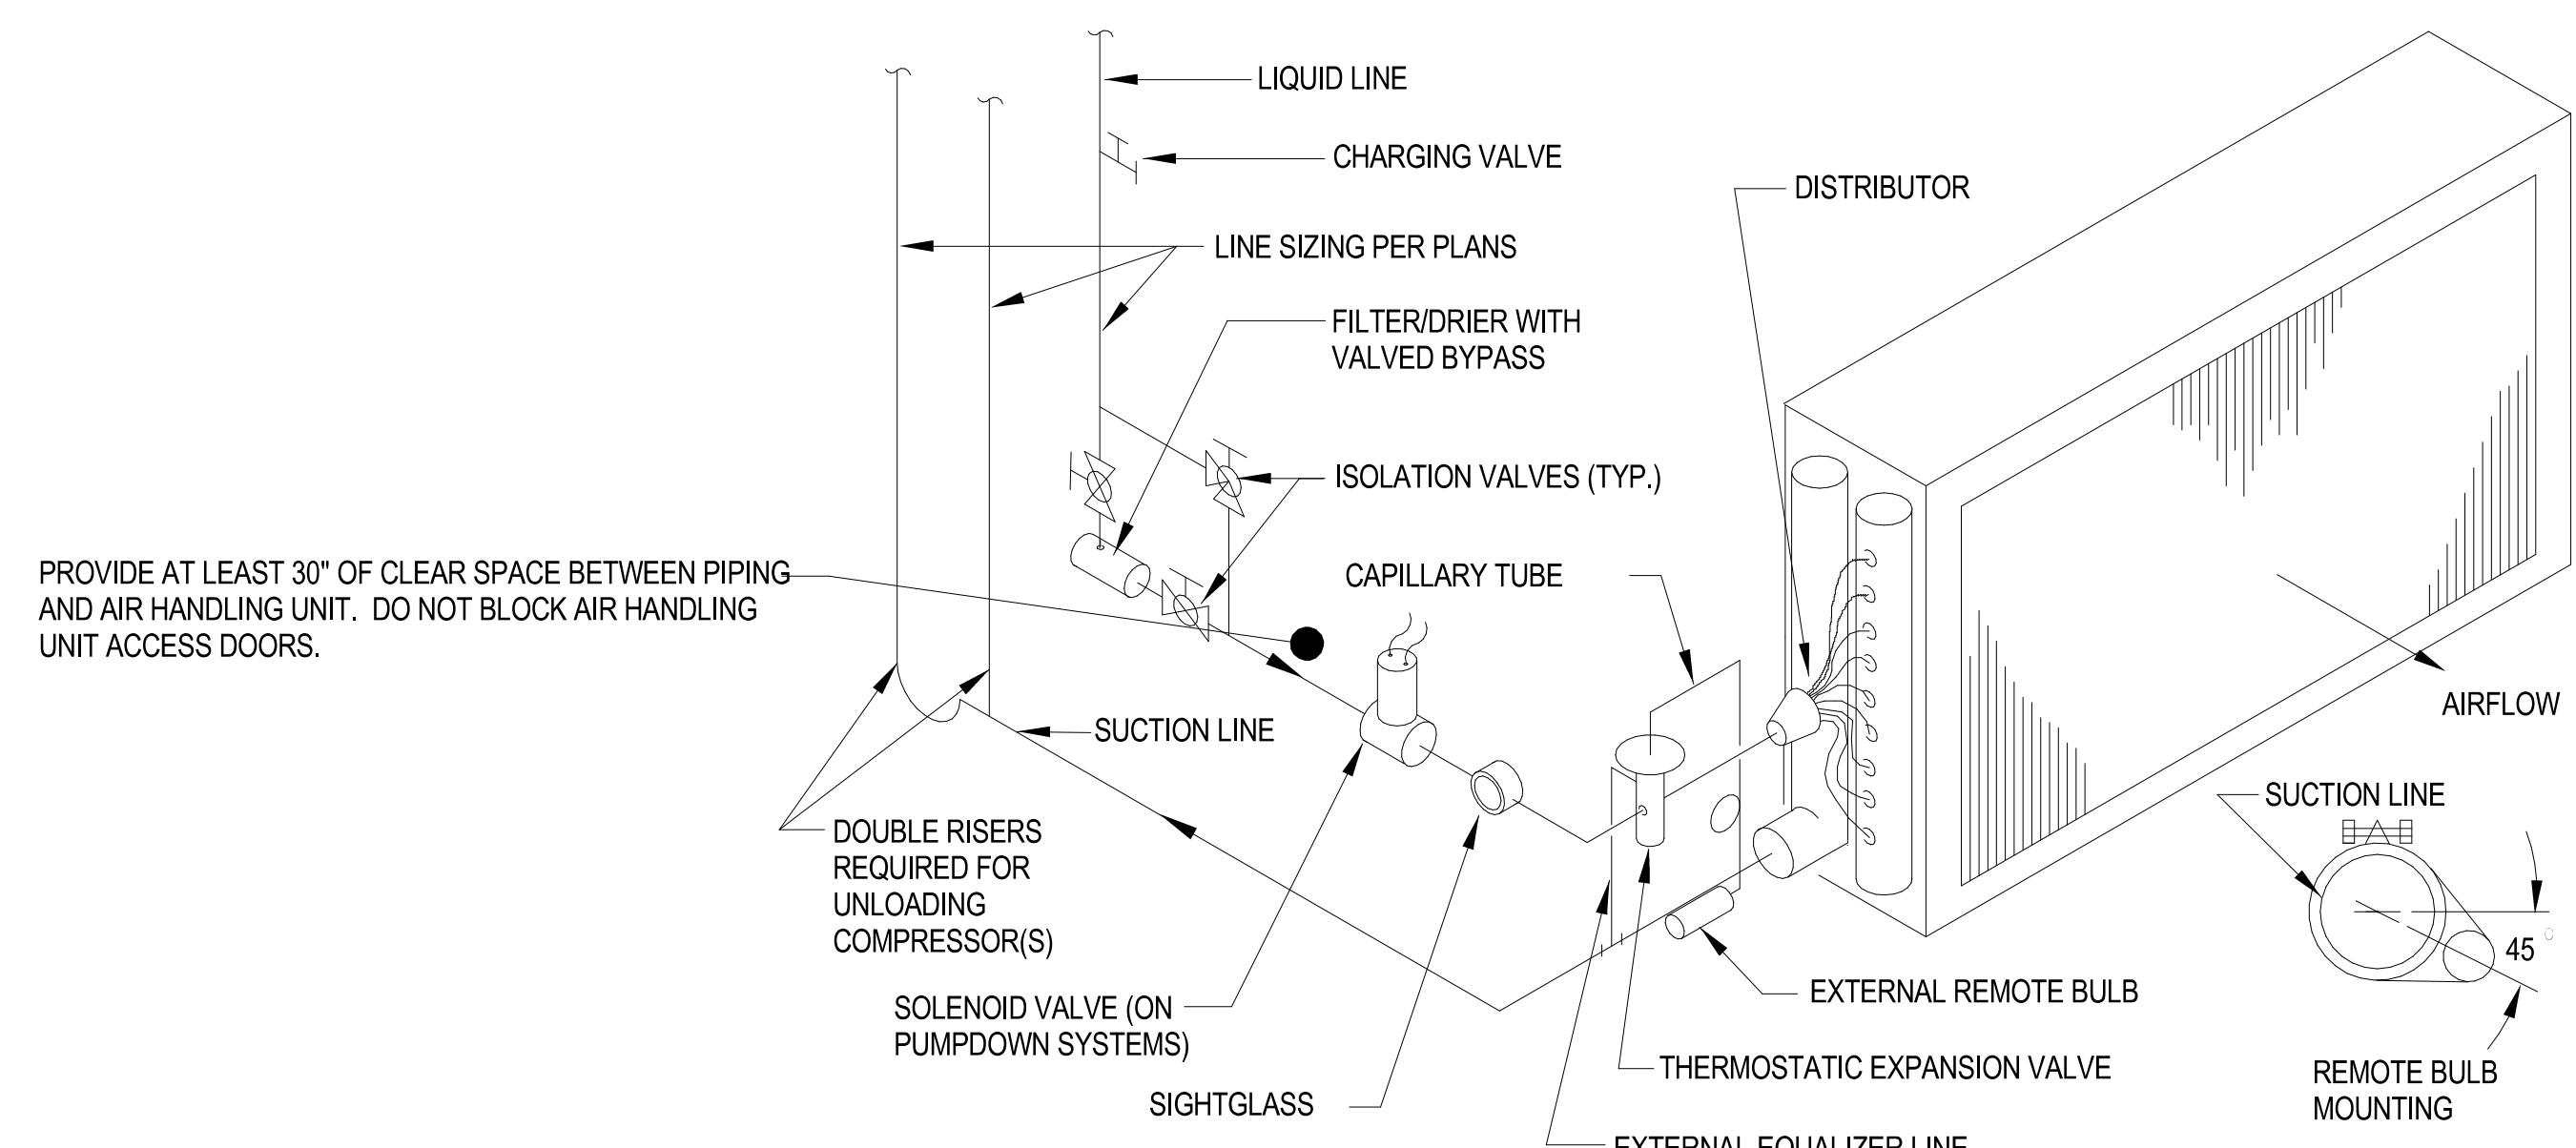


1 DETAIL - REFRIGERANT COIL PIPING

SCALE: NONE

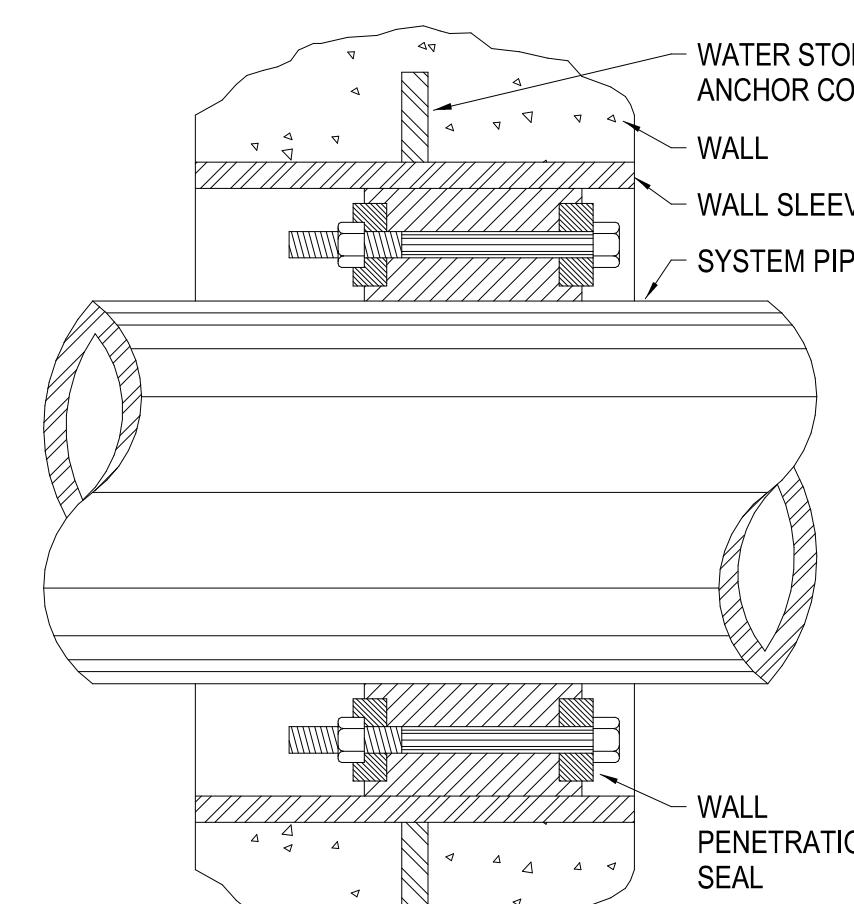

3 DETAIL - PIPE THRU WALL PENETRATION ASSEMBLY

SCALE: NONE

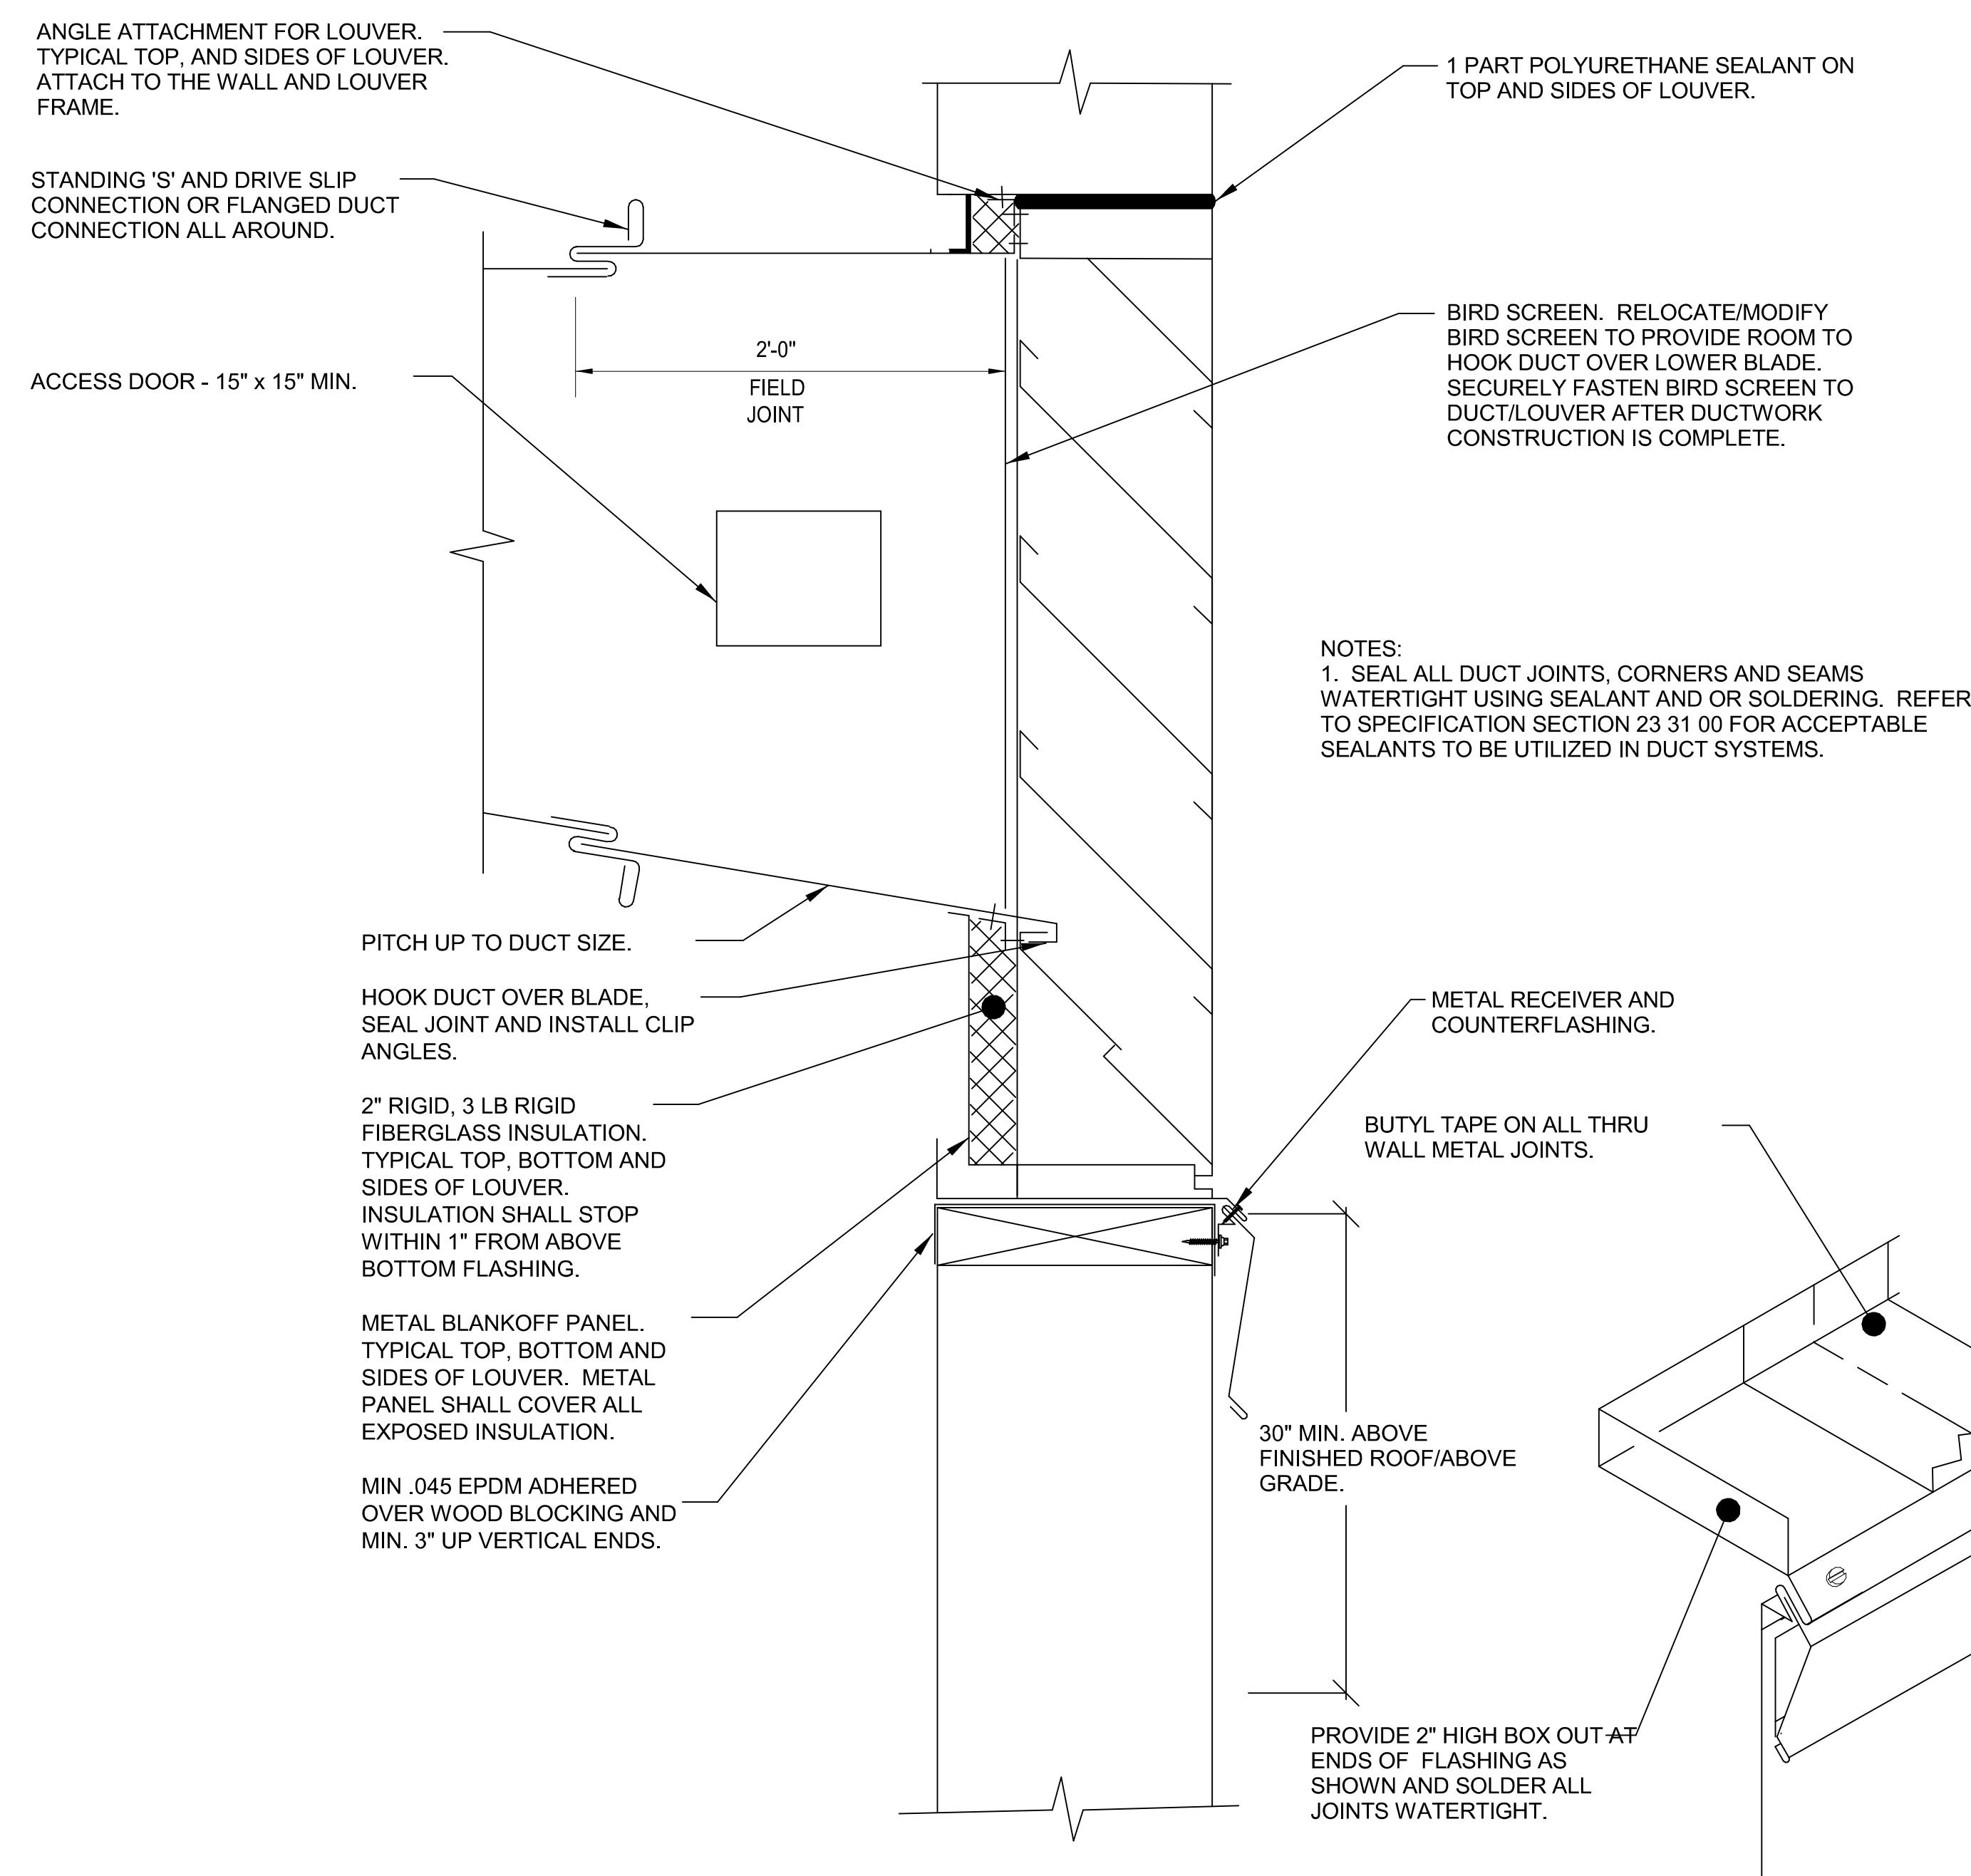

2 DETAIL - LOUVER INSTALLATION

SCALE: NONE

State of Wisconsin
Department of Administration
Division of Facilities Development
Old World Wisconsin Ethnic Outdoor Museum
Town of Eagle, Wisconsin

Tavern Renovations
Old World Wisconsin Ethnic Outdoor Museum
Wisconsin Historical Society
Town of Eagle, Wisconsin
Sheet Title: TAVERN MECHANICAL DETAILS

Revisions:

No.

Date:

Description:

Graphic Scale	See Details
DRF Number	17I1K-04
Set Type	BD
Date Issued	9/8/2023
Sheet Number	M501


KEYED NOTES
ED-1 ALL EXISTING WIRING, SUPPORTS,
AND CONNECTIONS TO BE REMOVED.

ARO EBERLE
ARCHITECTS
433 W. Washington Ave.
Suite 200
Madison, WI 53703
(608) 204-7464
AroEberle.com

Consultant:
DESIGN
ENGINEERS
Architectural Engineers
8801 Prairie View Lane SW, Suite 200
Cedar Rapids, IA 52404
(319) 365-1941
1421 University Street
Middleton, WI 53562 | 608-424-8815
designengineers.com



State of Wisconsin
Department of Administration
Division of Facilities Development

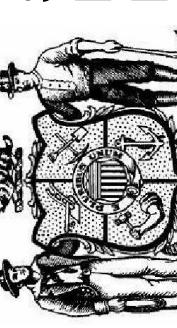





Old World Wisconsin Ethnic Outdoor Museum
Town of Eagle, Wisconsin

Tavern Renovations
Old World Wisconsin Ethnic Outdoor Museum
Wisconsin Historical Society
Town of Eagle, Wisconsin

Sheet Title:
TAVERN ELECTRICAL DEMOLITION PLANS

Revisions:
No. Date Description:

Graphic Scale	See Details
DFD Number	171K-04
Set Type	BD
Date Issued	9/8/2023
Sheet Number	ED110

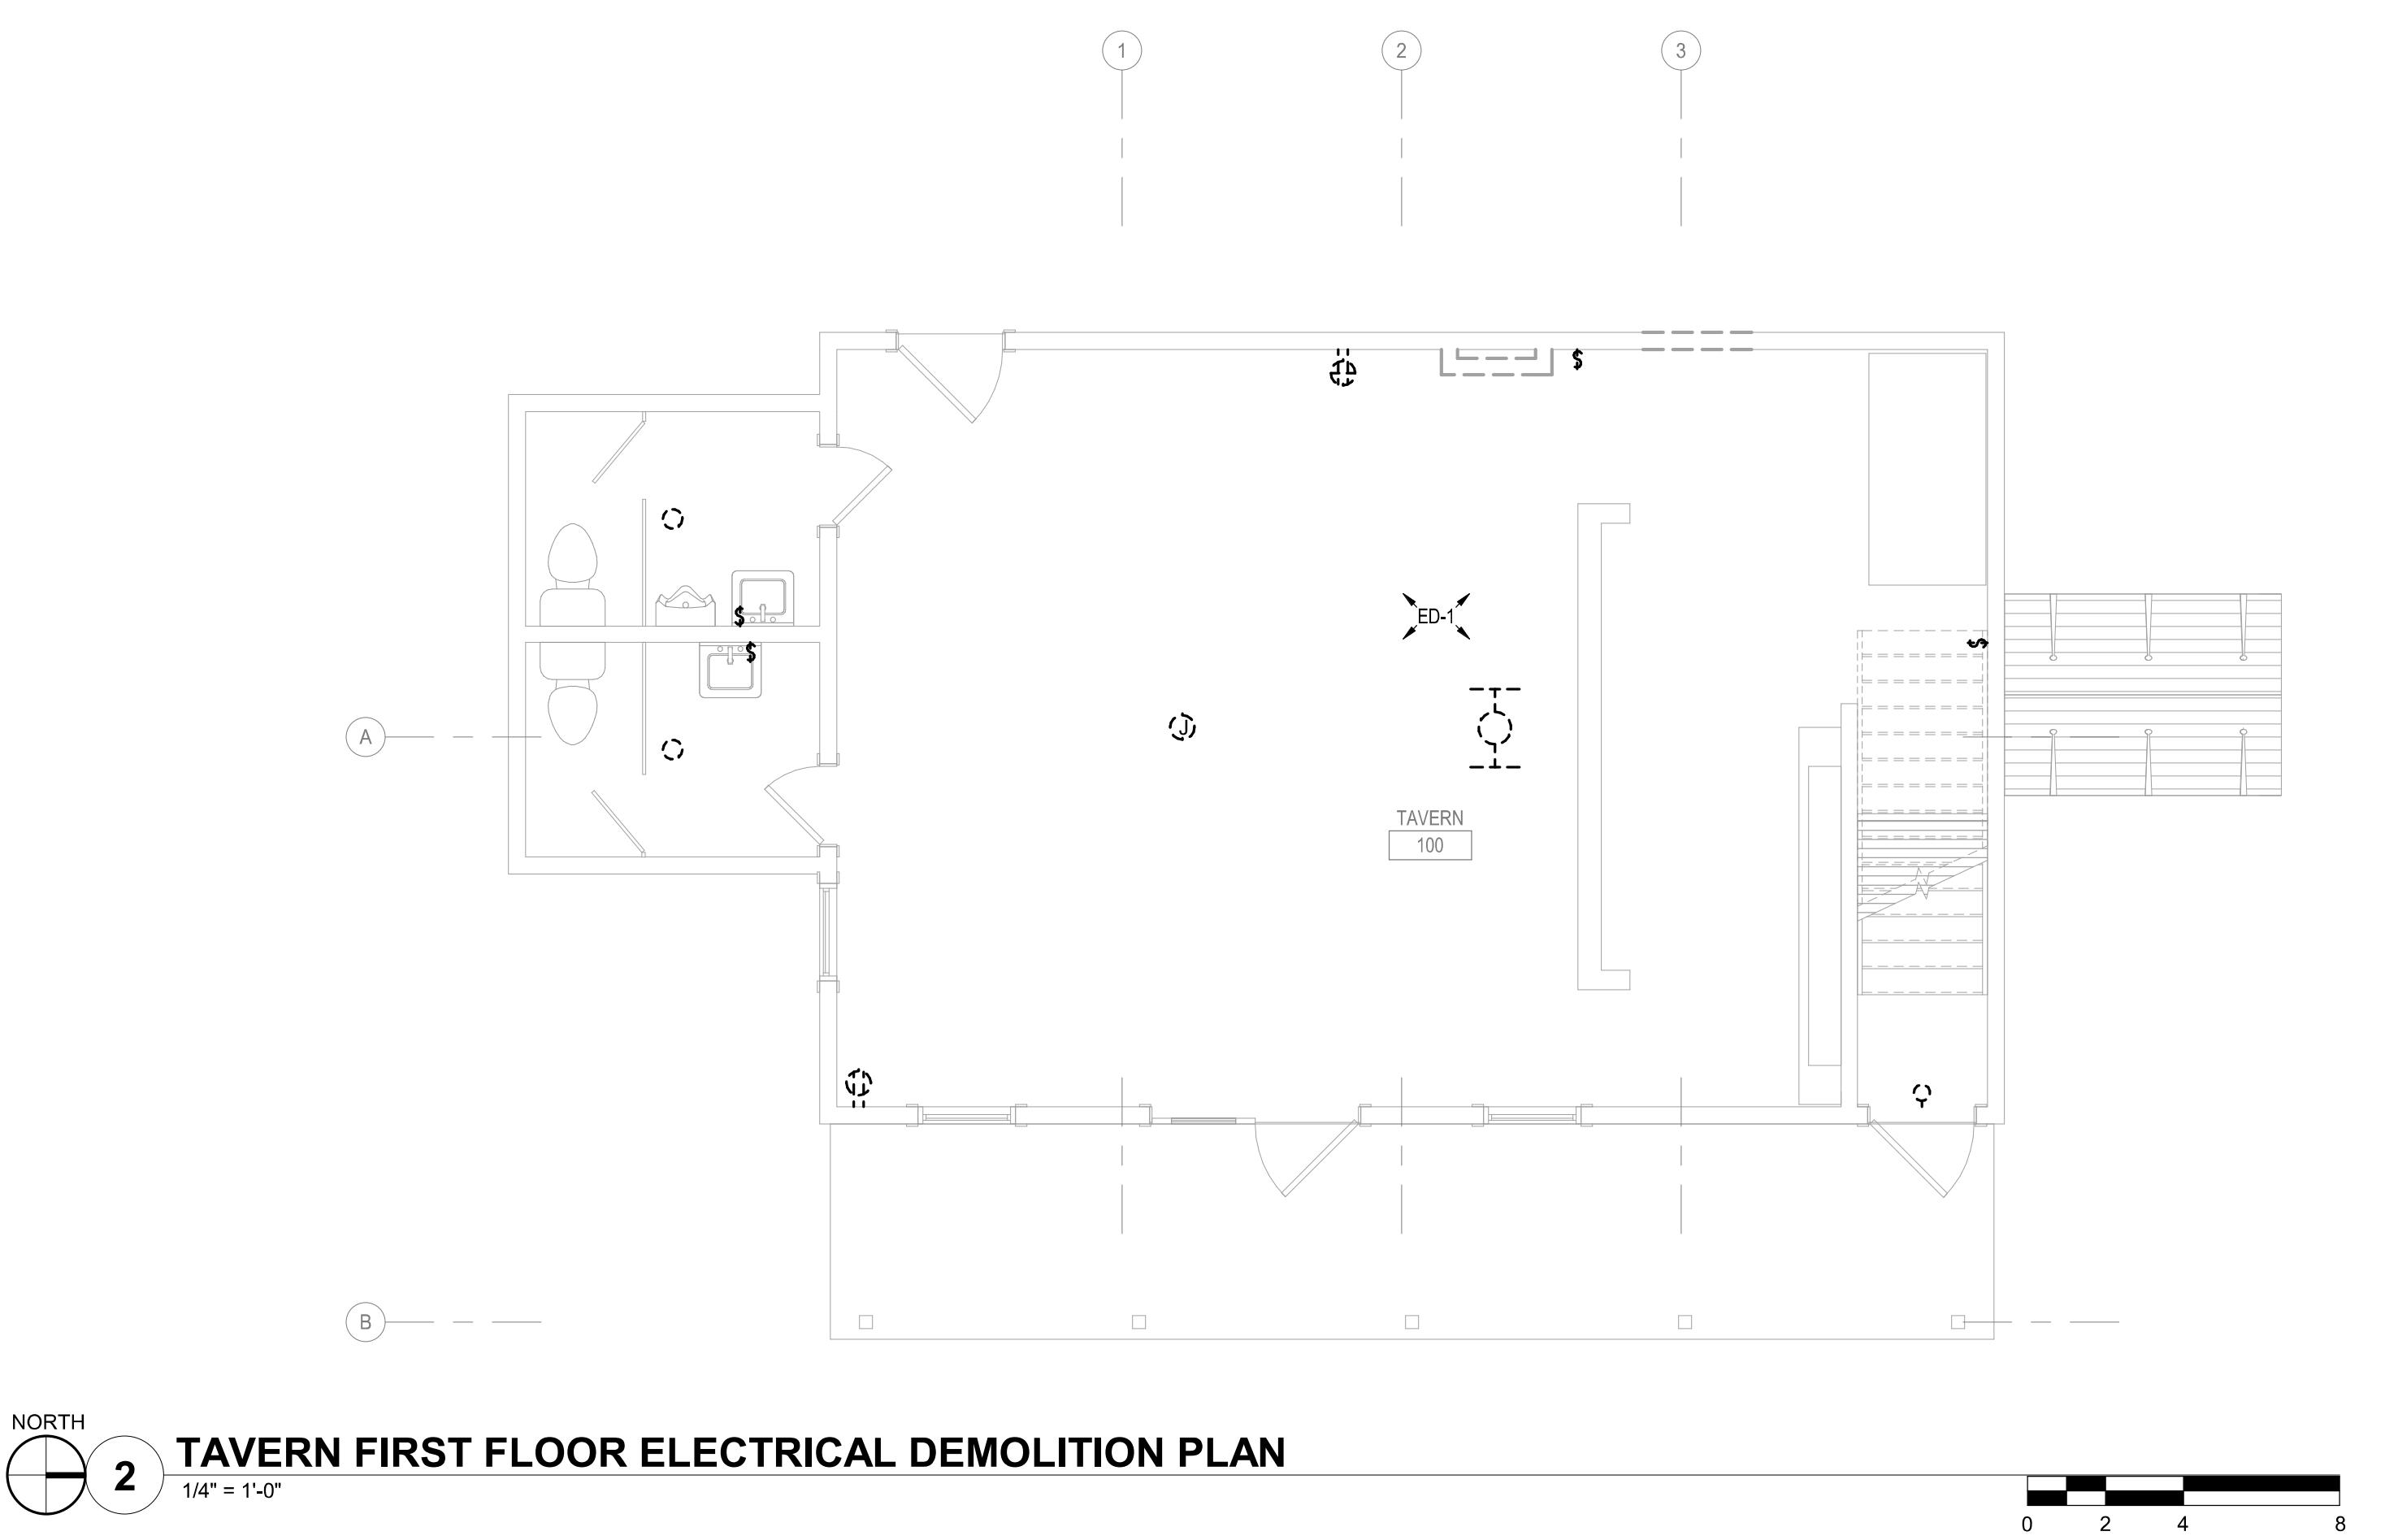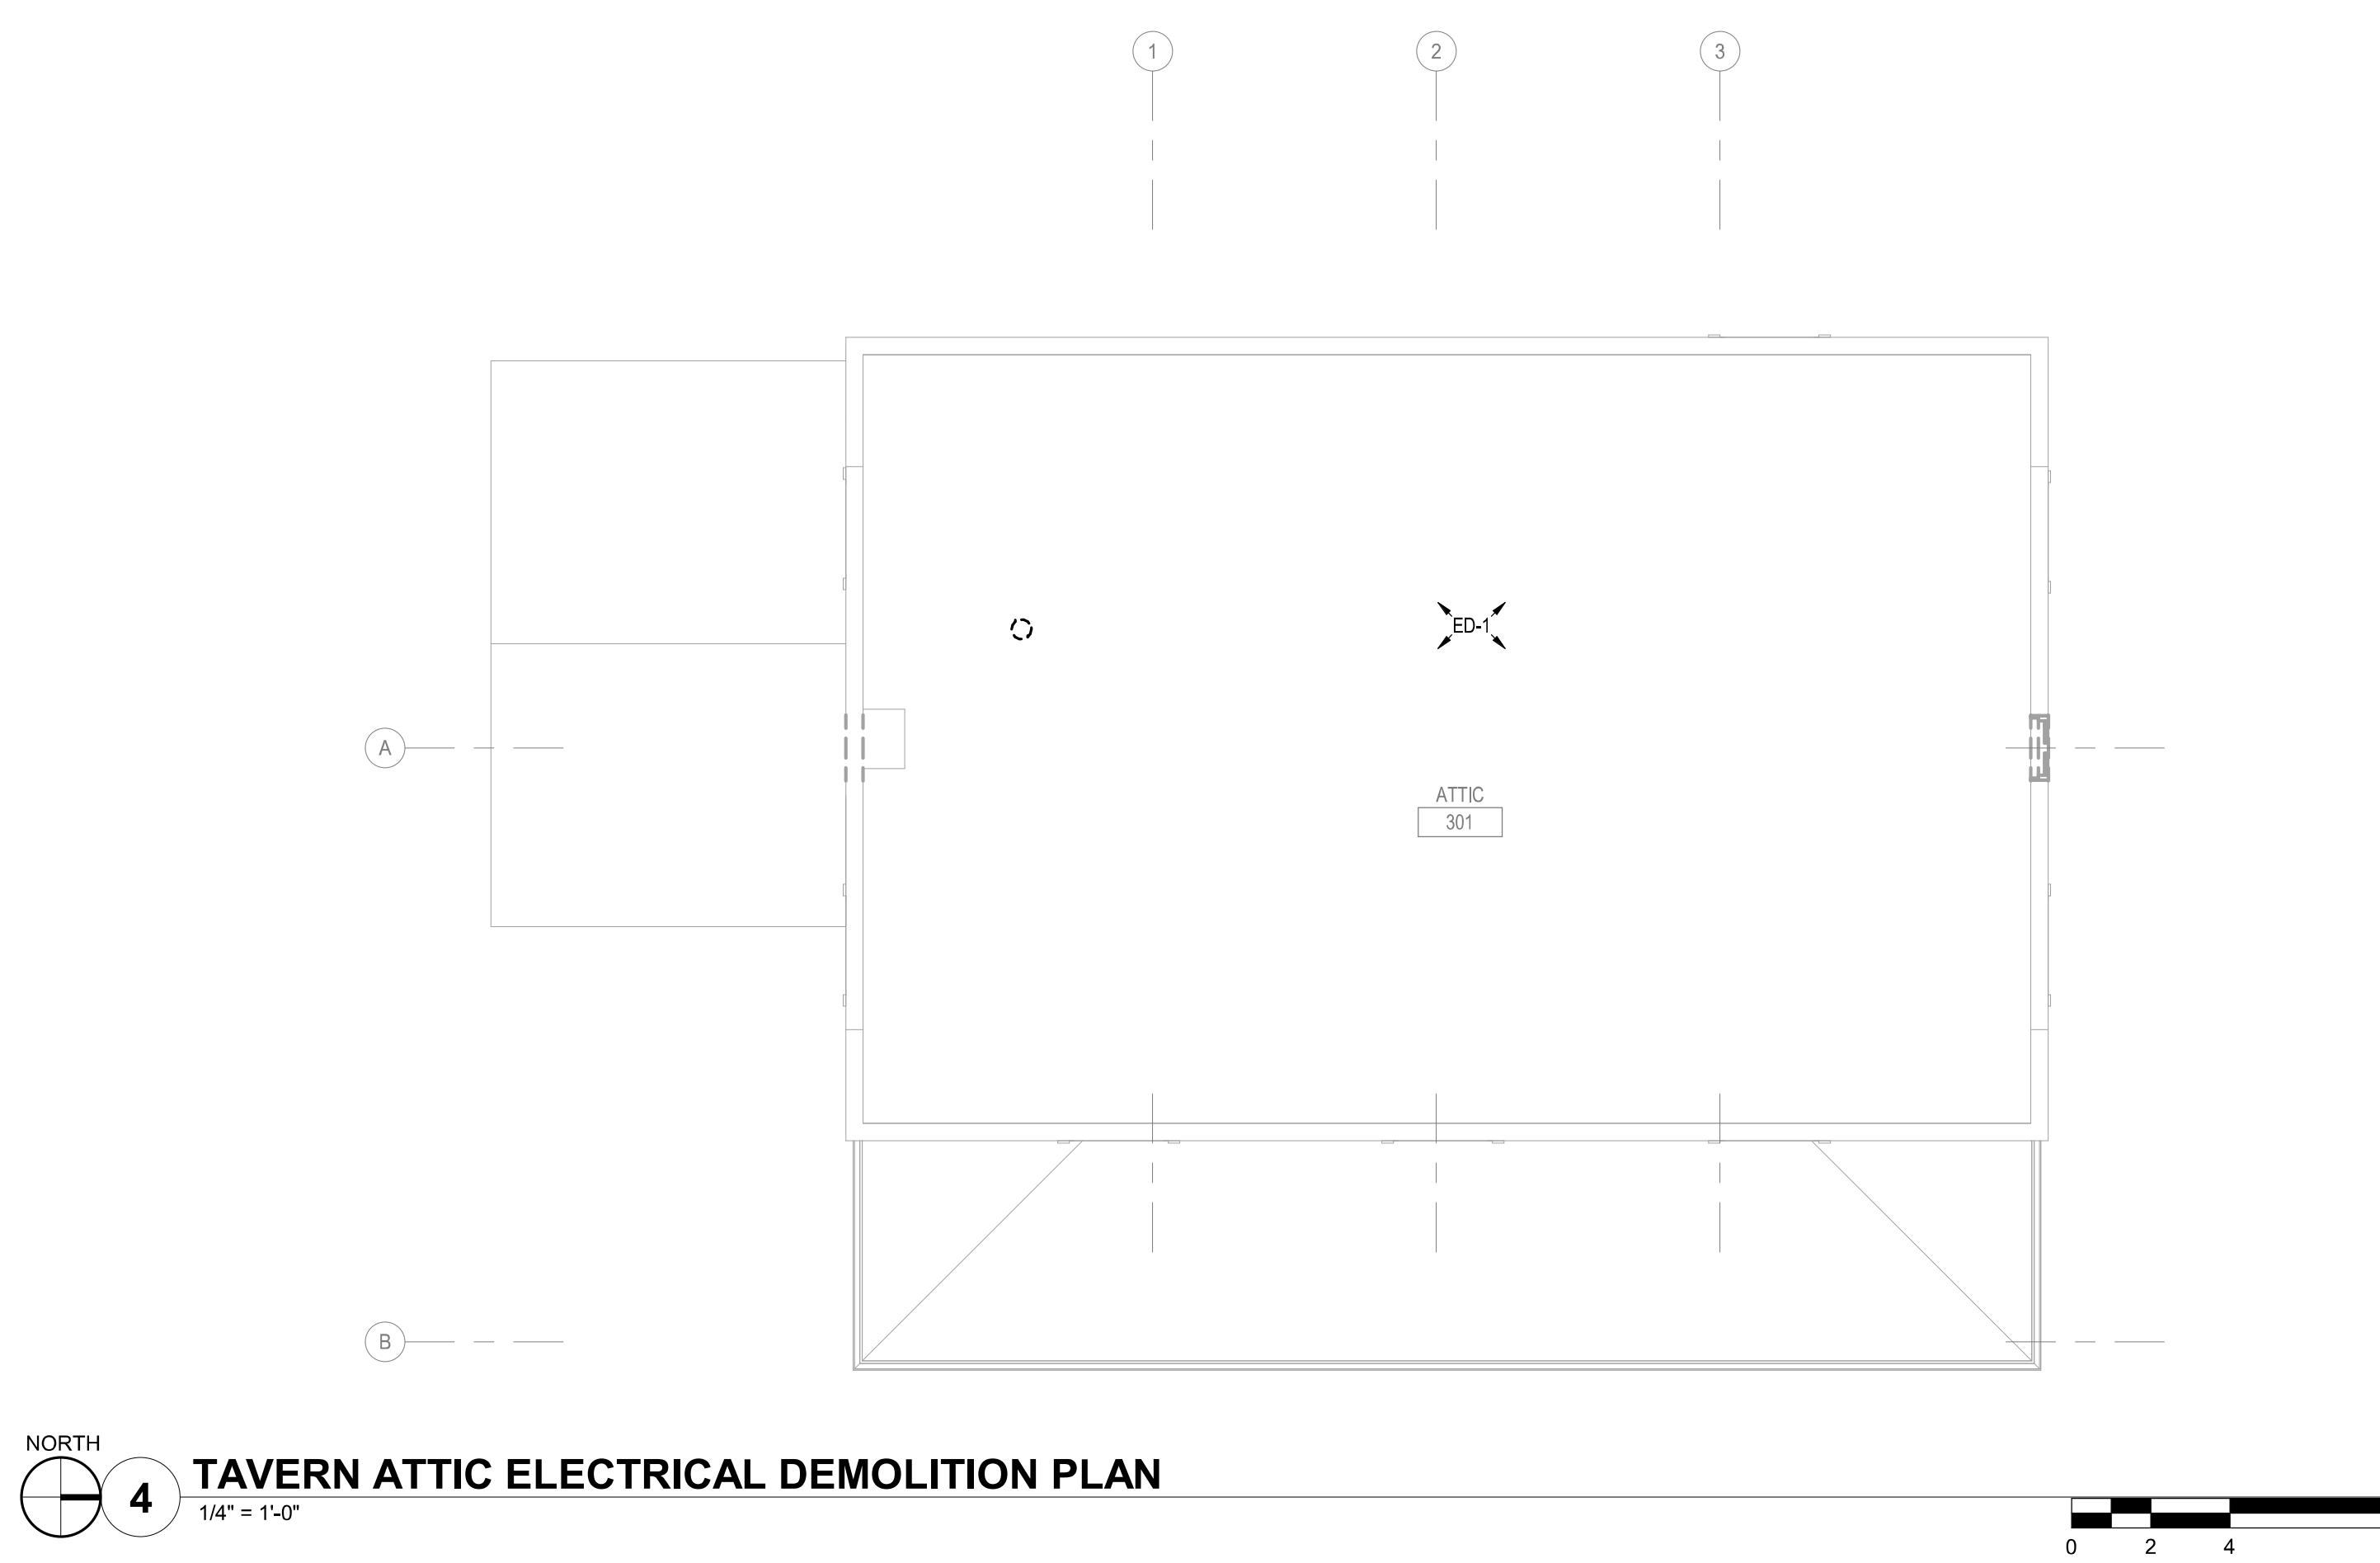
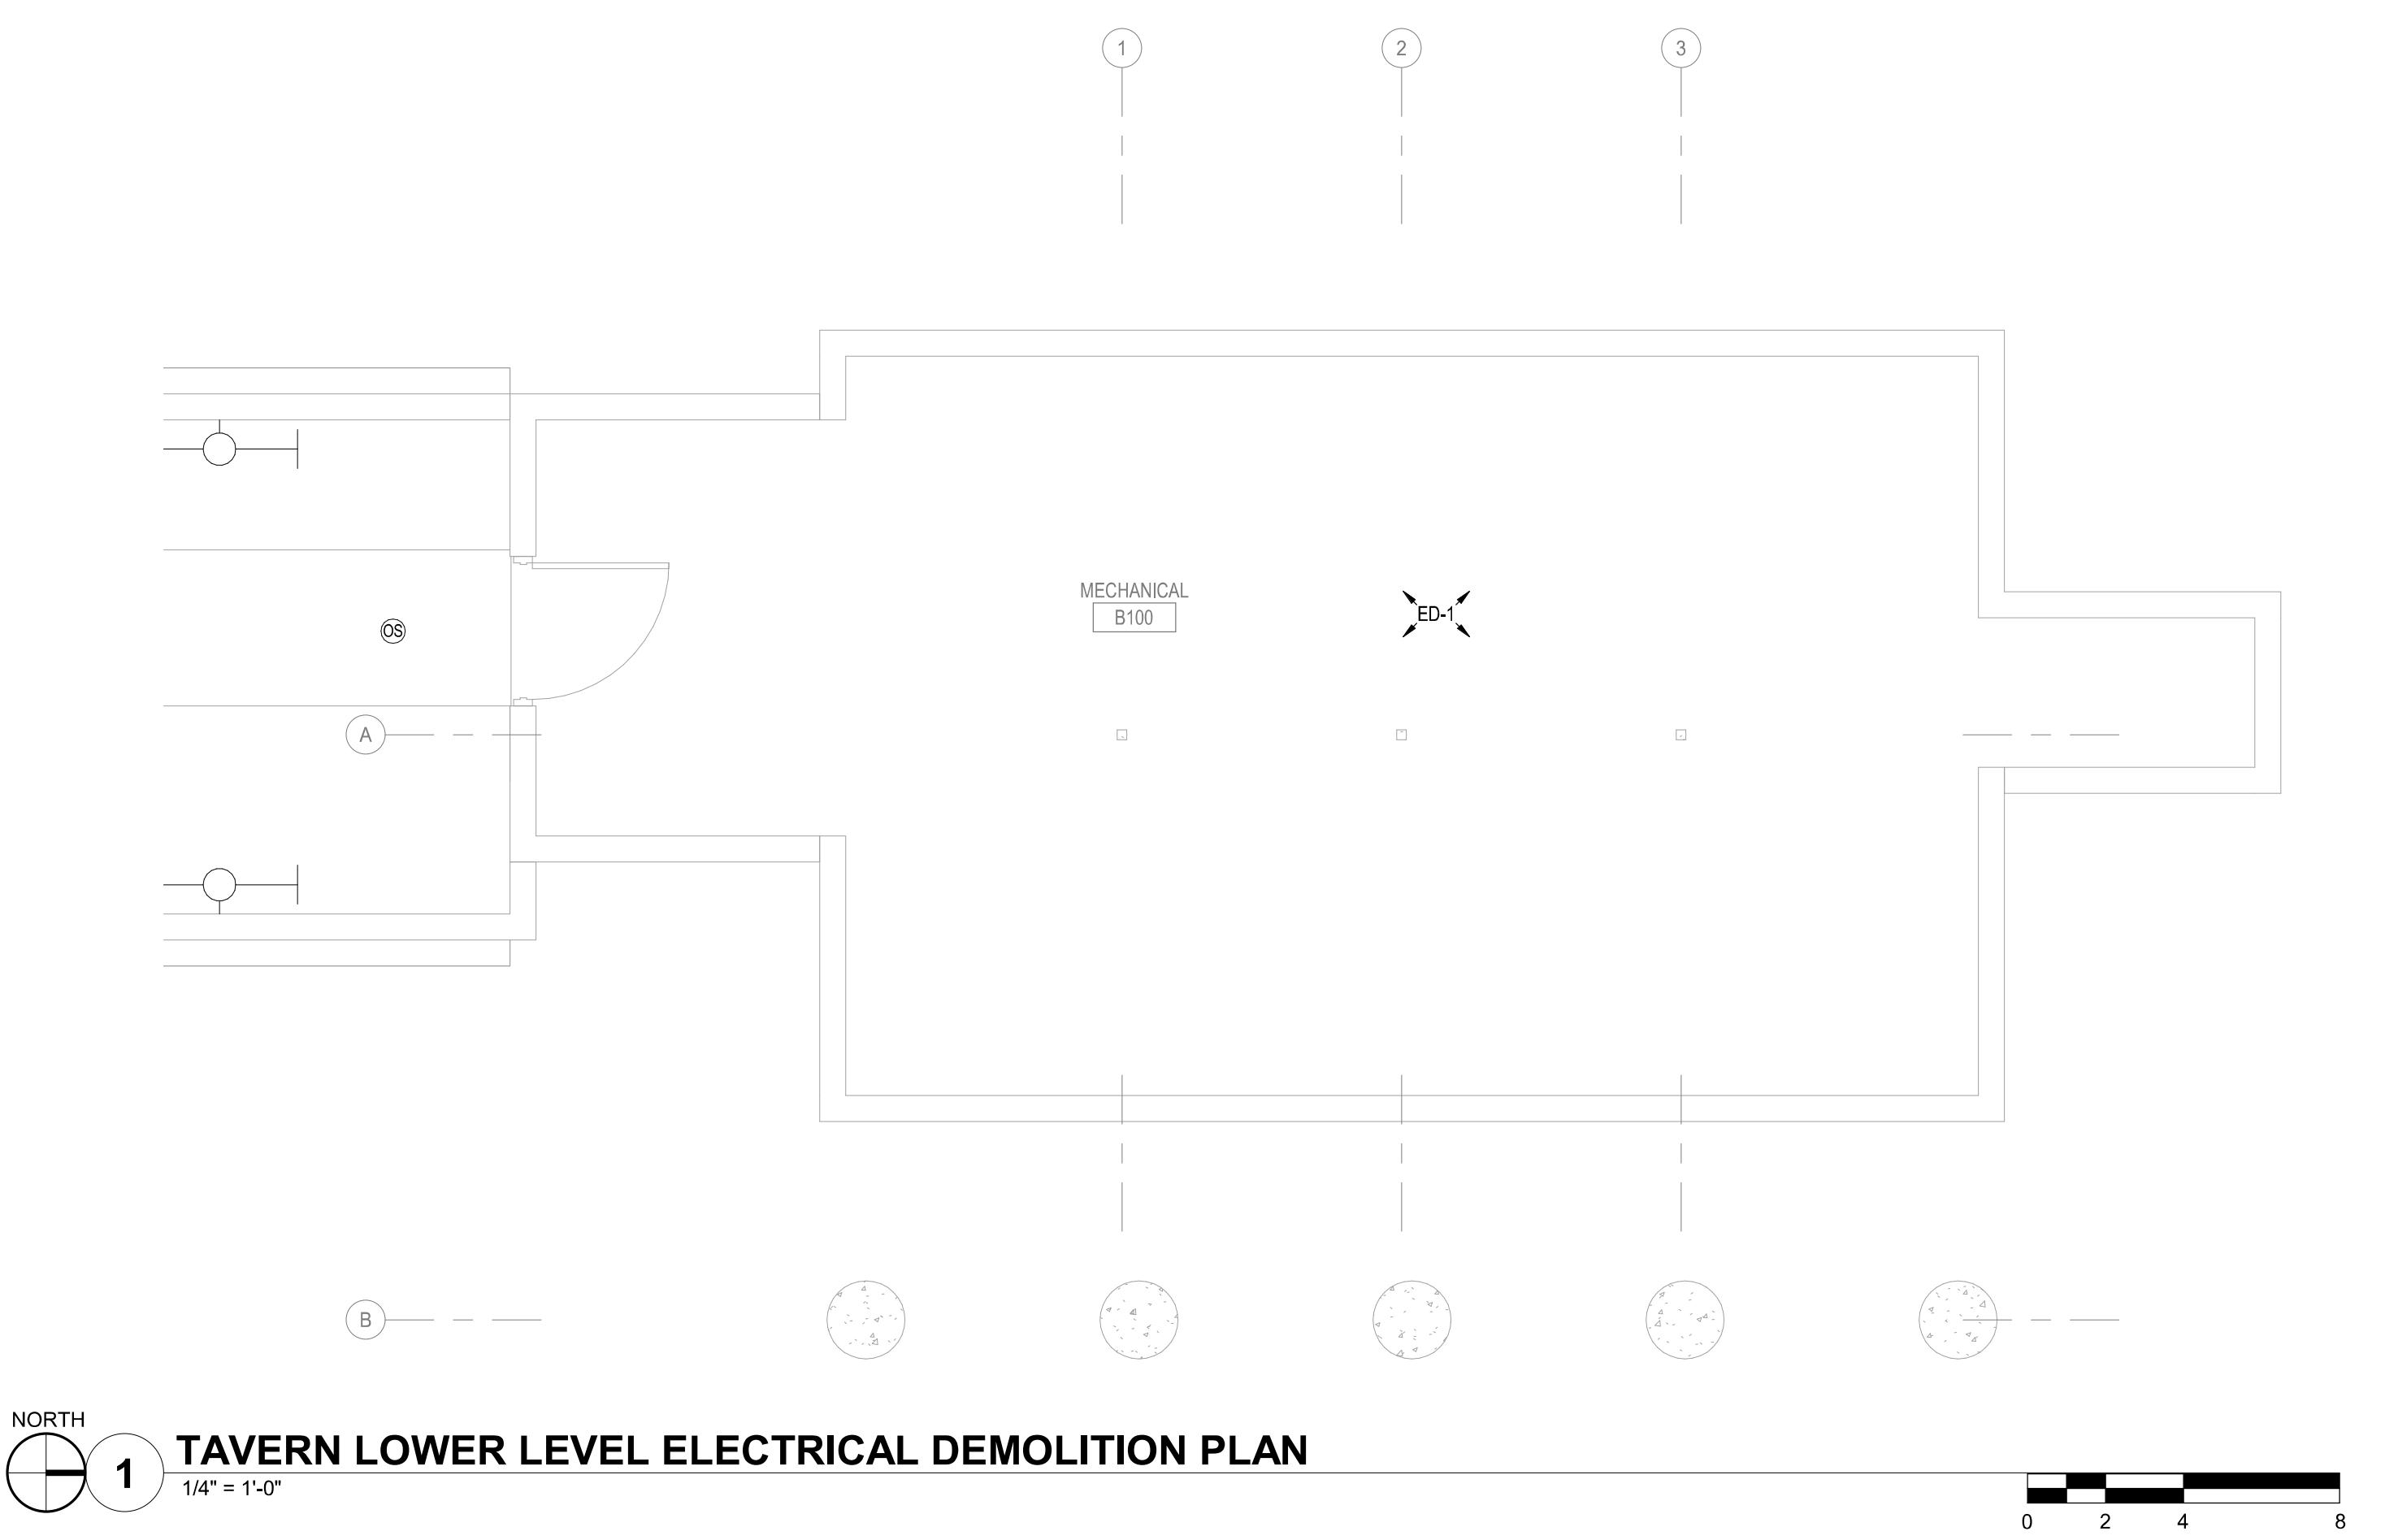
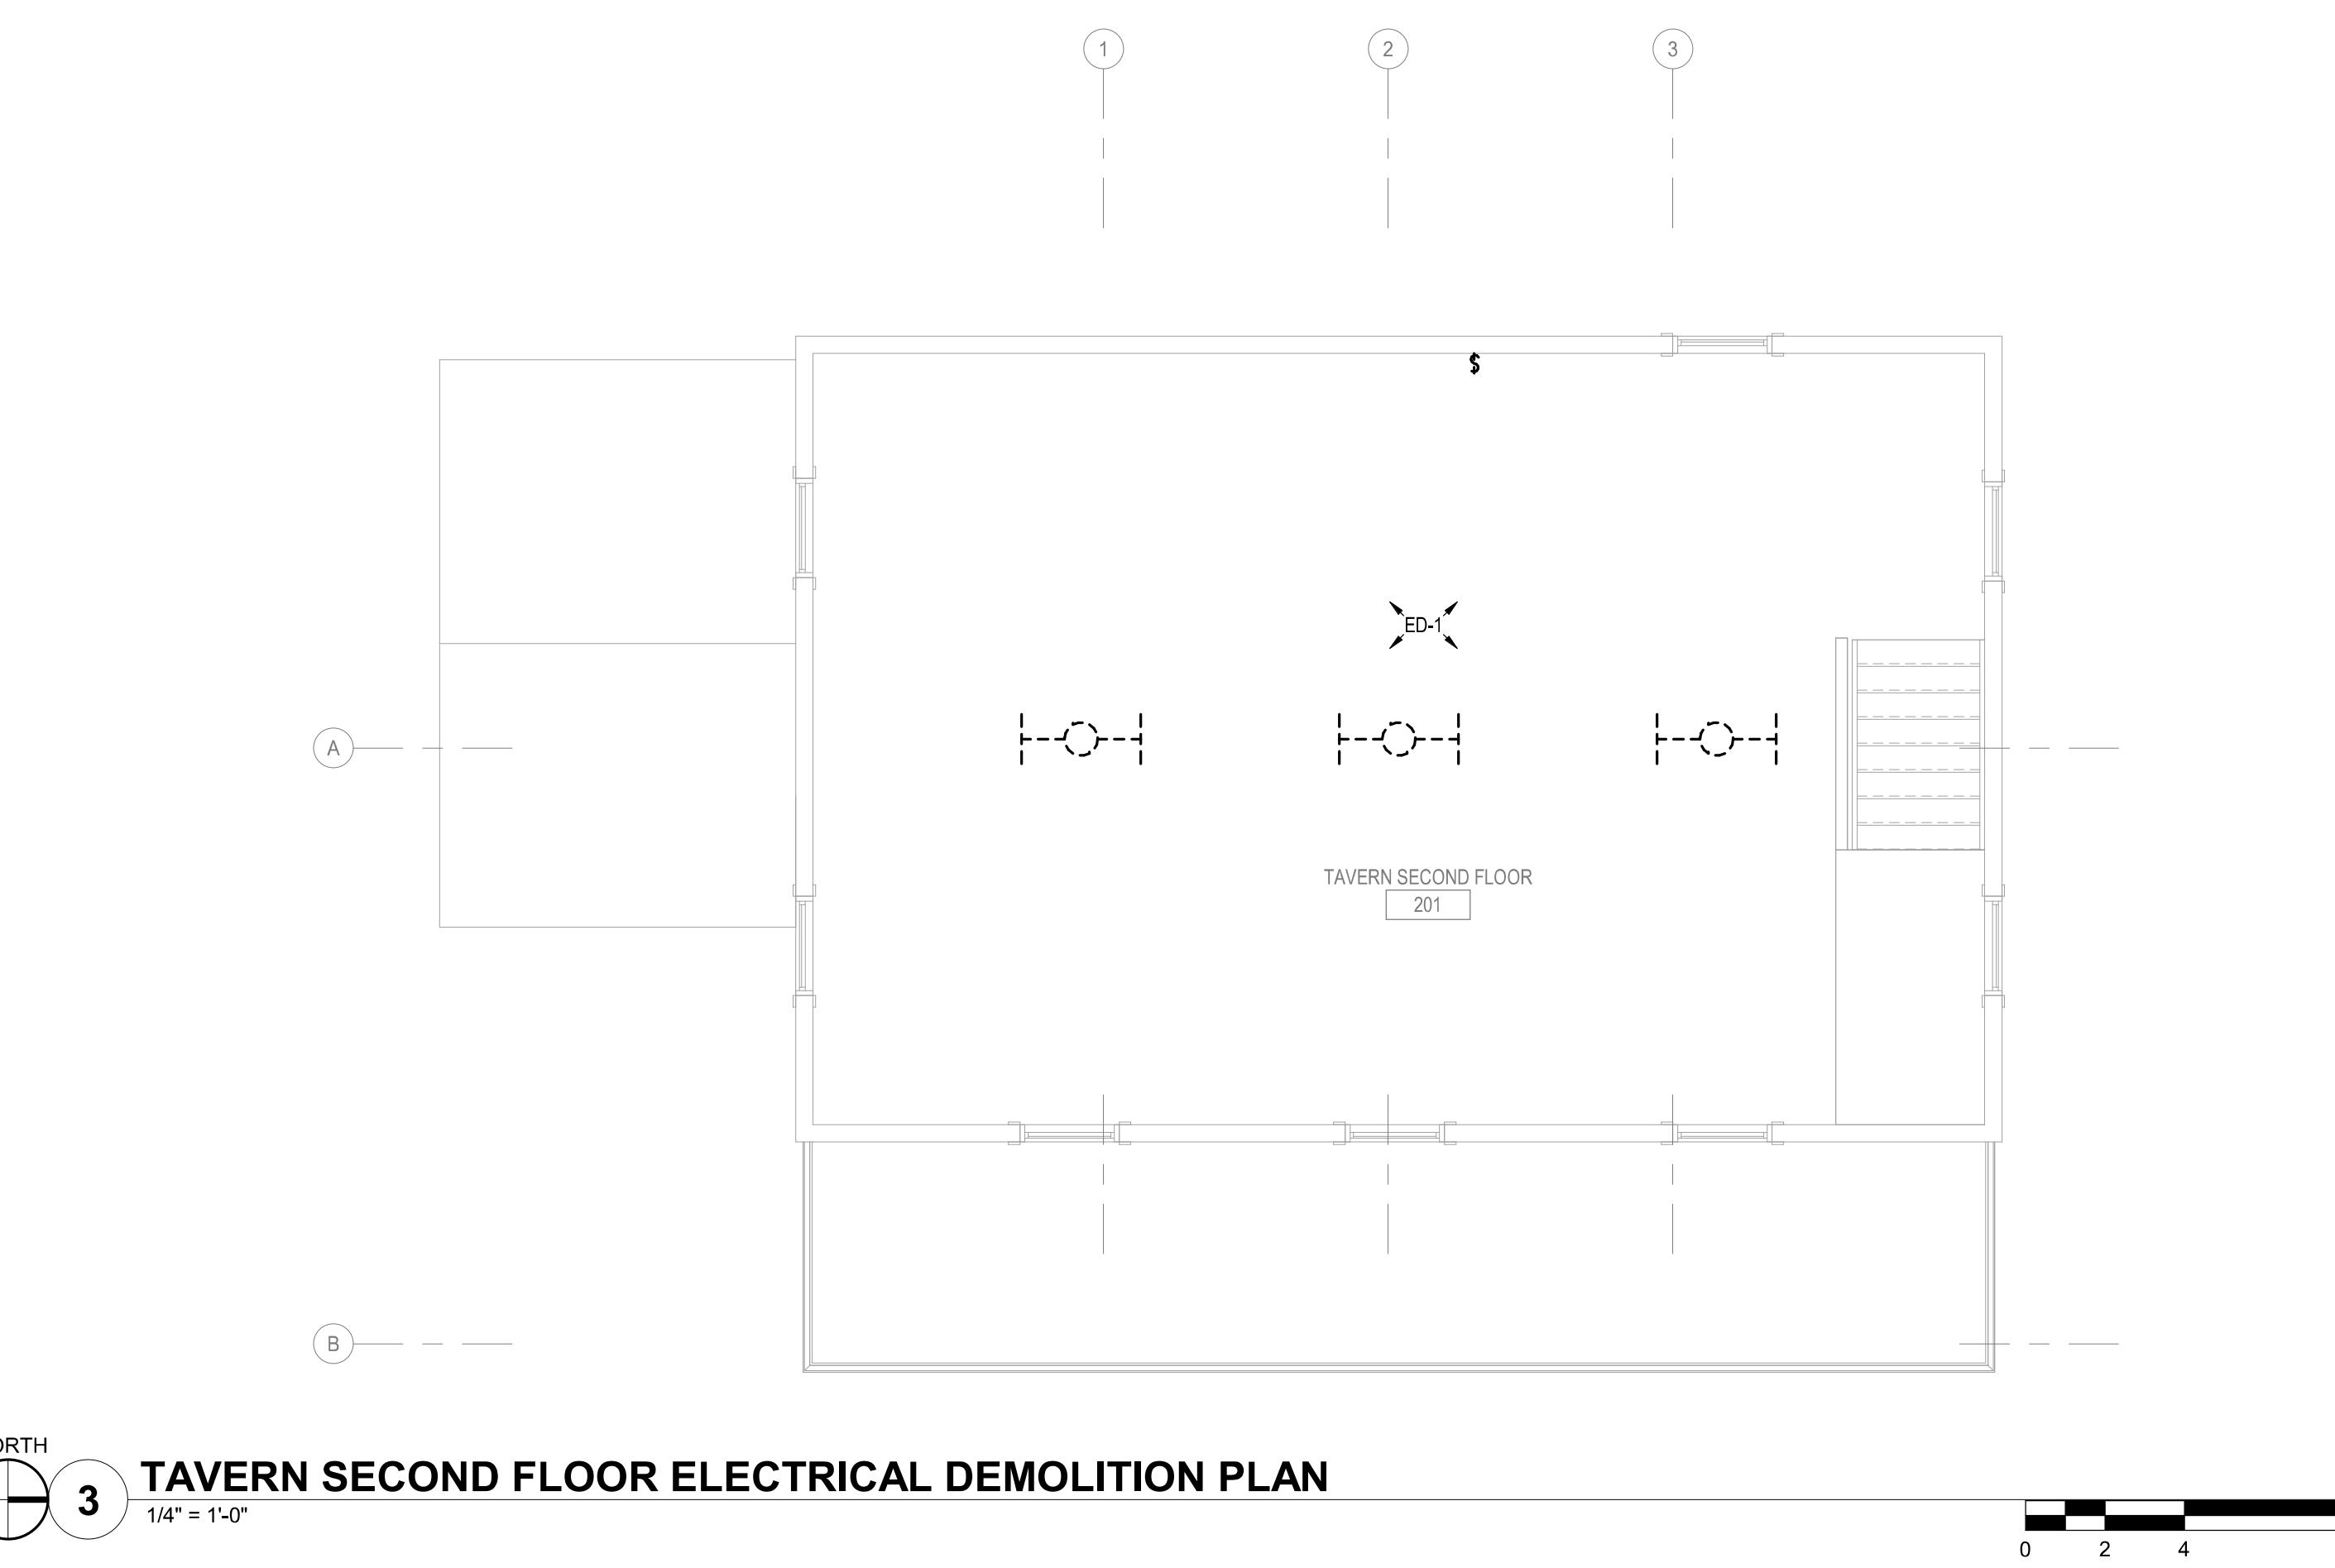


Consultant:

DESIGN
ENGINEERS
Architectural Engineers
8801 Prairie View Lane SW, Suite 200
Cedar Rapids, IA 52404 | 888.1944.1944
4215 University Avenue | Suite 300
Madison, WI 53705 | 608.424.8815
designengineers.com



KEYED NOTES	
E3	PROVIDE 100A-3PH FEED TO EXISTING BREWERY PANEL LL-1A. PROVIDE 100/3 POLE BREAKER TO MATCH EXISTING EATON 359AC BIMINI BREAKER IN EXISTING PANEL, BOX CAT E23048R. JOB NO. SMK1194813-002. MFGD AT JRZ. REMOVE SPARE BREAKERS 37, 38&41 IF NOT USED. HIDE AS NECESSARY.
E4	COORDINATE ALL WALK-IN FREEZER/COOLER WIRING, CONDUIT, CONNECTION REQUIREMENTS AND PENETRATIONS WITH EQUIPMENT PROVIDER AND MANUFACTURER AS NECESSARY.
E5	PROVIDE (1) GND OUTLET TO SERVE TELECOM DC1 RACK WITH (2) CIRCUITS. COORDINATE FINAL MOUNTING LOCATION WITH DIVISION 27.

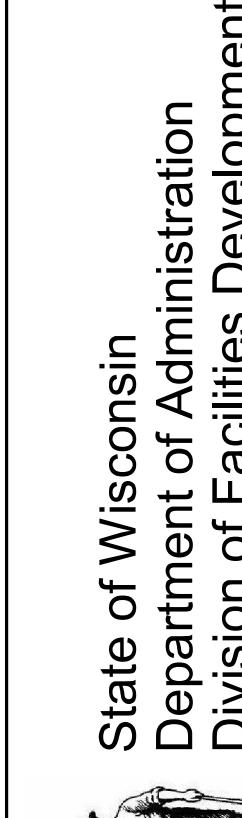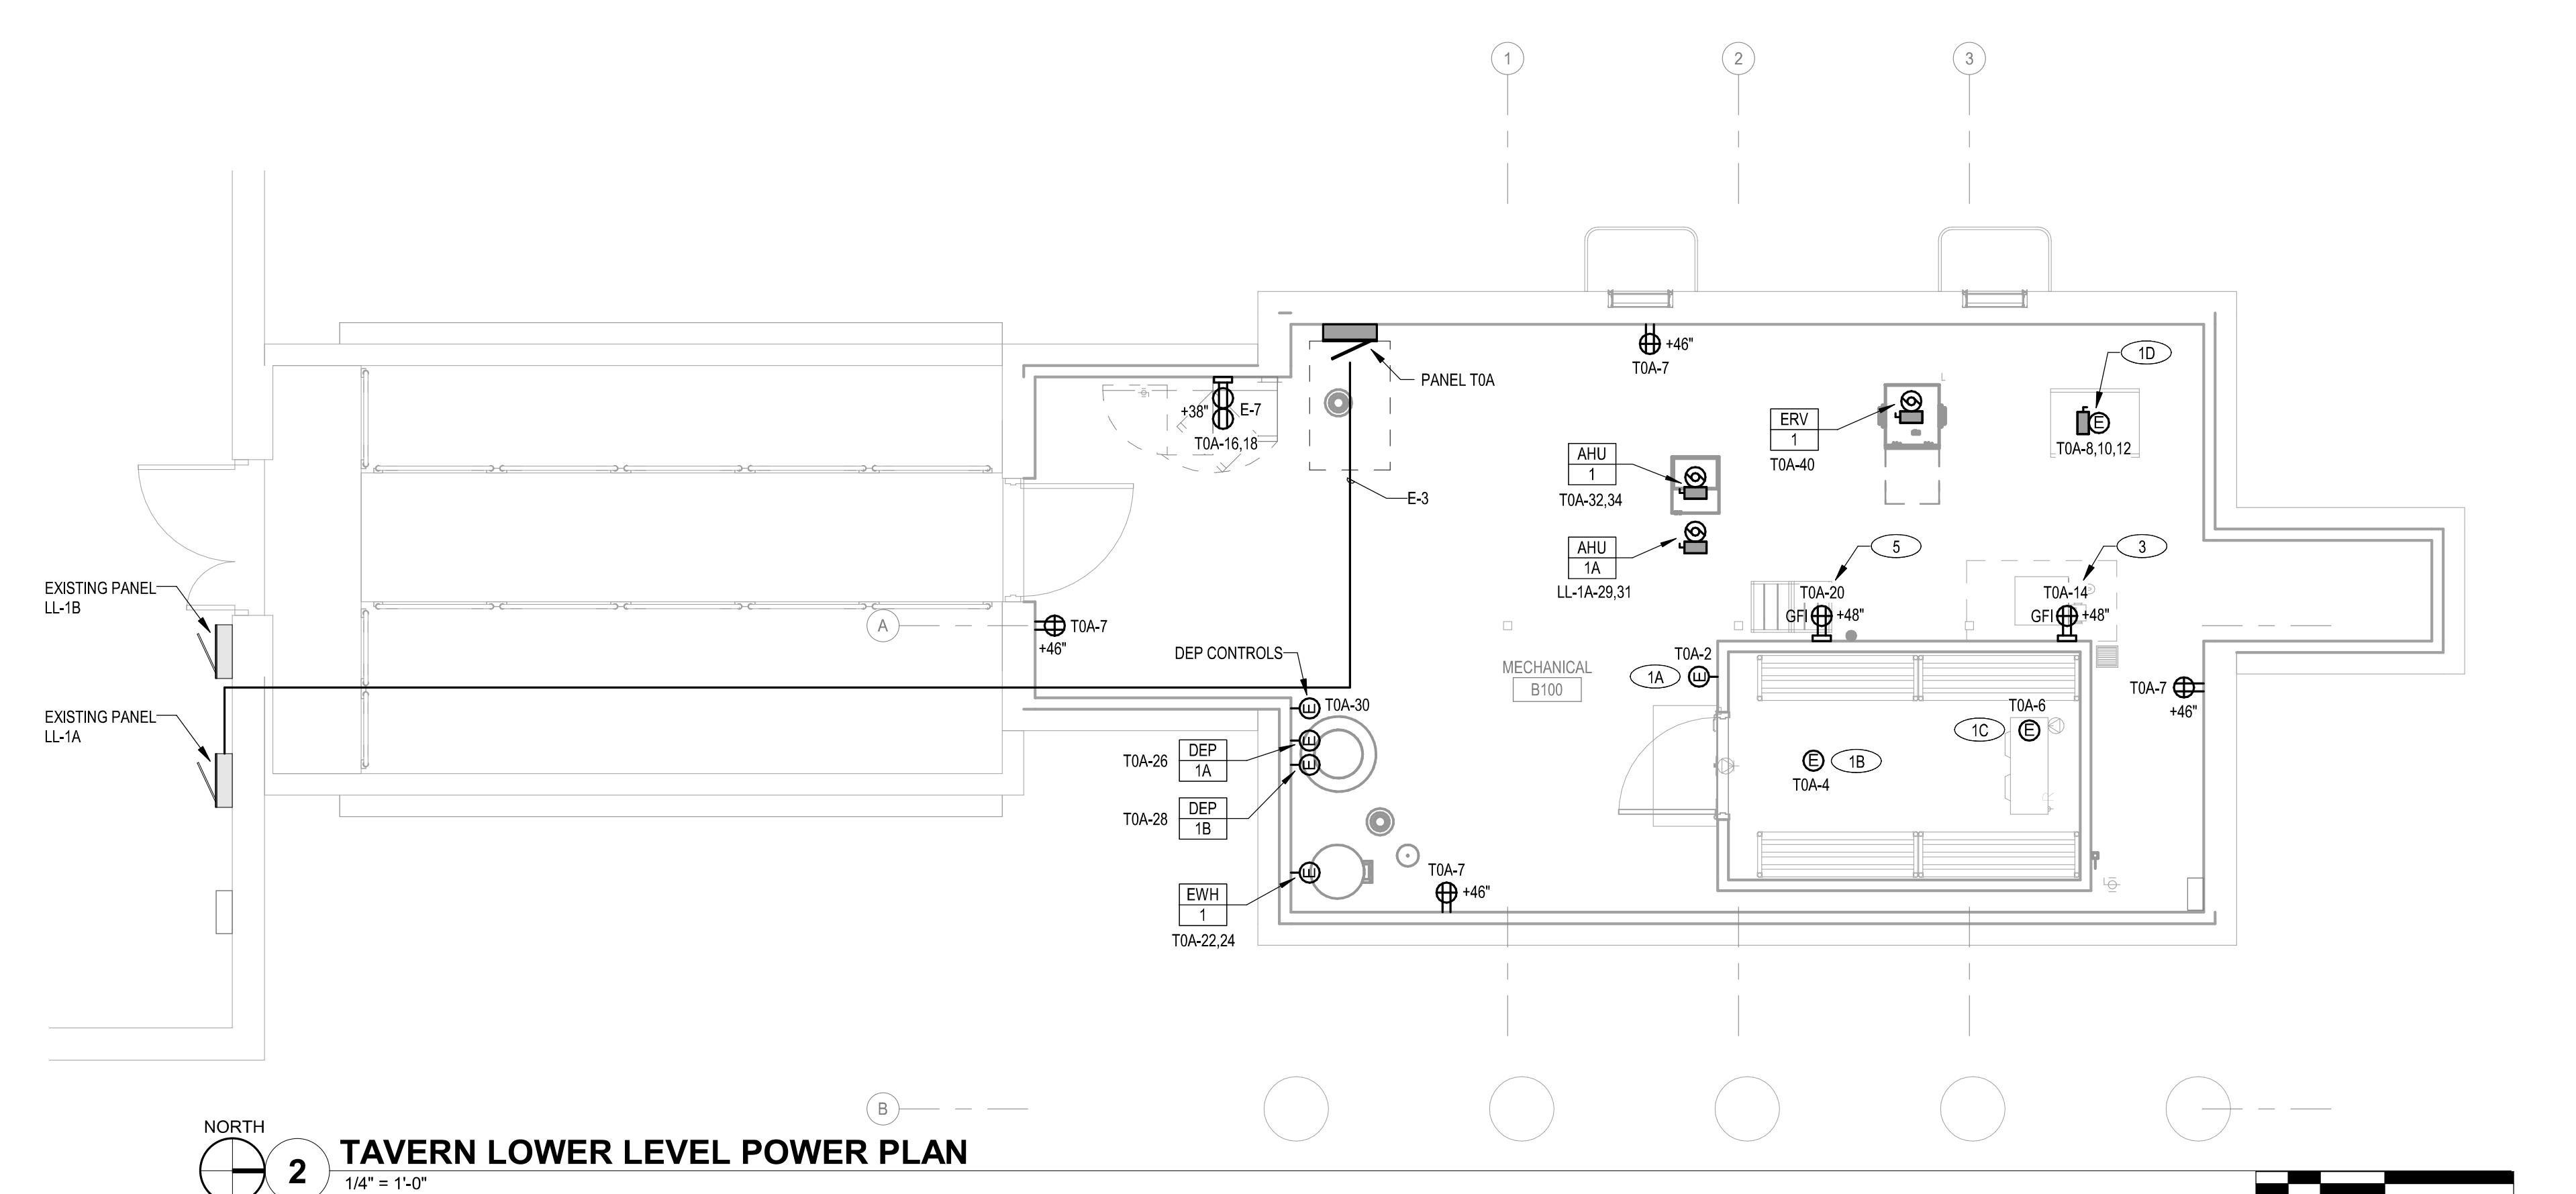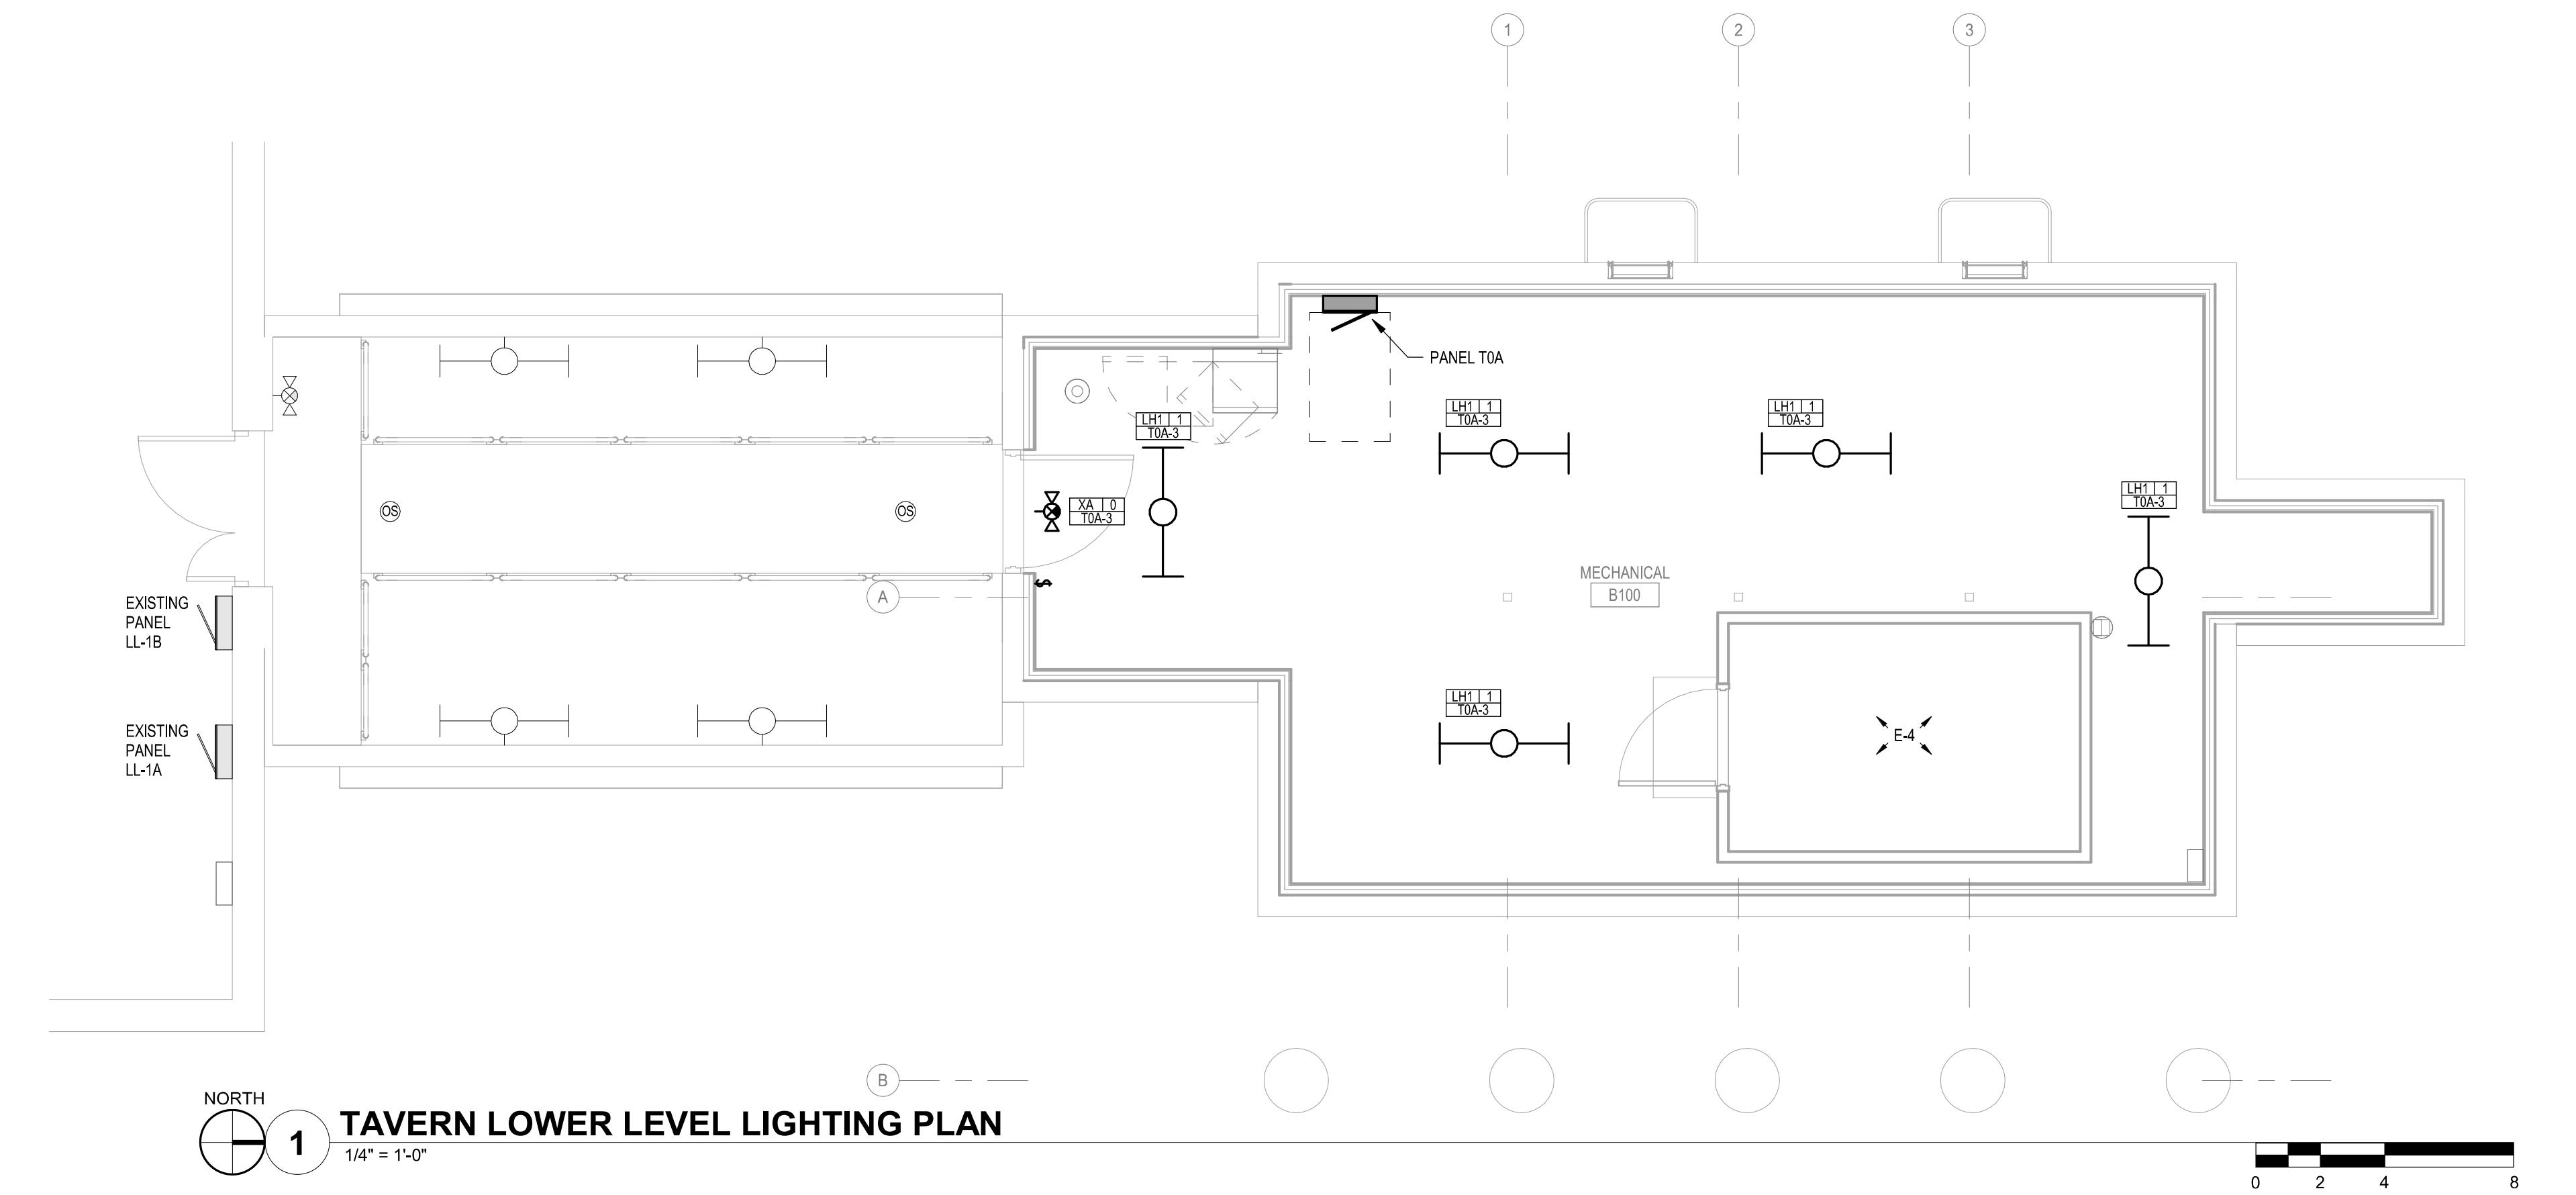

State of Wisconsin
Department of Administration
Division of Facilities Development

Tavern Renovations
Old World Wisconsin Ethnic Outdoor Museum
Wisconsin Historical Society
Town of Eagle, Wisconsin

Sheet Title:
TAVERN LOWER LEVEL ELECTRICAL PLANS

E110

Revisions:

No. Date: Description:

Graphic Scale

See Details

DFD Number

1711K-04

Set Type

BD




Date Issued

9/8/2023

Sheet Number

NEW WORK KEY	
—	EXISTING
—	NEW / REVISED
■	EXISTING EQUIPMENT
■	NEW / REVISED EQUIPMENT

9/8/2023 1:11:45 PM

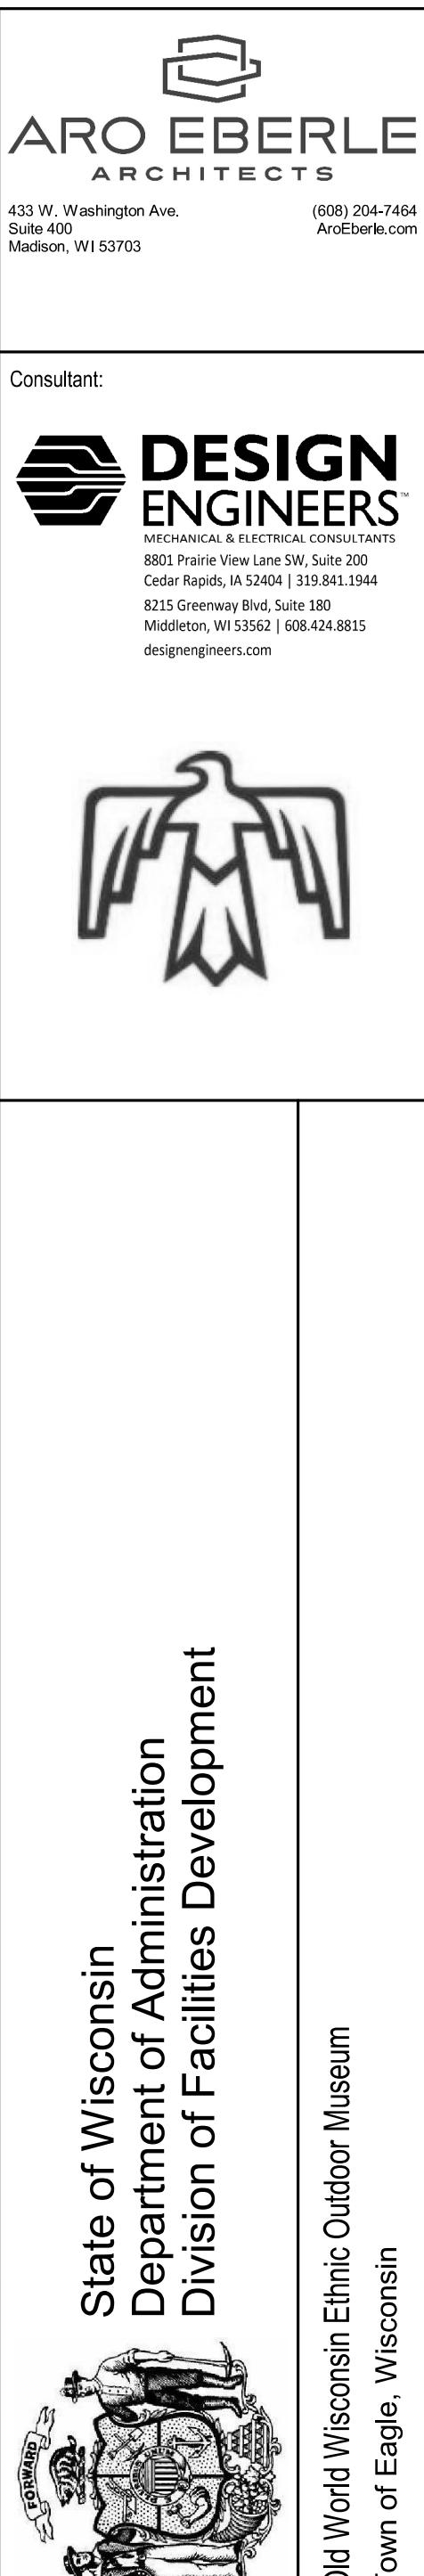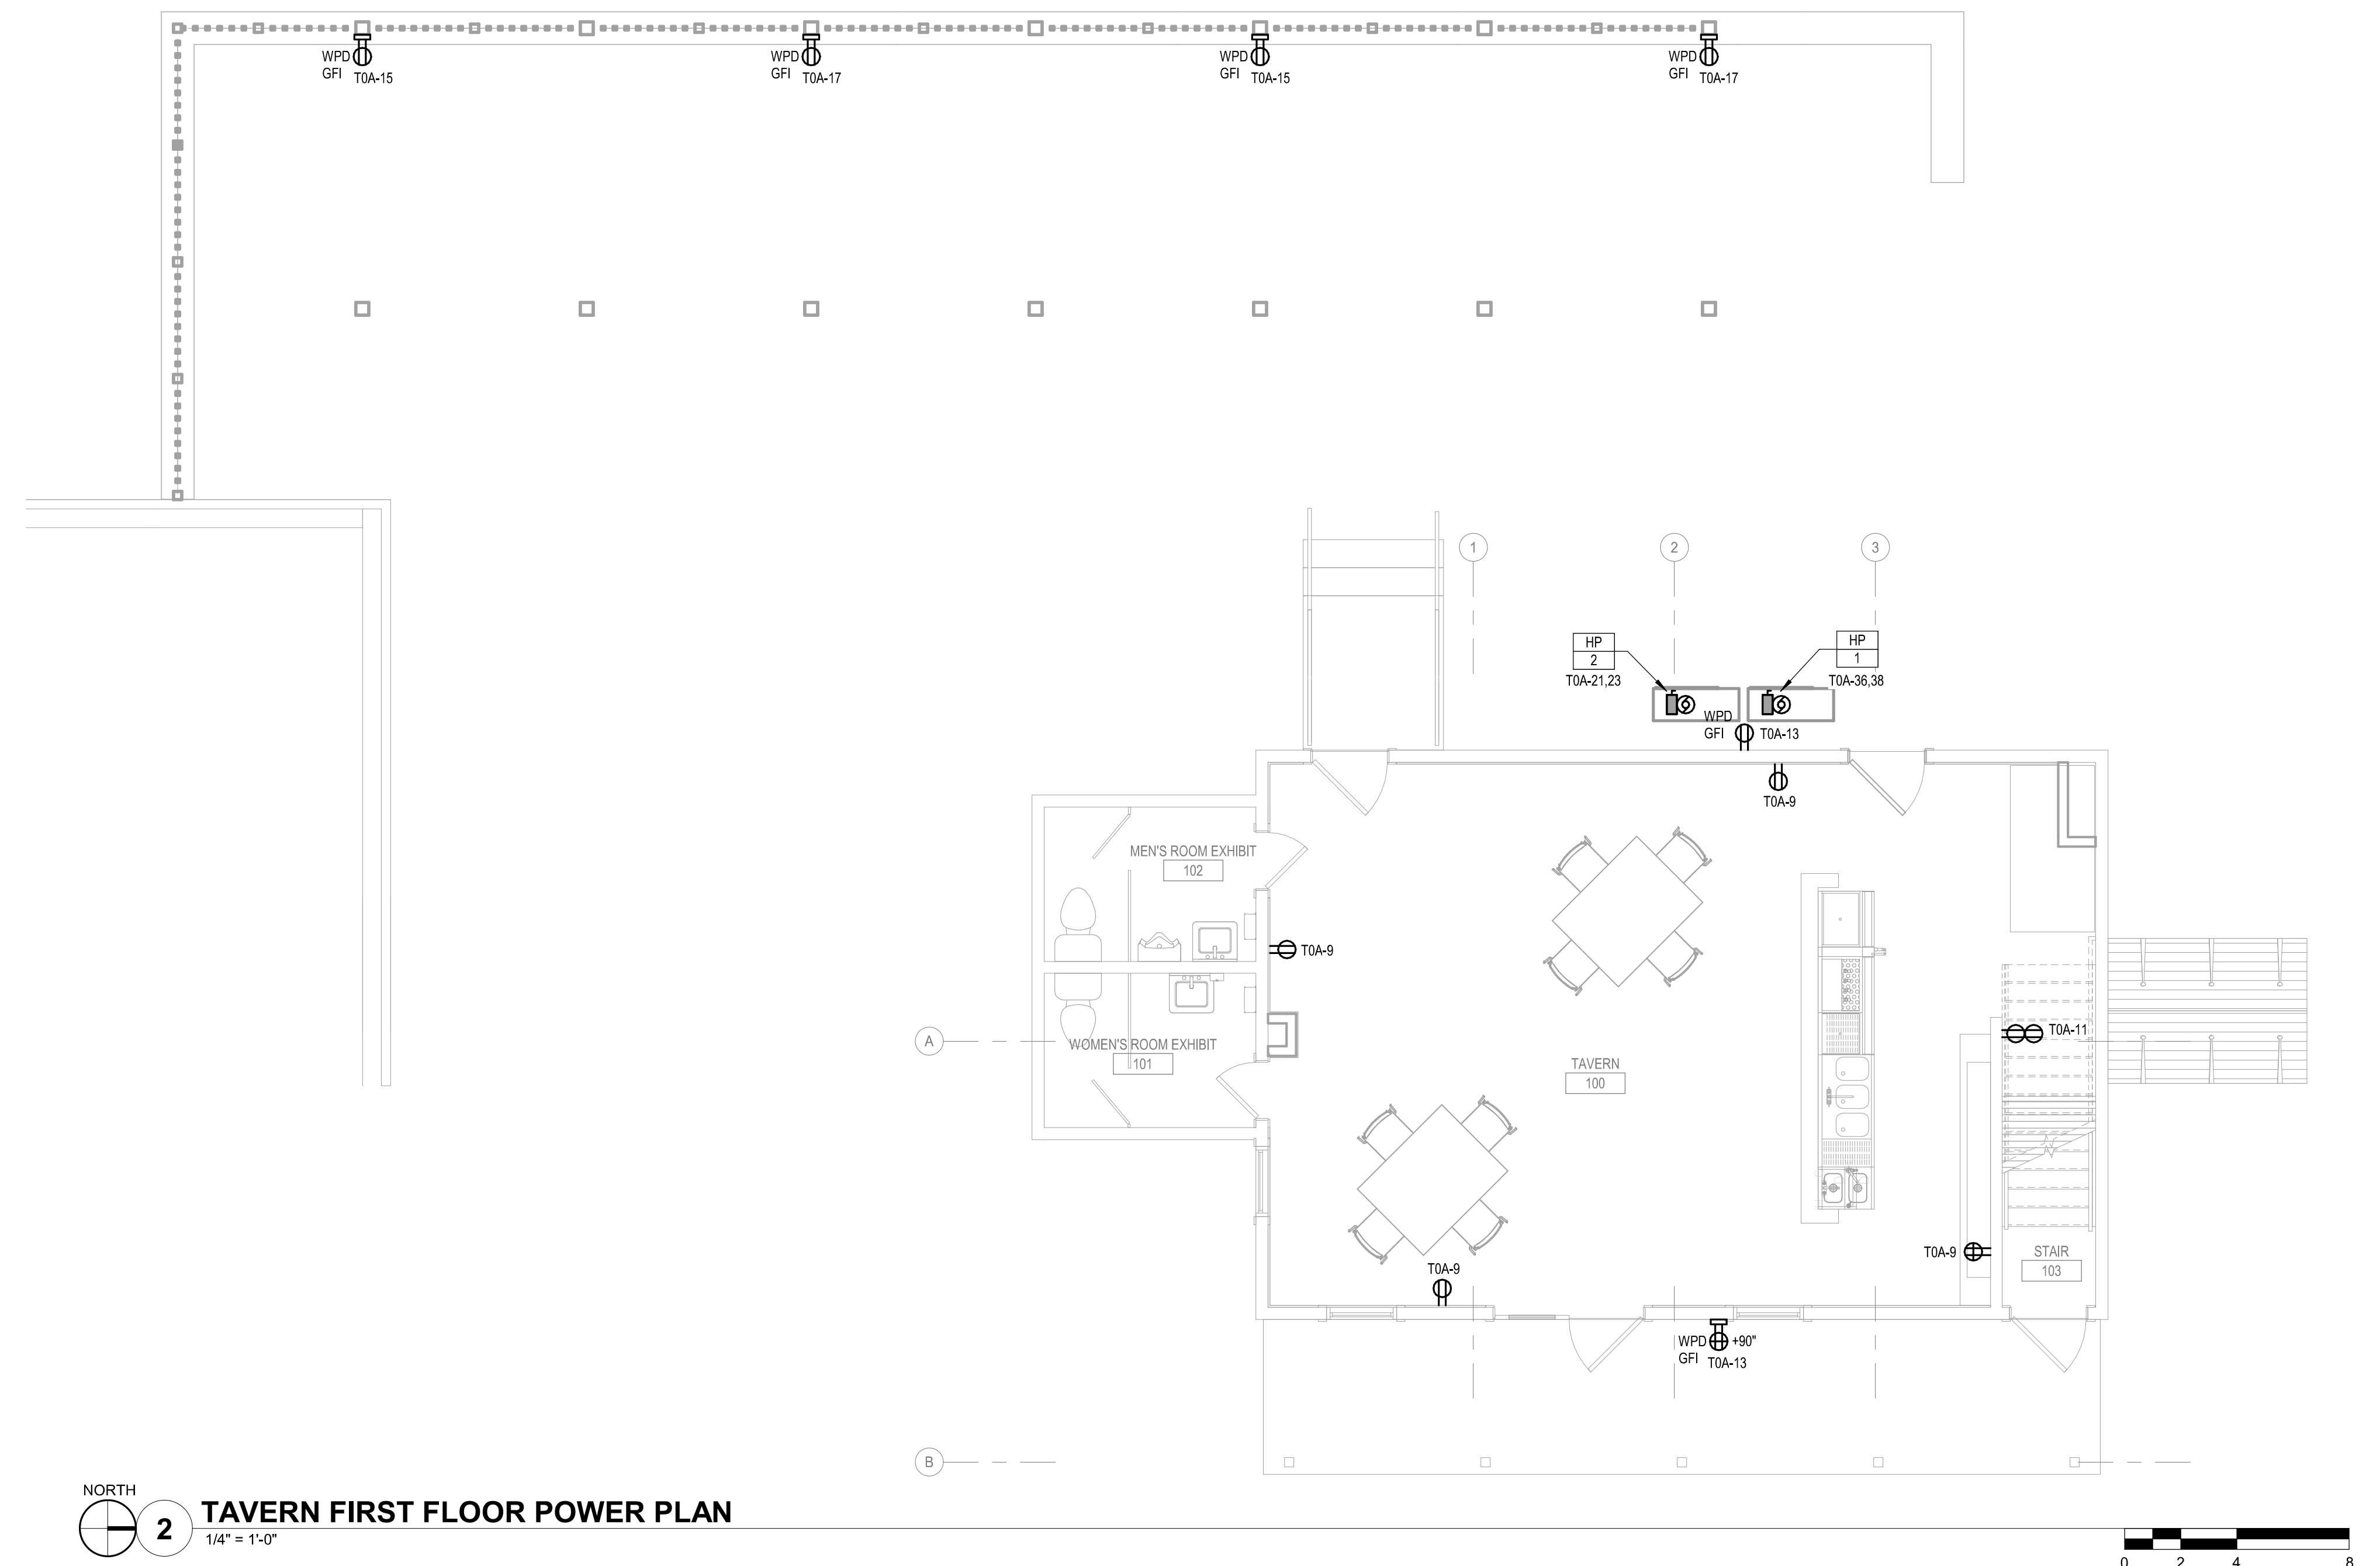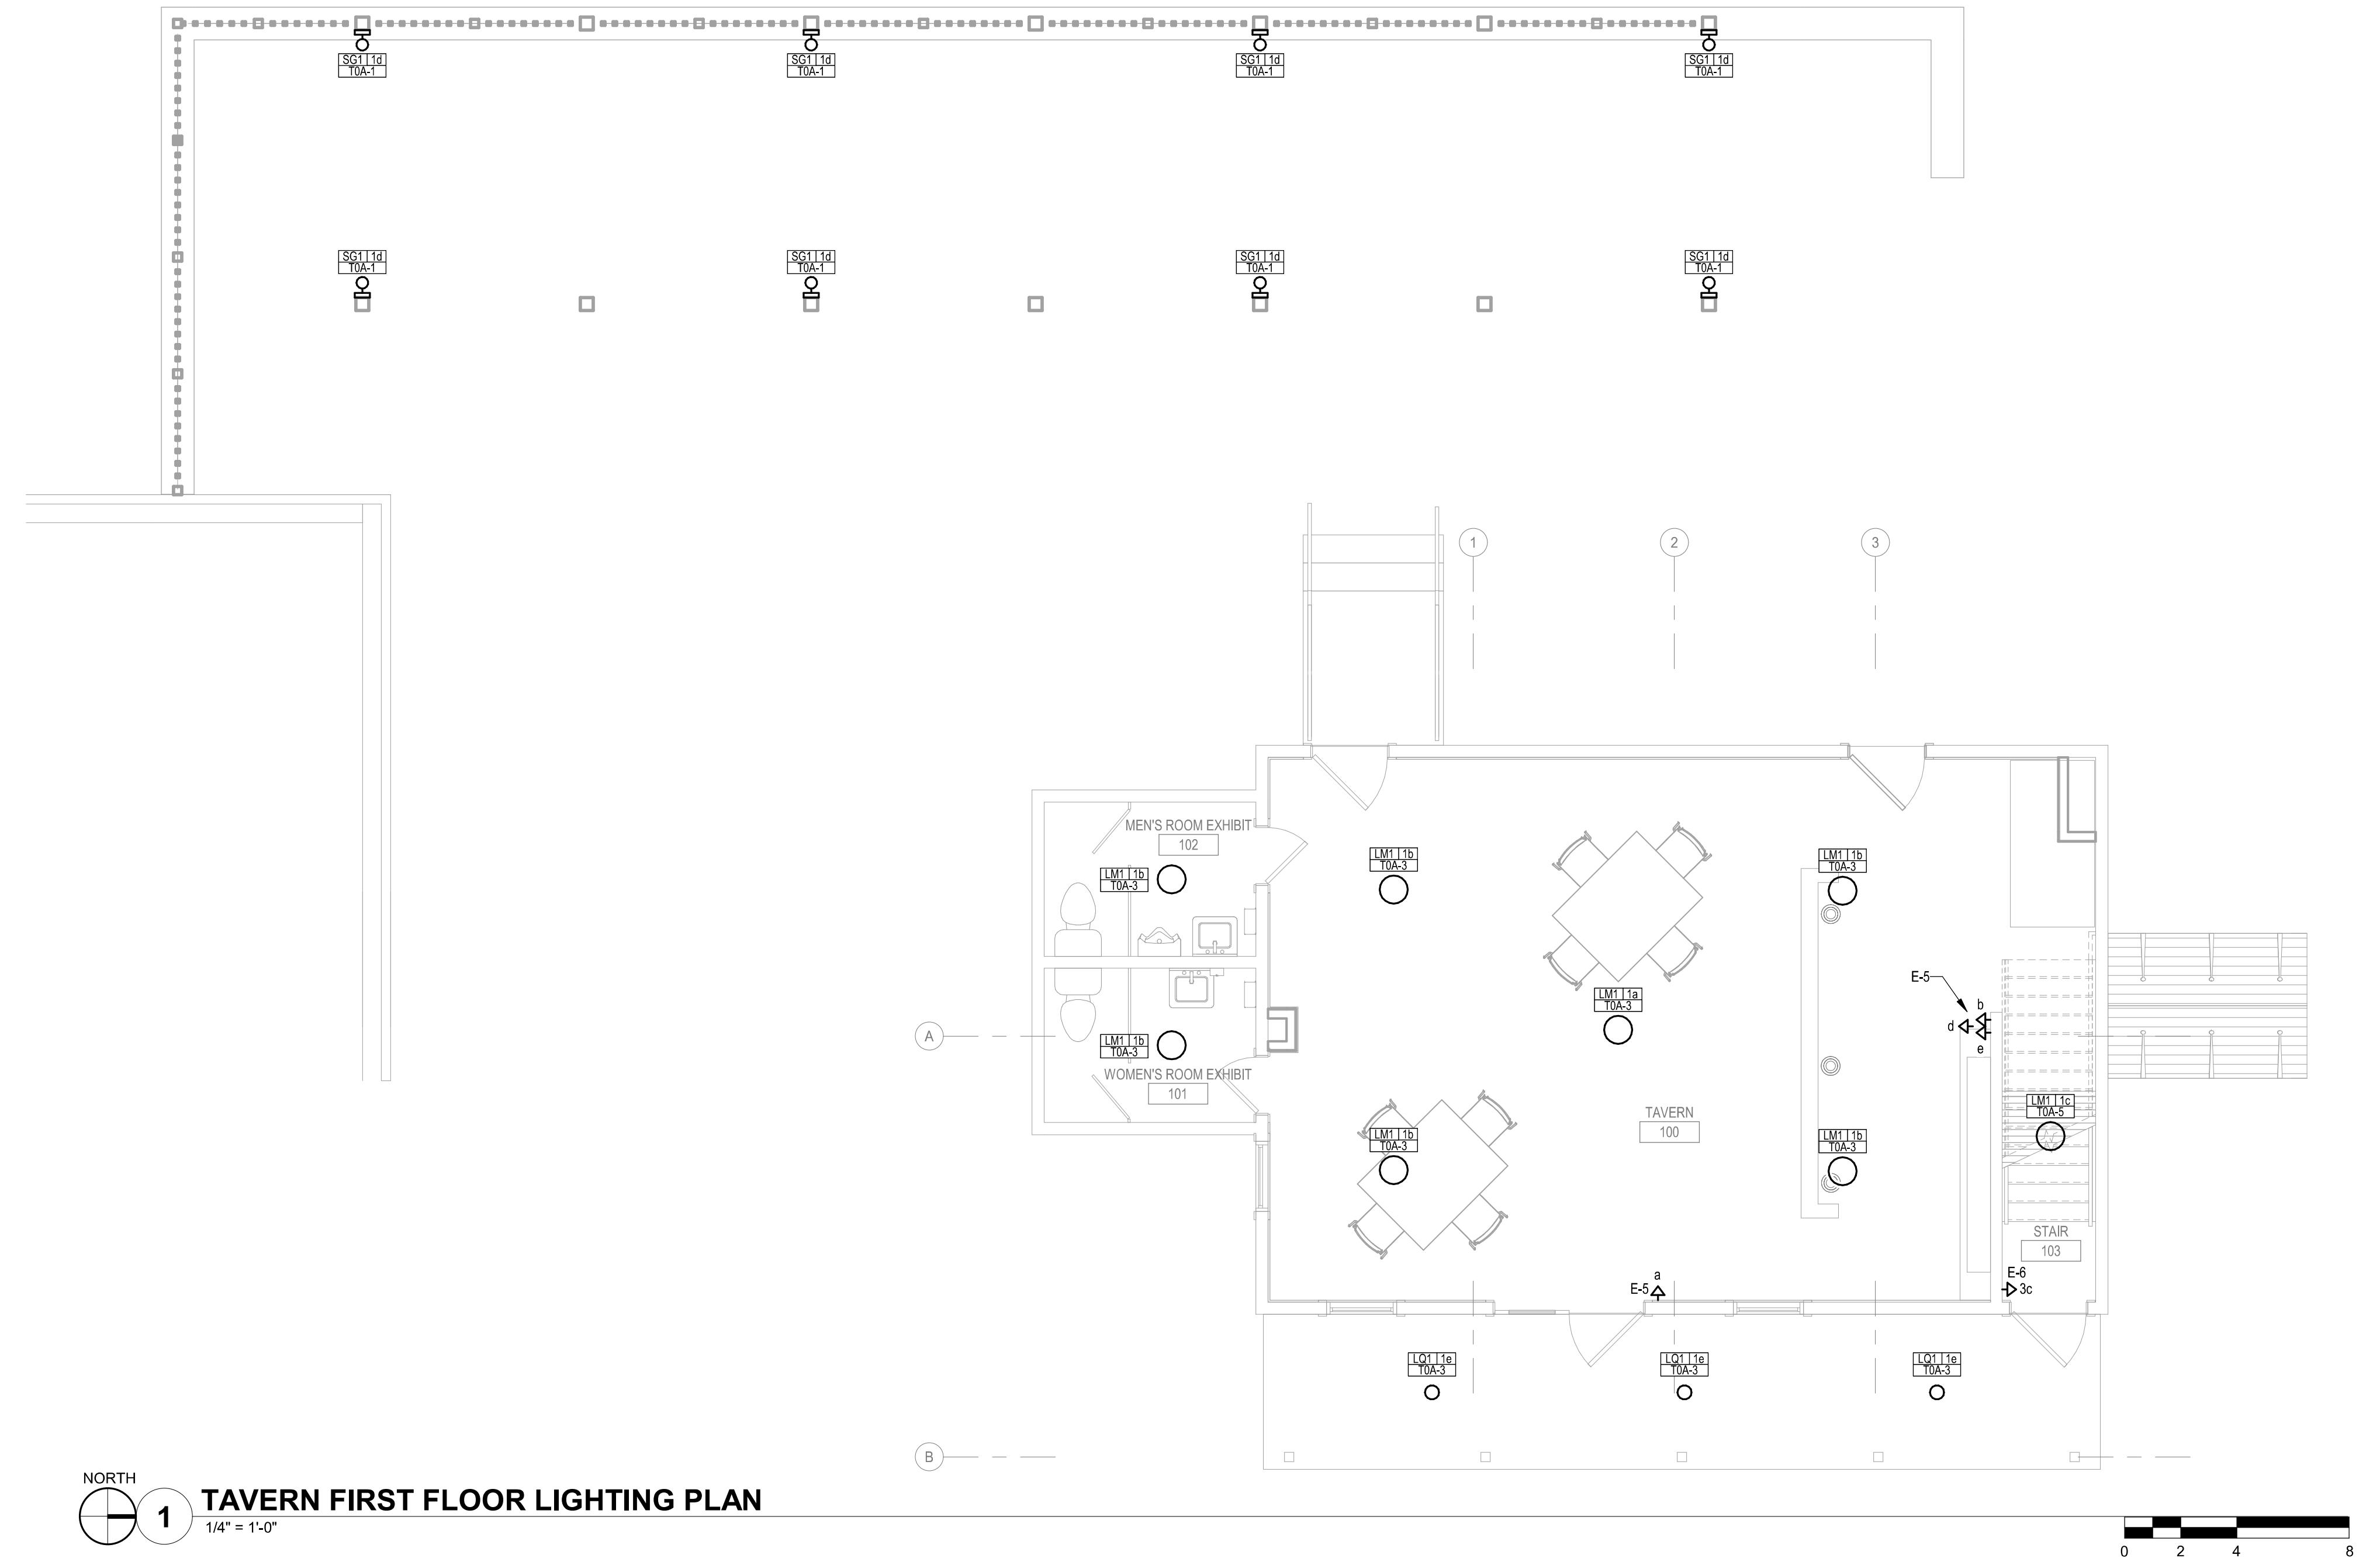

KEYED NOTES

E4 PROVIDE VINTAGE PUSH-BUTTON
STYLE LIGHT (2-BUTTON
RAISE/LOWER 3-WAY DIMMING TYPE)
SWITCHES (PRANGE & CO. ELECTRIC
MANUFACTURING CO., INC.)
MATCHING BURNISHED ANTIQUE
COVERPLATE (LEWIS OR EQUAL).
SEE DETAIL 1/E601

ARO EBERLE
ARCHITECTS
433 W. Washington Ave.
Suite 400
Madison, WI 53701
(608) 204-7464
AroEberle.com

Consultant:
DESIGN
ENGINEERS
Architectural Engineers
8801 Prairie View Lane SW, Suite 200
Cedar Rapids, IA 52404
(319) 365-1000 | Suite 100
Middleton, WI 53562 | 608-424-8815
designengineers.com




State of Wisconsin
Department of Administration
Division of Facilities Development

Tavern Renovations
Old World Wisconsin Ethnic Outdoor Museum
Wisconsin Historical Society
Town of Eagle, Wisconsin


Sheet Title:
TAVERN SECOND FLOOR ELECTRICAL PLANS

Old World Wisconsin Ethnic Outdoor Museum
Town of Eagle, Wisconsin

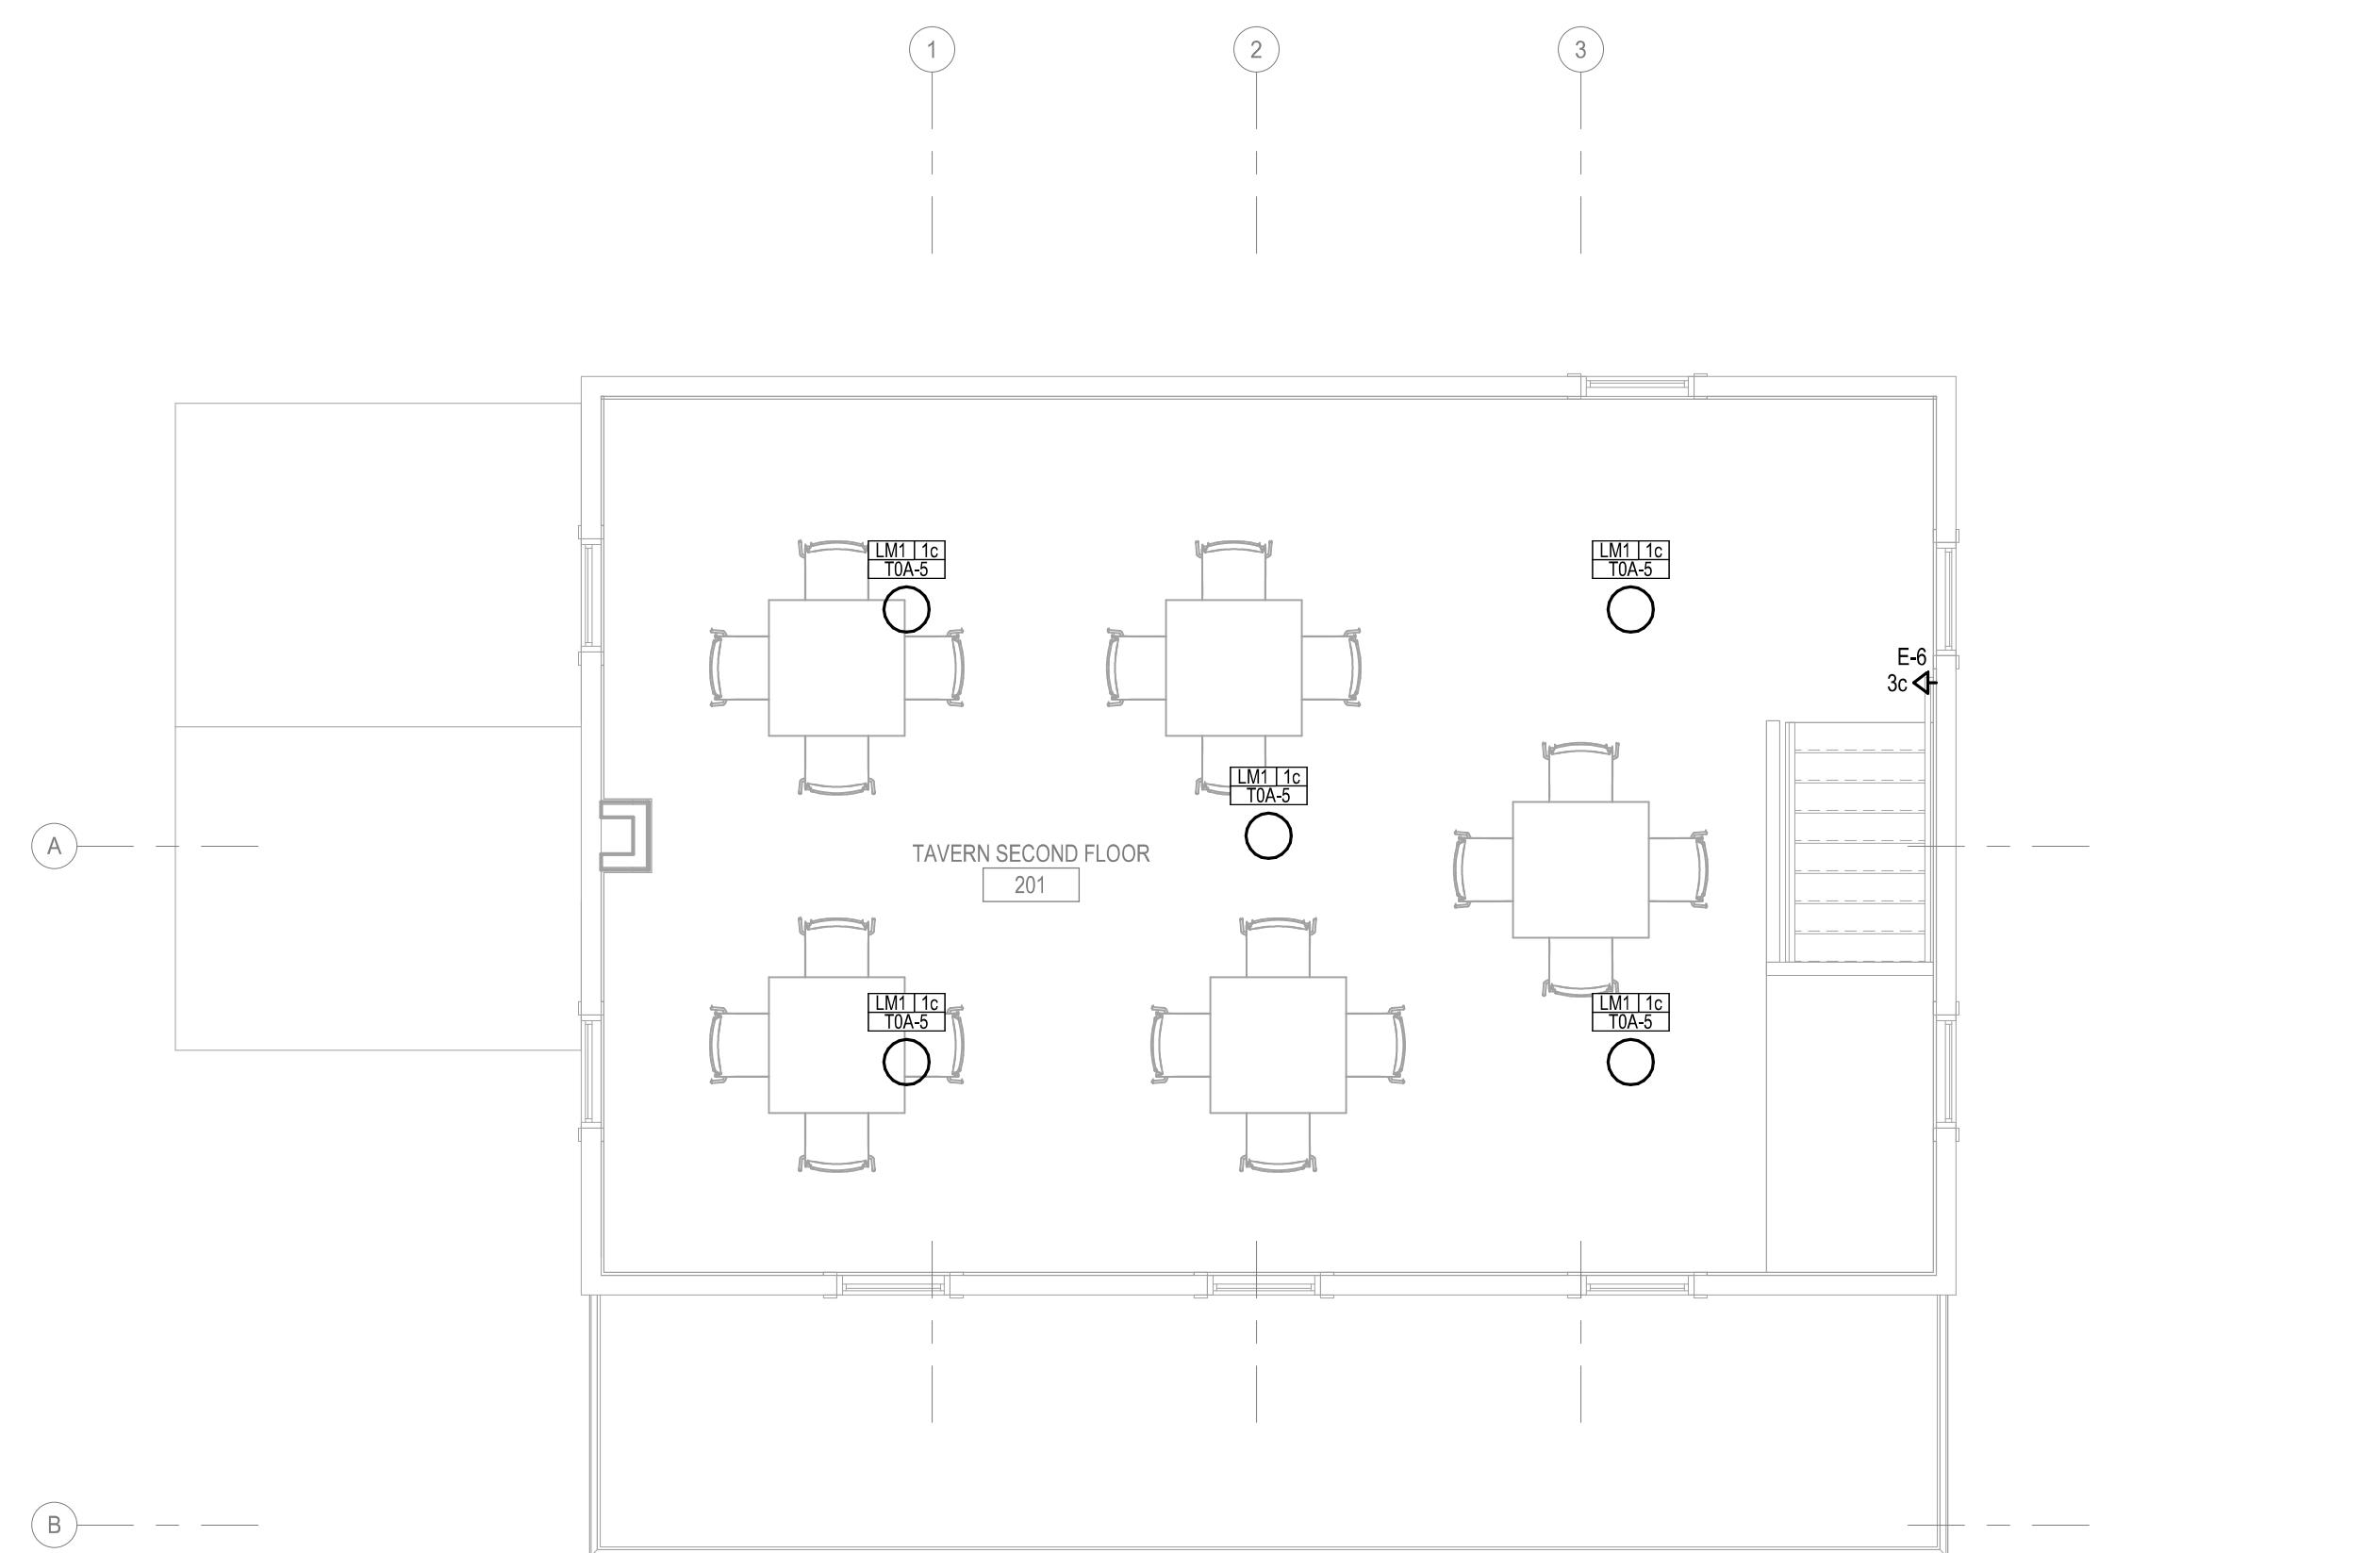

NORTH
1 TAVERN SECOND FLOOR LIGHTING PLAN
1/4" = 1'-0"

0 2 4 8

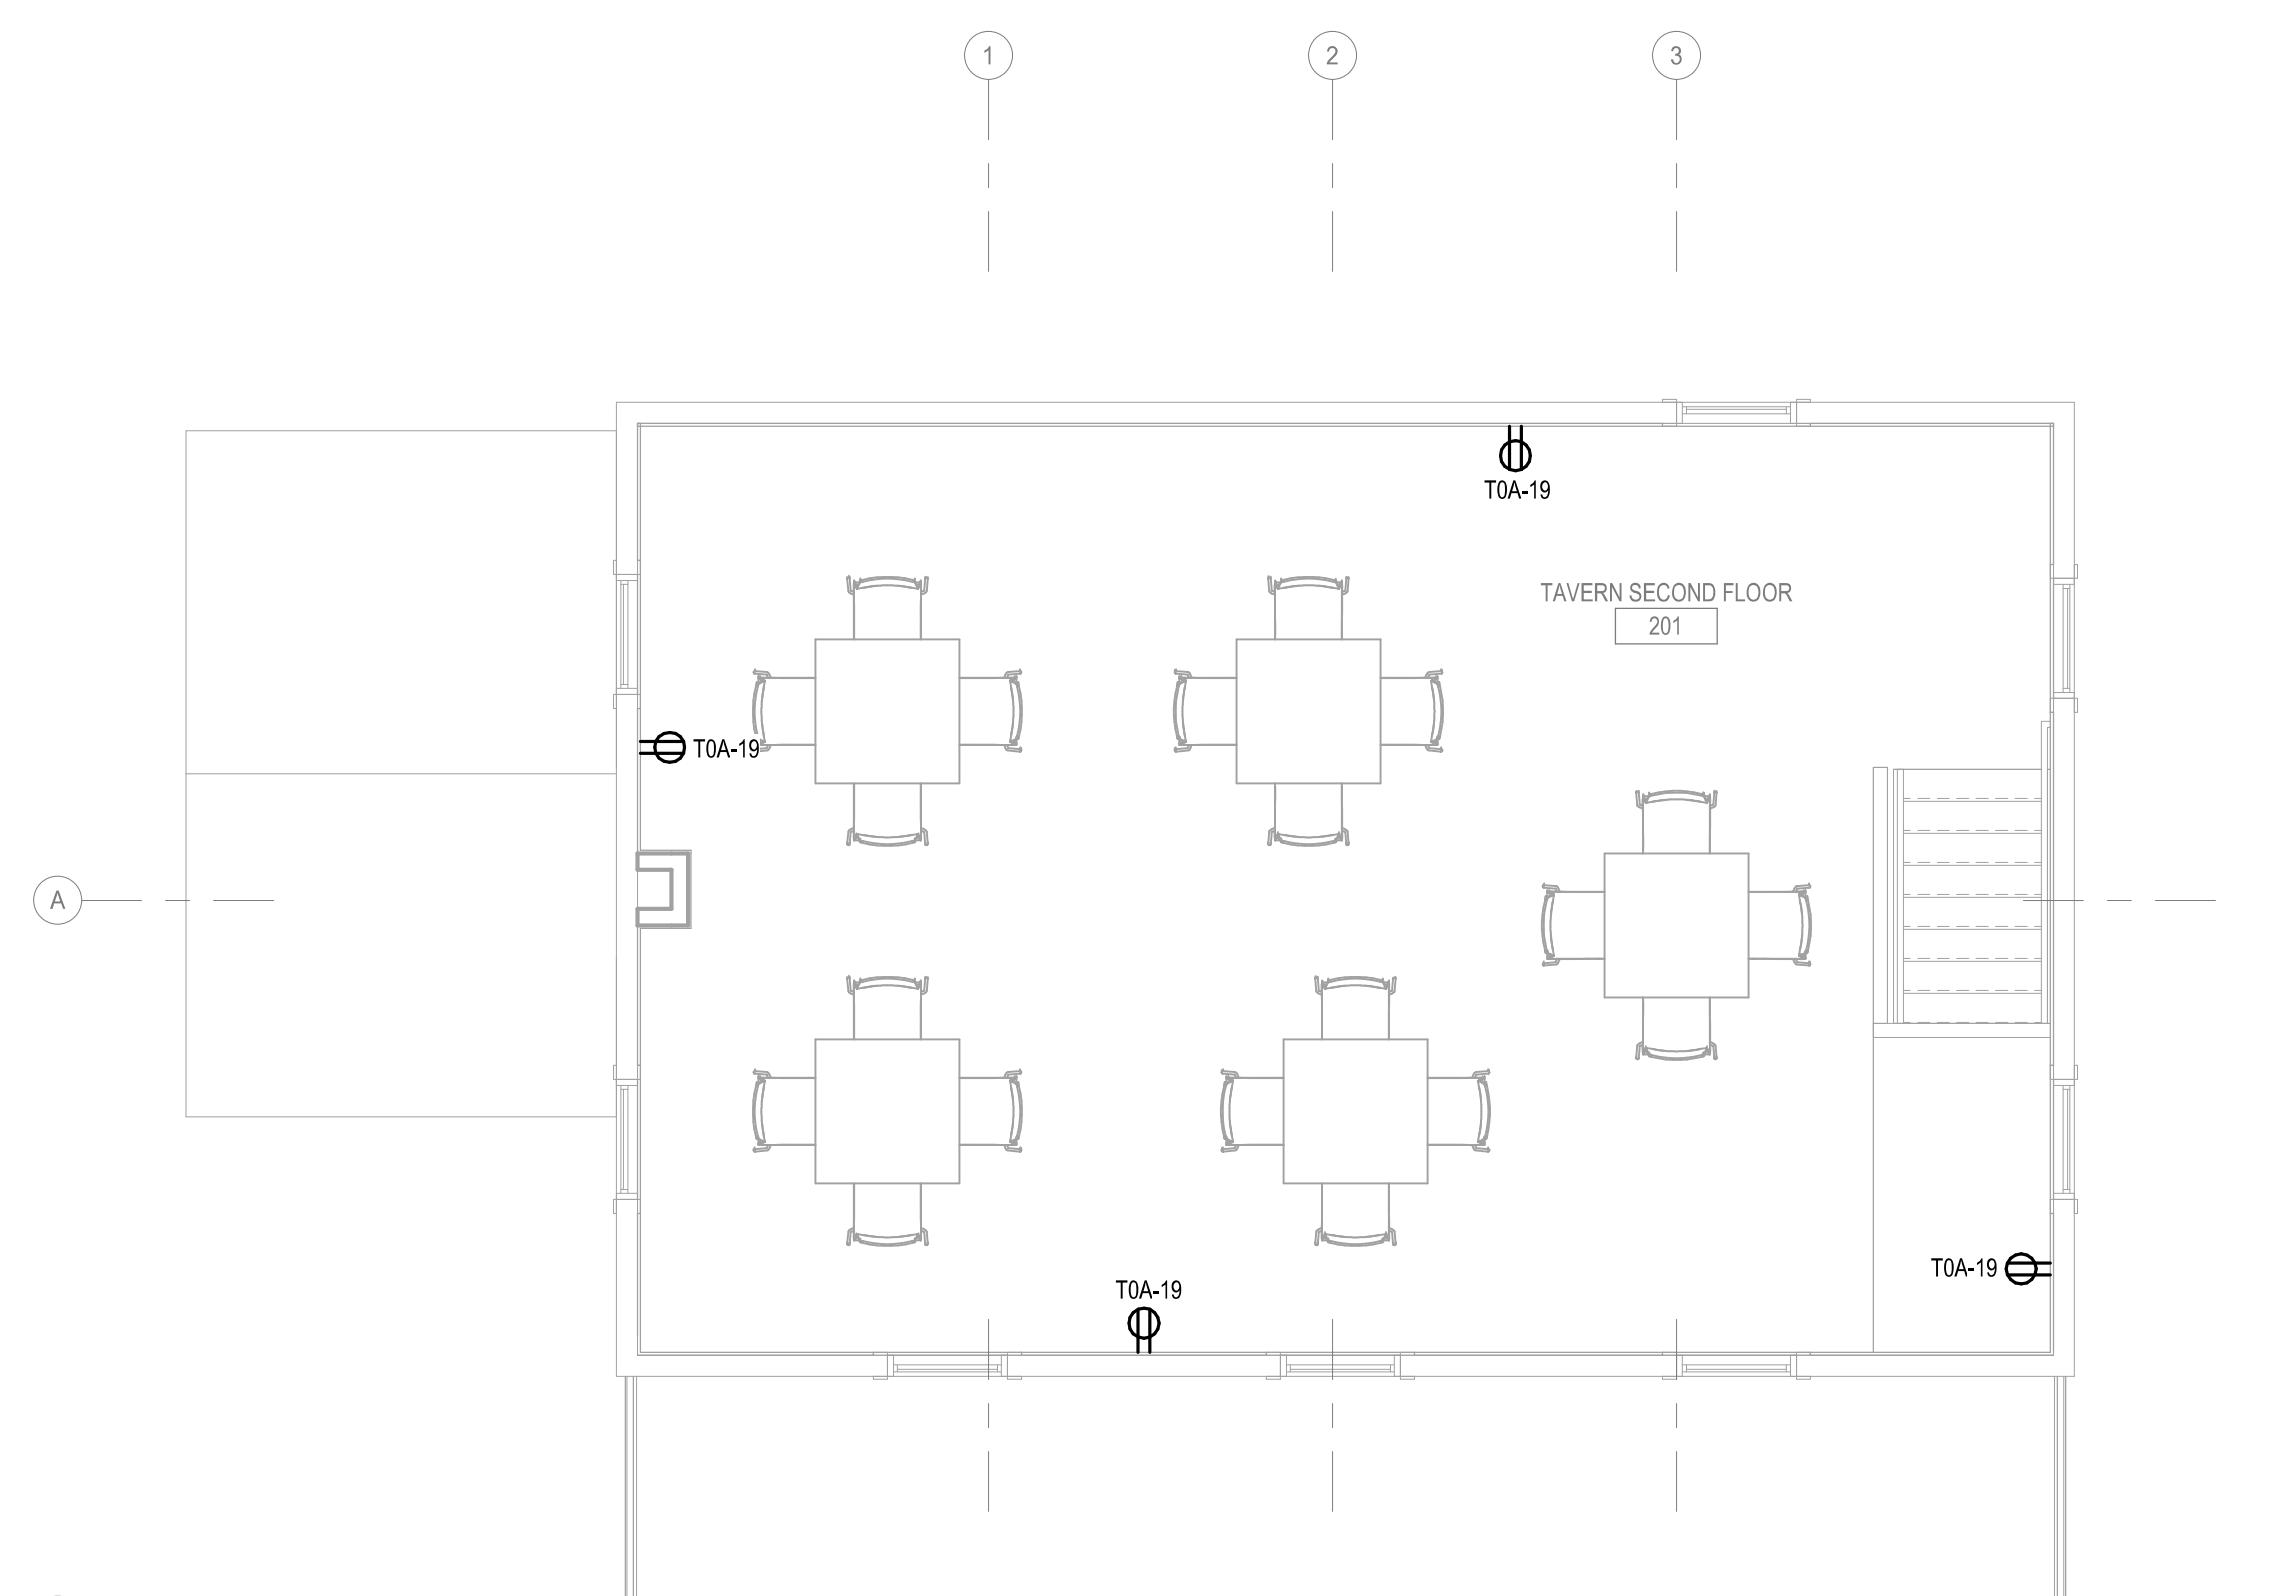

NORTH
2 TAVERN SECOND FLOOR POWER PLAN
1/4" = 1'-0"

0 2 4 8

LIGHTING/SWITCHING KEY	
LIGHTING	LIGHTING CONTROLS OPERATION SEQUENCE (0,1,2,...) PER DETAILS PER SCHEDULE
SWITCHING	SWITCHING ZONE (a,b,c...)
CIRCUIT NUMBER	CIRCUIT DATA, PANEL NAME, CIRCUIT NUMBER (XX-XXX#) OR CIRCUIT NOTE (E4)
EMERGENCY FIXTURE	EM - EMERGENCY FIXTURE NL - NIGHT LIGHT
COORDINATE CEILING MOUNTED DEVICES WITH ARCHITECTURAL REFLECTED CEILING PLAN	COORDINATE CEILING MOUNTED DEVICES WITH ARCHITECTURAL REFLECTED CEILING PLAN
SWITCHING	SWITCHING
(X)(X)(X)	(X)(X)(X) - LIGHTING CONTROL STATION


IX - INDICATES SWITCH CONTROLS. REFER TO LIGHTING
CONTROL STATION CONFIGURATION DETAIL.
(X)(X) - INDICATES SWING ZONE
(X)(X) - DIMMING INDICATES HEIGHT TO CENTER OF SWITCH
ABOVE FINISH FLOOR (+46" TO CENTER IF NOT SHOWN)

Graphic Scale	See Details
DFD Number	171K-04
Set Type	BD
Date Issued	9/8/2023
Sheet Number	E112

NEW WORK KEY
EXISTING
NEW / REVISED
EXISTING EQUIPMENT
NEW / REVISED EQUIPMENT



State of Wisconsin
Department of Administration
Division of Facilities Development

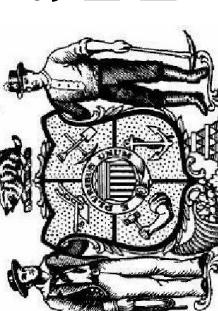


Old World Wisconsin Ethnic Outdoor Museum
Town of Eagle, Wisconsin

Tavern Renovations
Old World Wisconsin Ethnic Outdoor Museum
Wisconsin Historical Society
Town of Eagle, Wisconsin

Sheet Title:
TAVERN ATTIC ELECTRICAL PLANS


Revisions:

No. Date Description

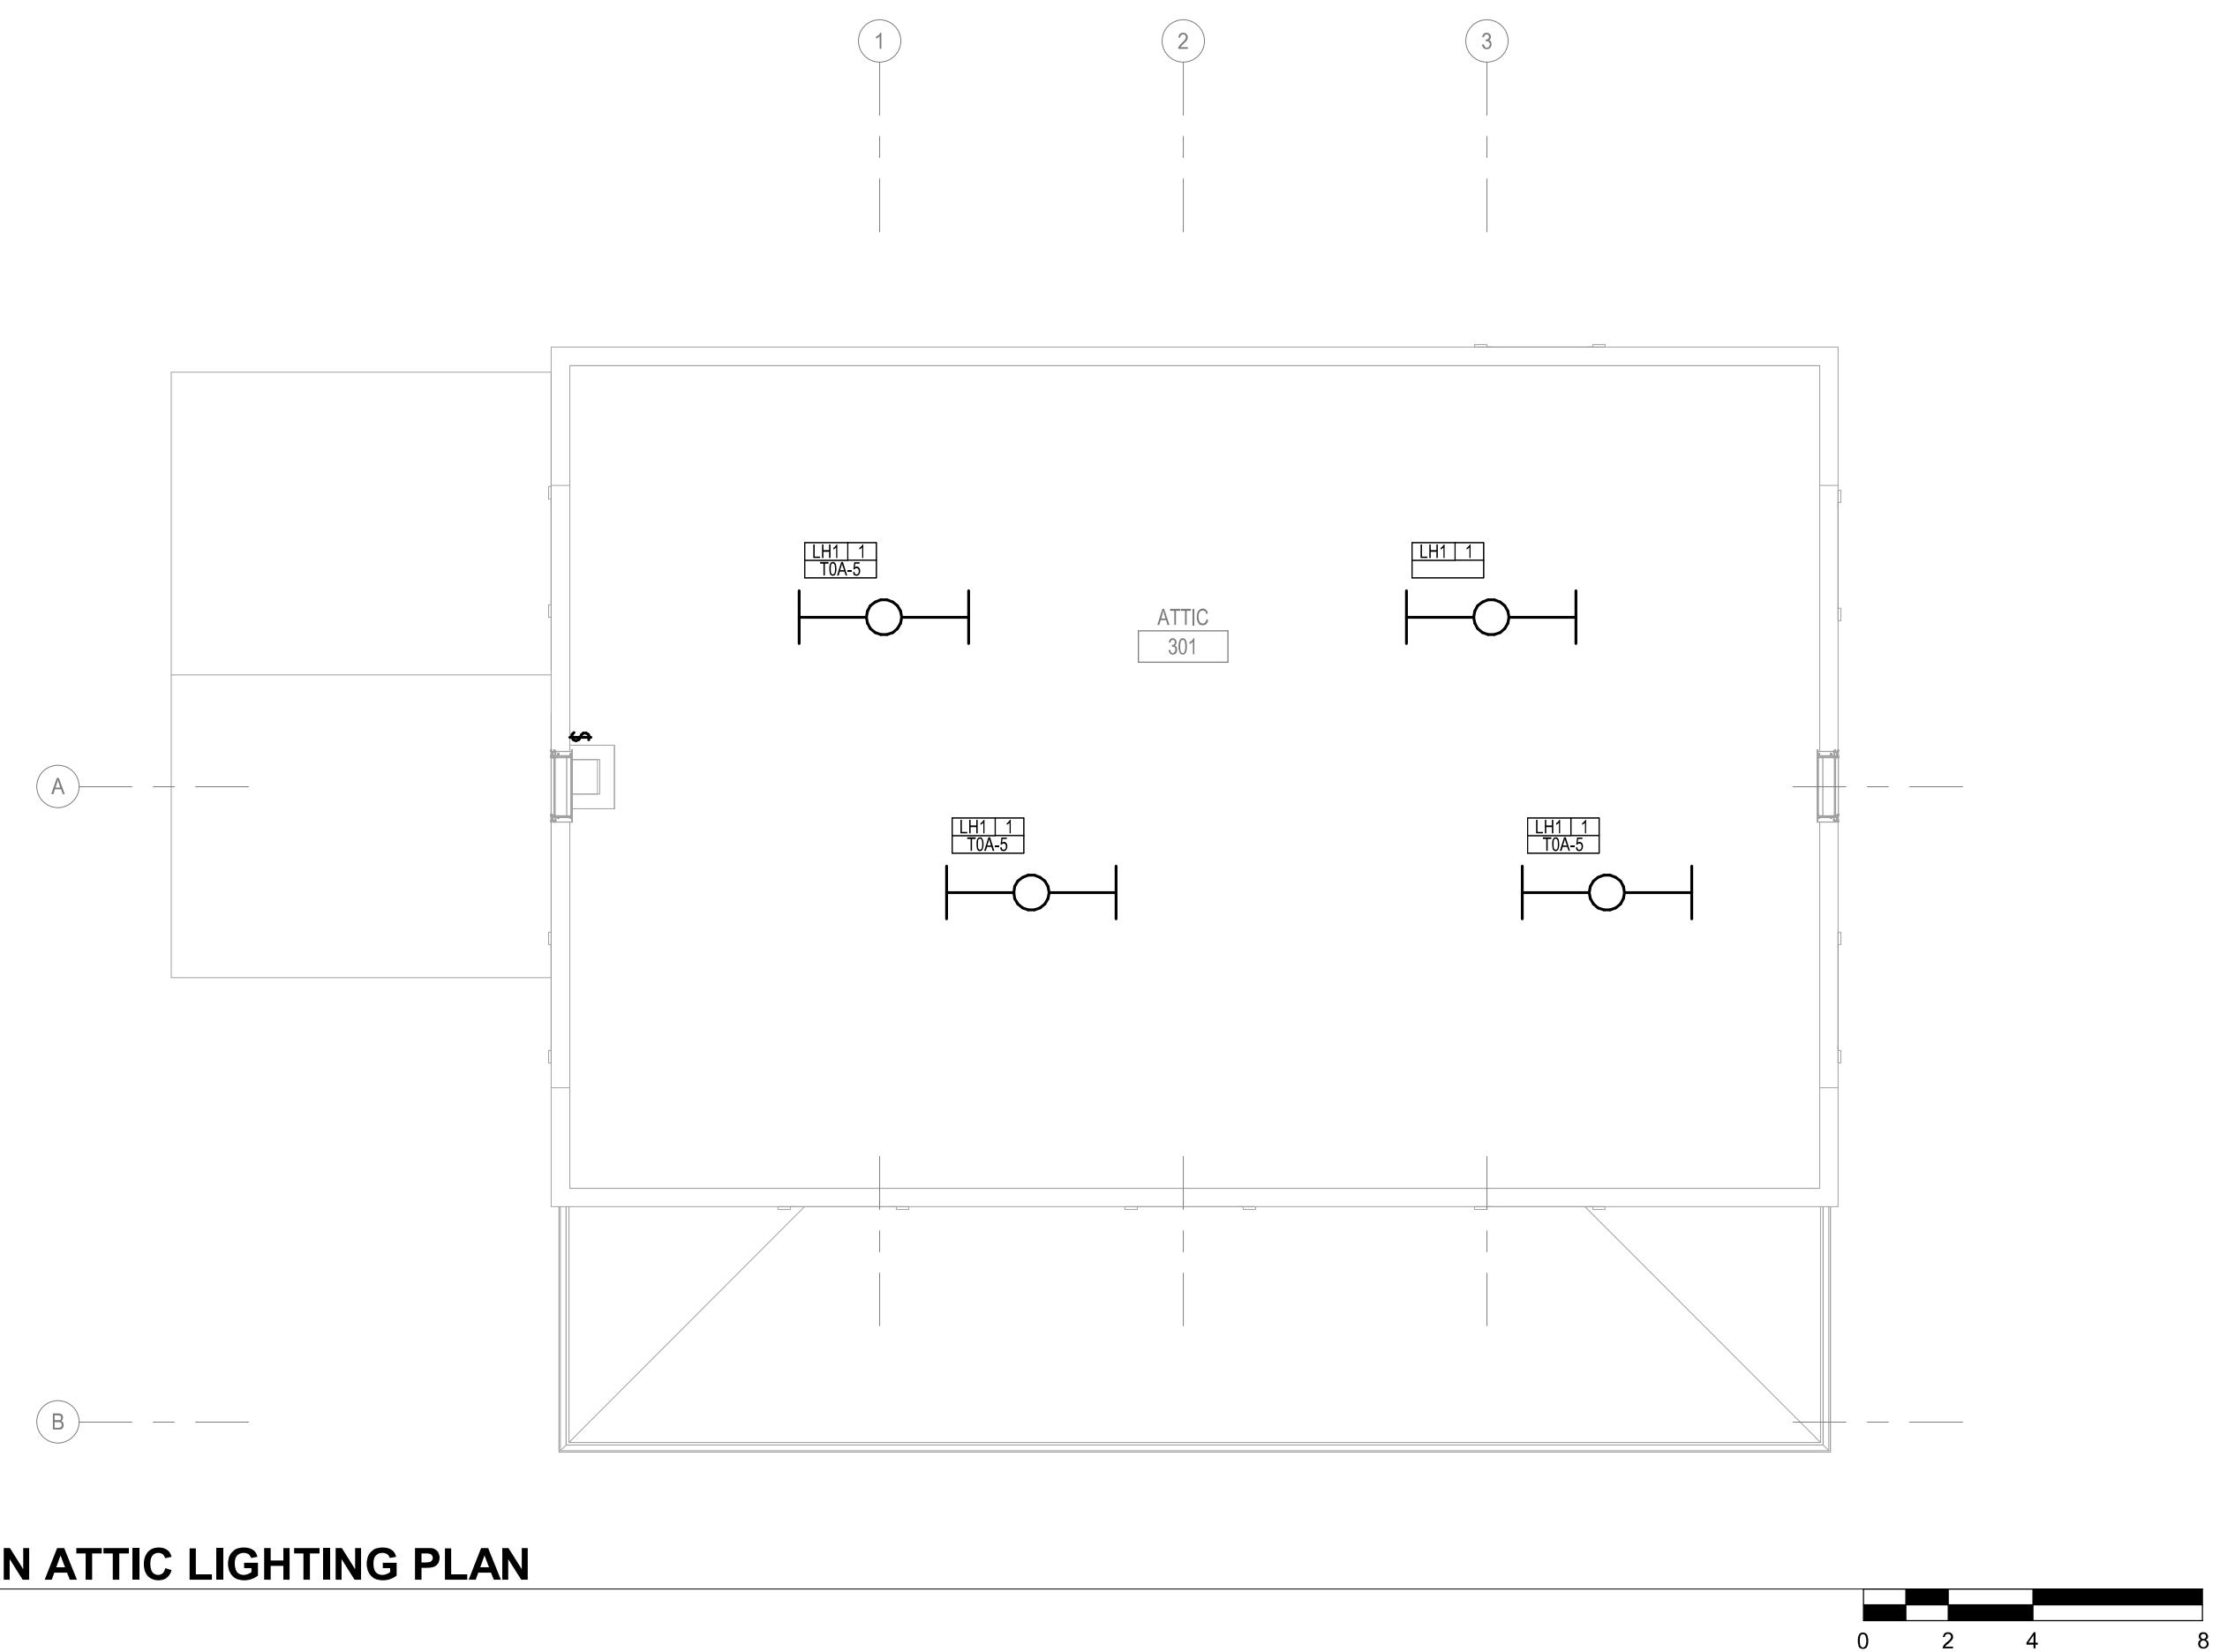

NORTH
1 TAVERN ATTIC LIGHTING PLAN
1/4" = 1'-0"

0 2 4 8

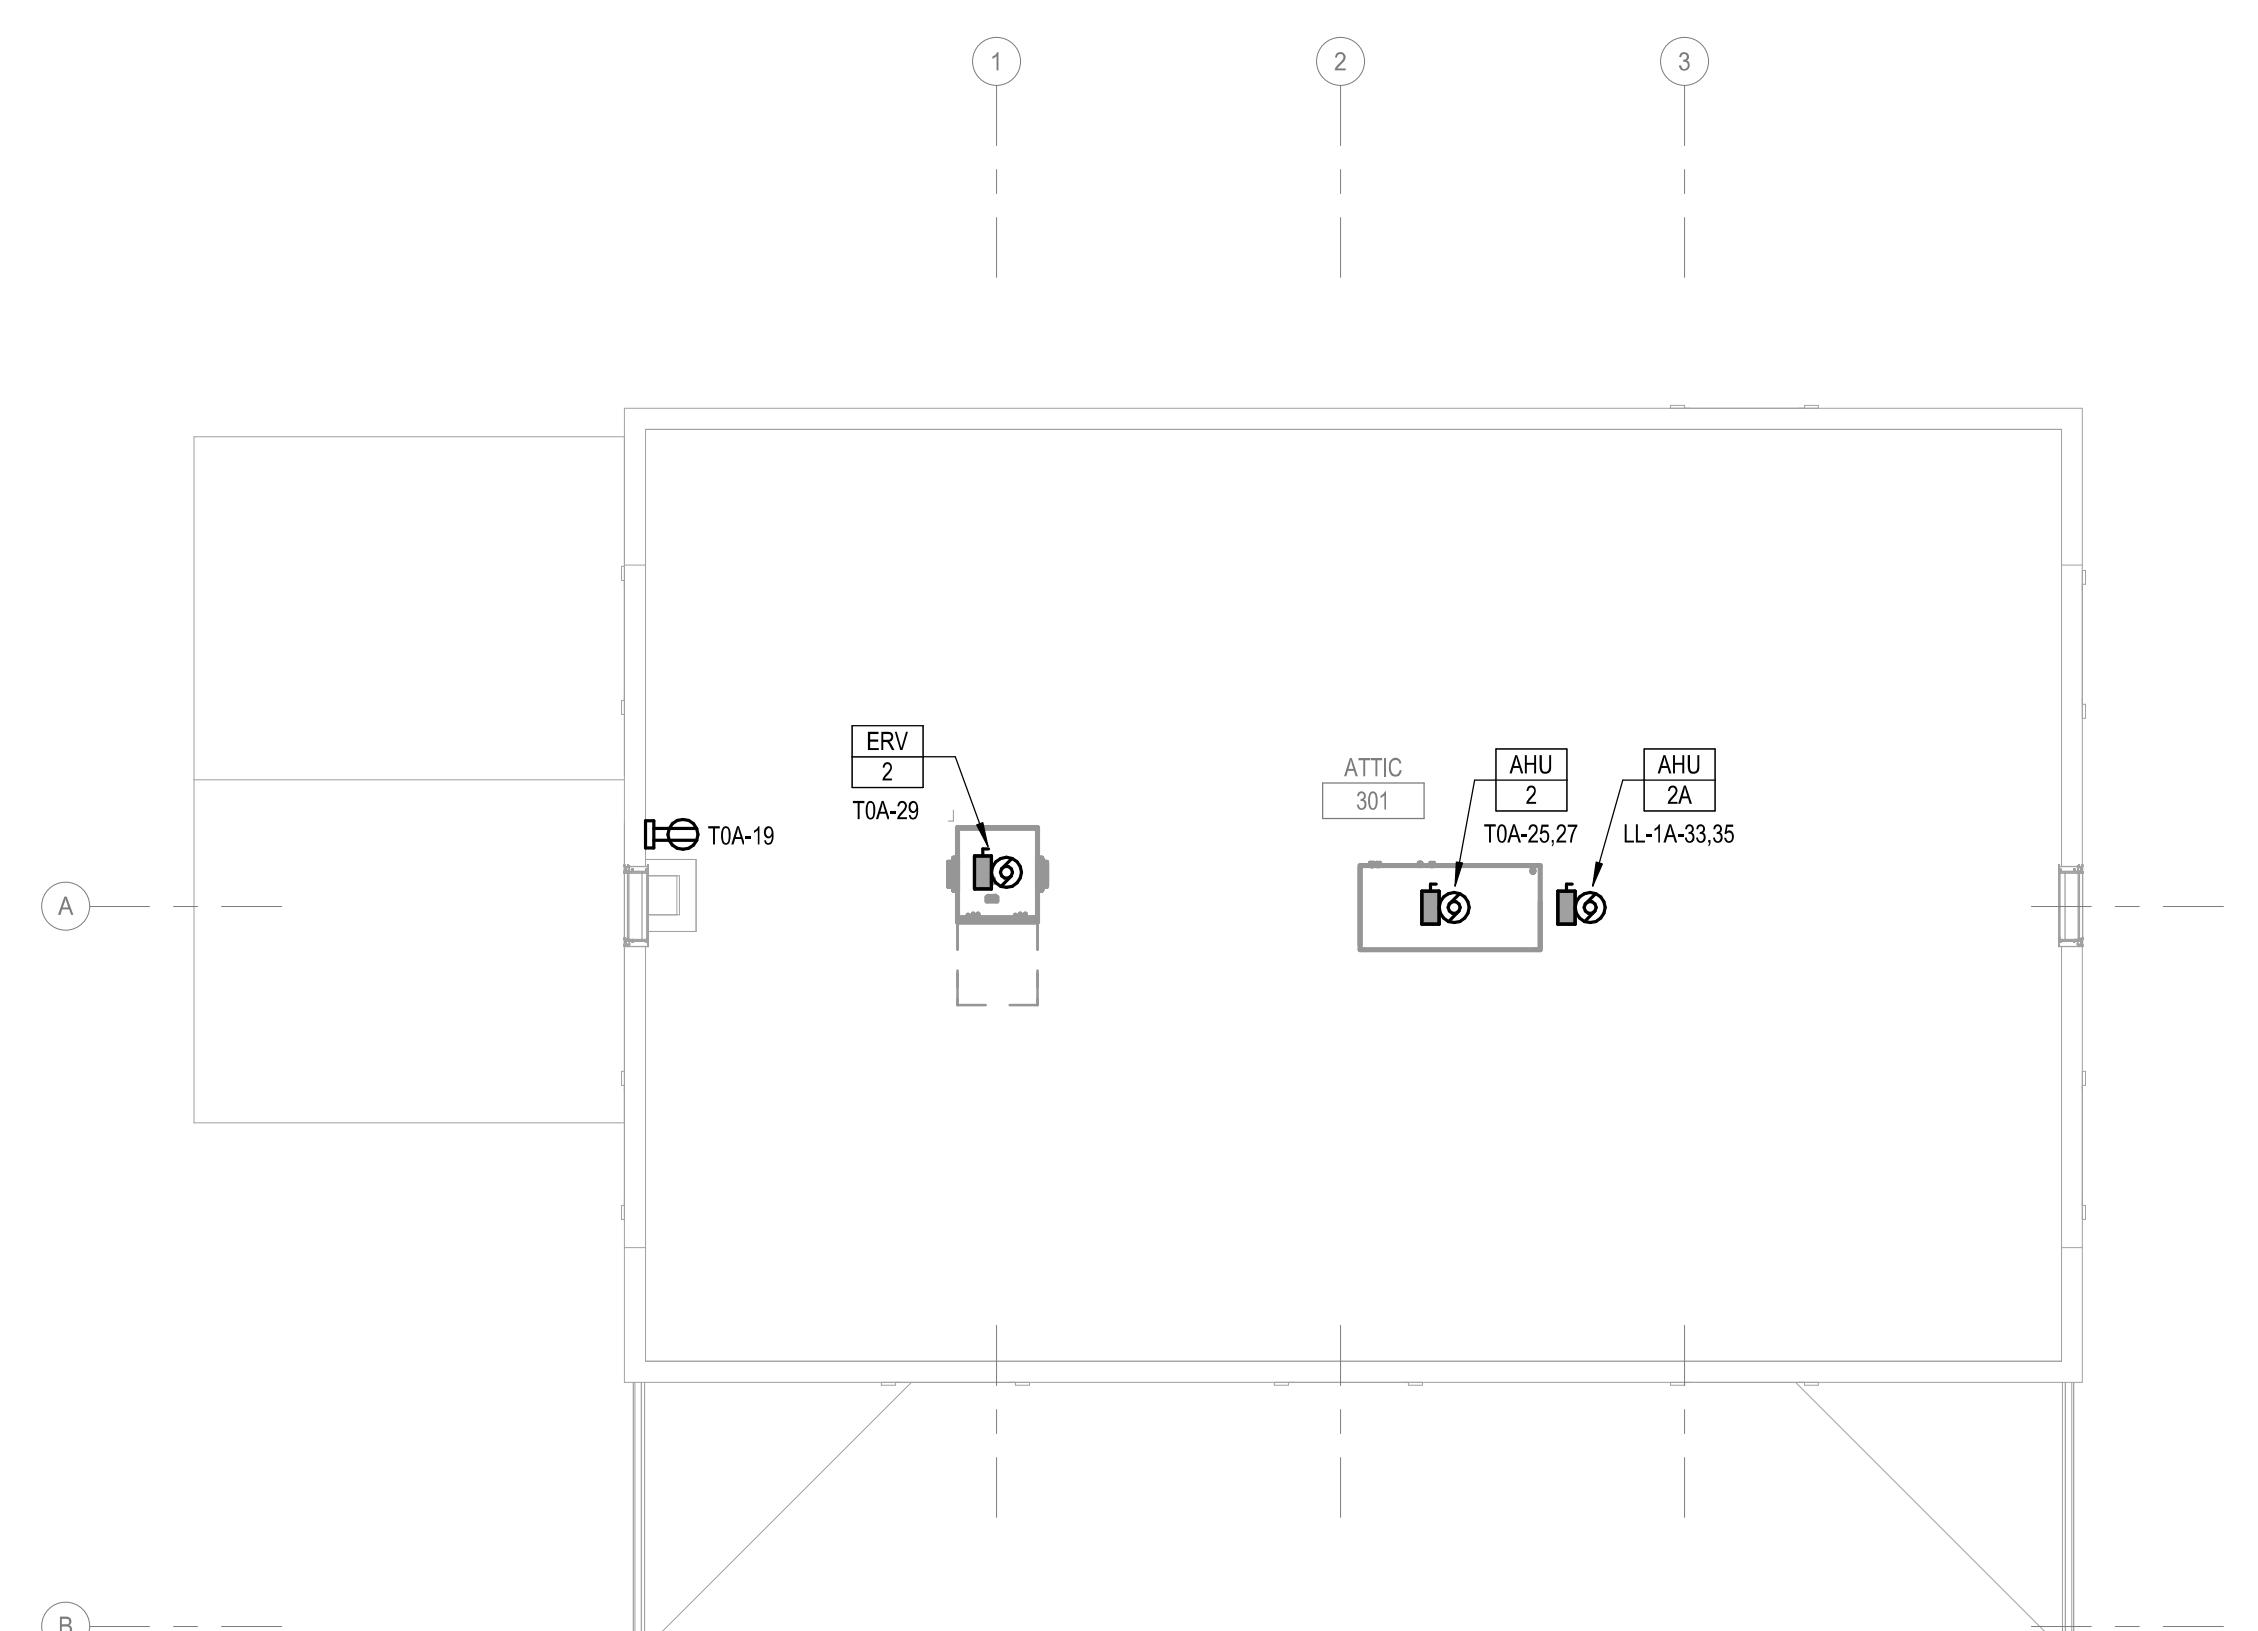

NORTH
2 TAVERN ATTIC POWER PLAN
1/4" = 1'-0"

0 2 4 8

LIGHTING/SWITCHING KEY	
LIGHTING	LIGHTING CONTROLS OPERATION SEQUENCE (0,1,2,...) PER DETAILS PER SCHEDULE
SWITCHING	SWITCHING ZONE (a,b,c...)
EMERGENCY FIXTURE	CIRCUIT DATA, PANEL NAME, CIRCUIT NUMBER (XX-XXX#) OR CIRCUIT NOTE (E-#)
EMERGENCY FIXTURE NL - NIGHT LIGHT	
COORDINATE CEILING MOUNTED DEVICES WITH ARCHITECTURAL REFLECTED CEILING PLAN	
SWITCHING	
(X)(X)(X) - LIGHTING CONTROL STATION	

IX - INDICATES SWITCH CONTROLS. REFER TO LIGHTING CONTROL STATION CONFIGURATION DETAIL.
(x)(x) - INDICATES SWITCH ZONE
(x)(x) - DIMENSIONS INDICATE HEIGHT TO CENTER OF SWITCH ABOVE FINISH FLOOR (+46" TO CENTER IF NOT SHOWN)

NEW WORK KEY	
—	EXISTING
—	NEW / REVISED
—	EXISTING EQUIPMENT
■	NEW / REVISED EQUIPMENT

Graphic Scale See Details	
DFD Number	171K-04
Set Type	BD
Date Issued	9/8/2023
Sheet Number	E113

KEYED NOTES

E-1 PROVIDE 100A BREAKER TO MATCH OTHER BREAKERS IN EXISTING PANEL.


E-2 TYPICAL: FOR EACH SEPARATE BUILDING, PROVIDE DRIVEN GROUND ROD AND BOND TO MAIN PANEL. GROUND BAR WITH #2 AWG COPPER.

ARO EBERLE ARCHITECTS
433 W. Washington Ave.
Madison, WI 53703
(608) 204-7464
AroEberle.com

Consultant:
DESIGN ENGINEERS
8801 Prairie View Lane SW, Suite 200
Cedar Rapids, IA 52404
(319) 365-1500 | Suite 100
Middleton, WI 53562 | 608-424-8815
designengineers.com




State of Wisconsin
Department of Administration
Division of Facilities Development

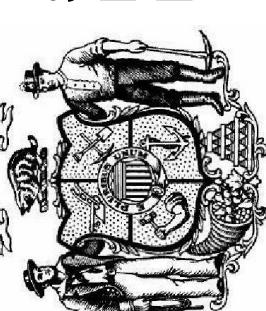

Old World Wisconsin Ethnic Outdoor Museum
Town of Eagle, Wisconsin

Tavern Renovations
Old World Wisconsin Ethnic Outdoor Museum
Wisconsin Historical Society
Town of Eagle, Wisconsin

Sheet Title:
ELECTRICAL ONE-LINE DIAGRAM

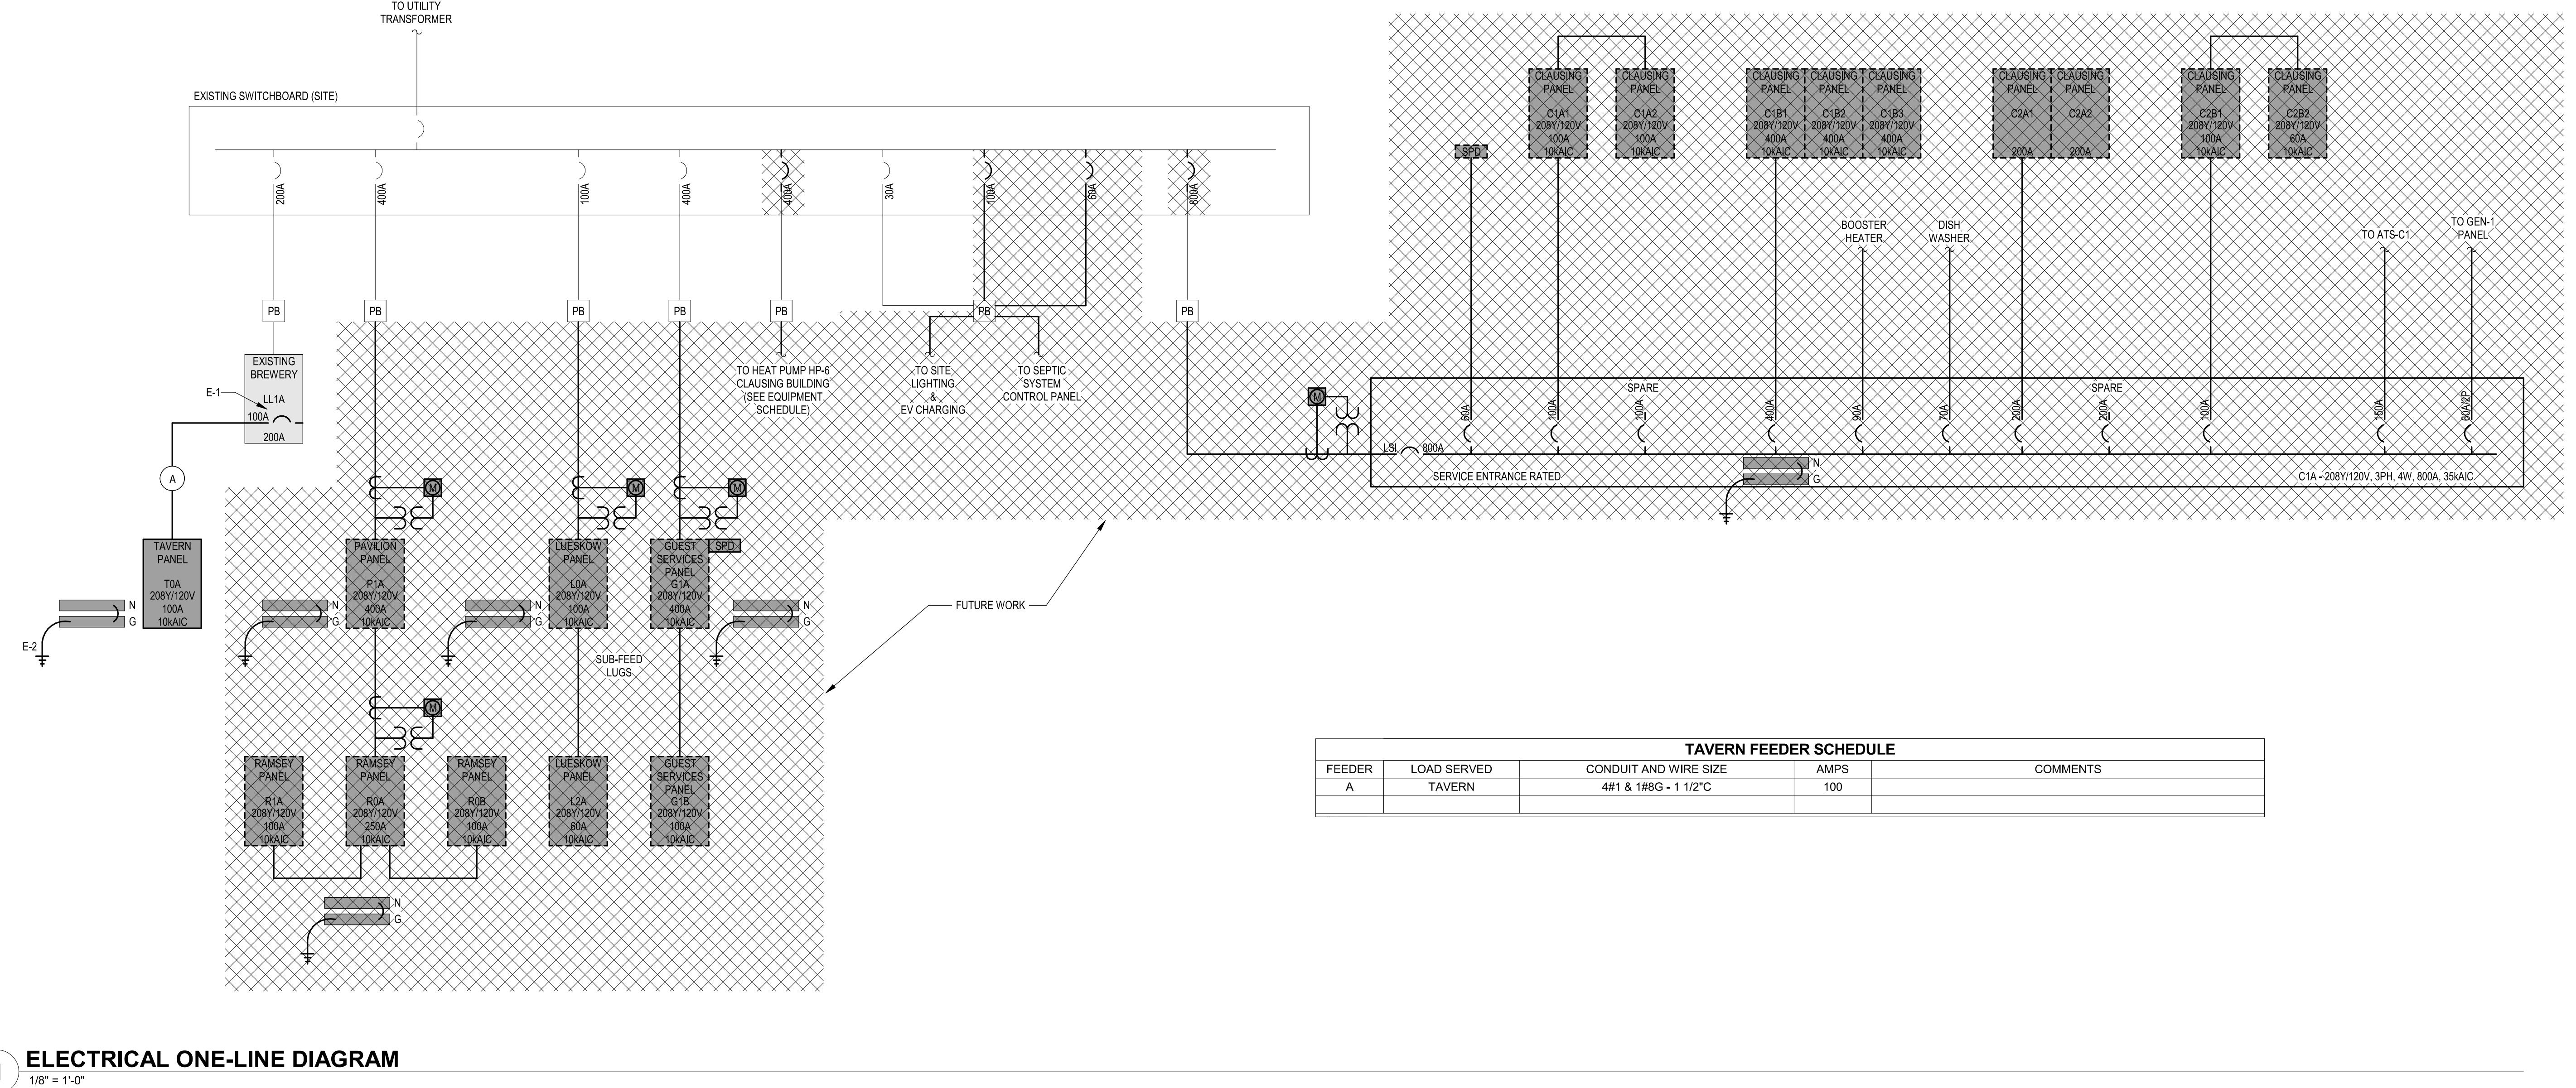

TAVERN FEEDER SCHEDULE				
FEEDER	LOAD SERVED	CONDUIT AND WIRE SIZE	AMPS	COMMENTS
A	TAVERN	4#1 & 1#6G - 1 1/2°C	100	

PANELBOARD NAMING CONVENTION:	
X	= BUILDING
C	= CLAUSING BARN
G	= GUEST SERVICES CENTER
L	= LUESKOV HOUSE
P	= PAVILION
R	= RAMSEY BARN
T	= TAVERN
1	= FLOOR LEVEL "0" FOR LOWER LEVEL, "1" FOR FIRST FLOOR, ETC.
Y	= PANEL DESIGNATOR
Z	= ADDITIONAL PANEL DESCRIPTOR

Graphic Scale No Scale




DFD Number 1711K-04

Set Type BD

Date Issued 9/8/2023


Sheet Number E401

DEMO/NEW/FUTURE KEY
— EXISTING
— NEW / REVISED
- - - FUTURE
■■■ EXISTING EQUIPMENT
■■■ NEW / REVISED EQUIPMENT
■■■■■ FUTURE EQUIPMENT

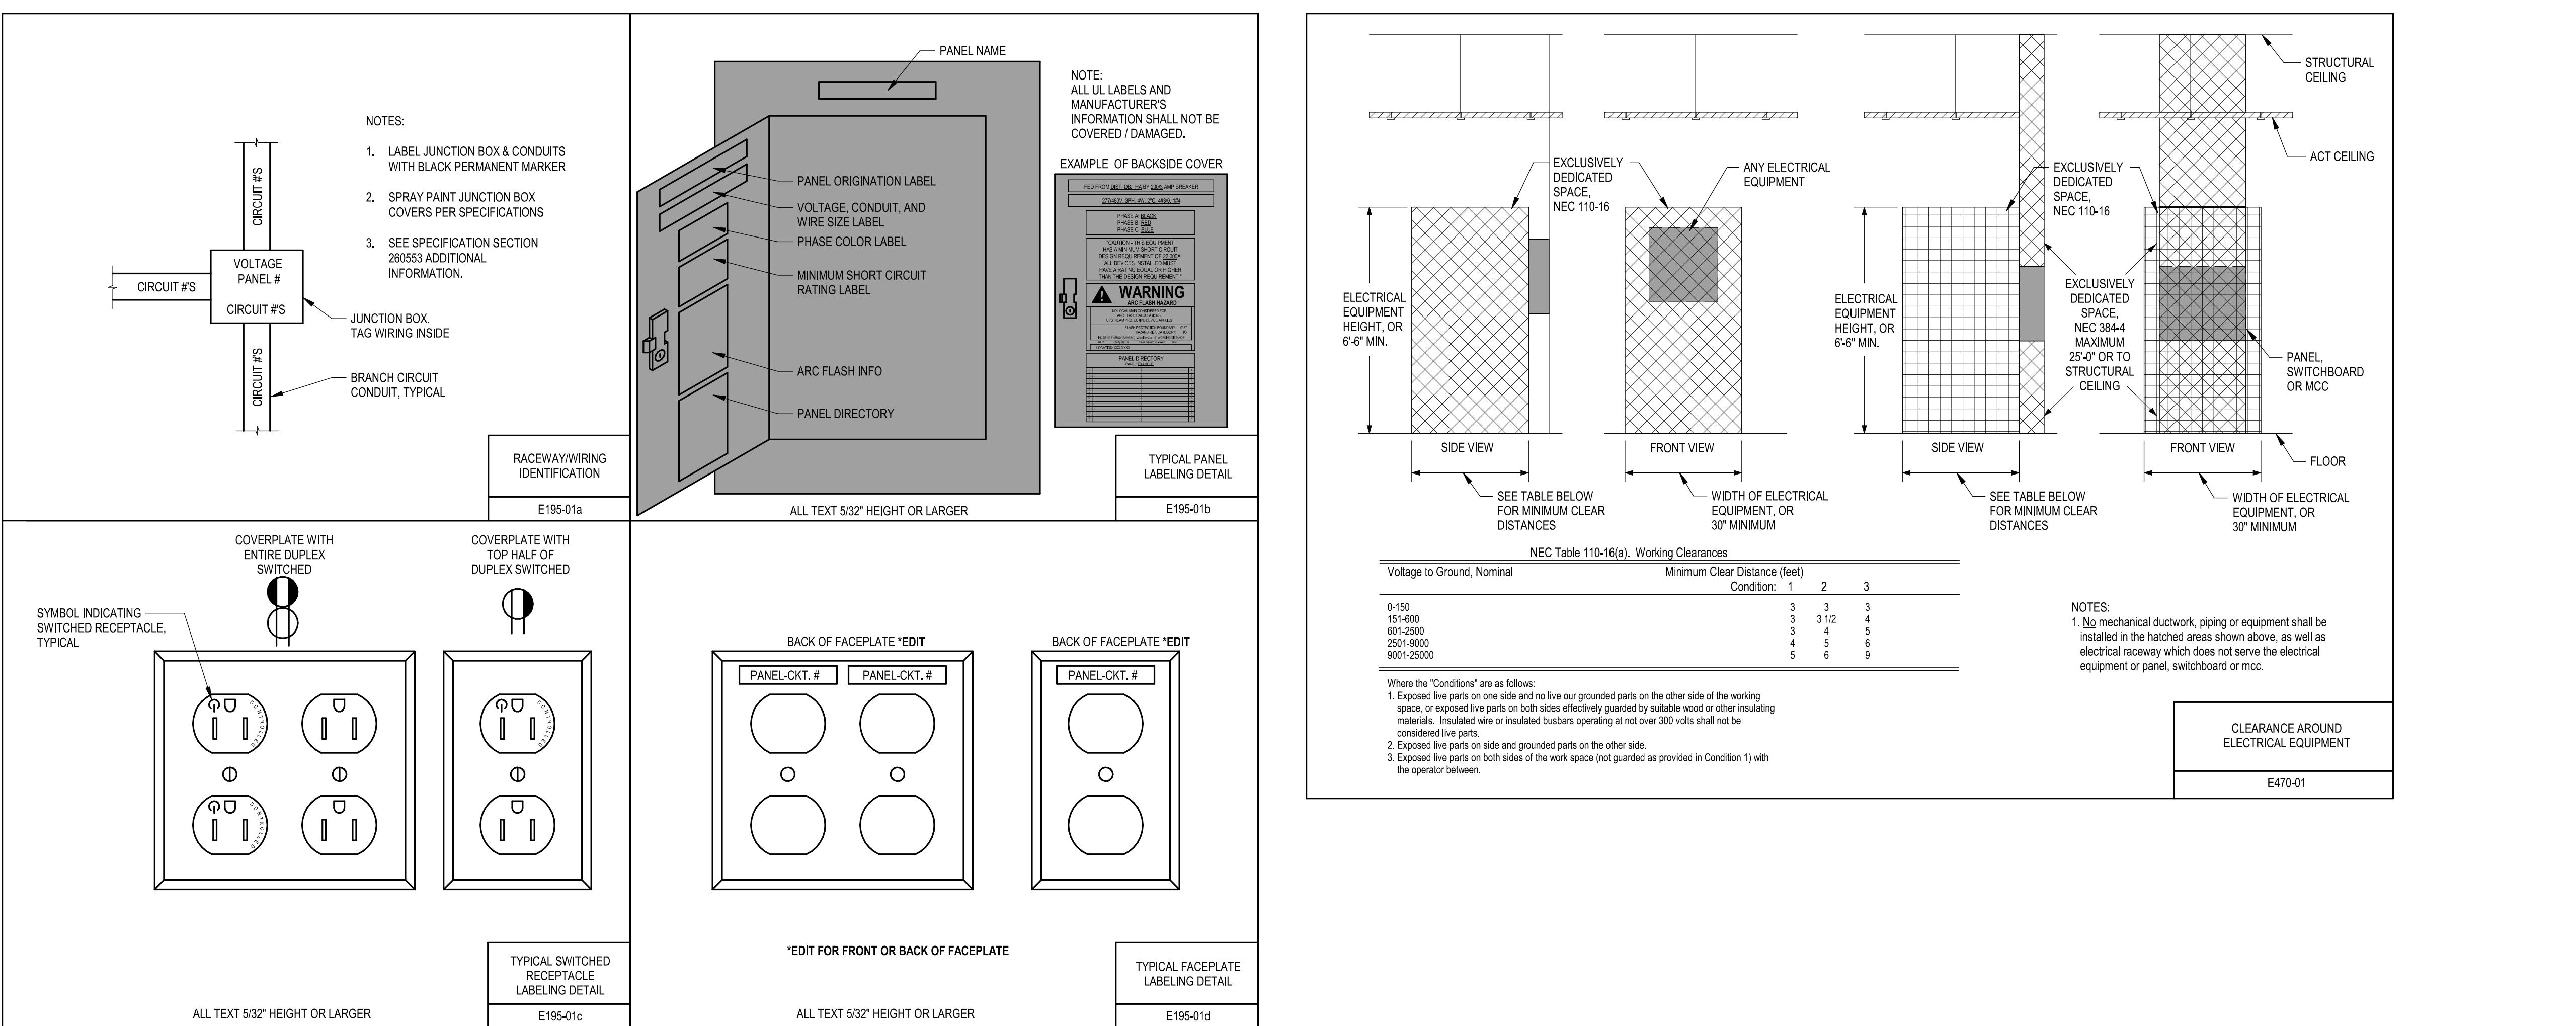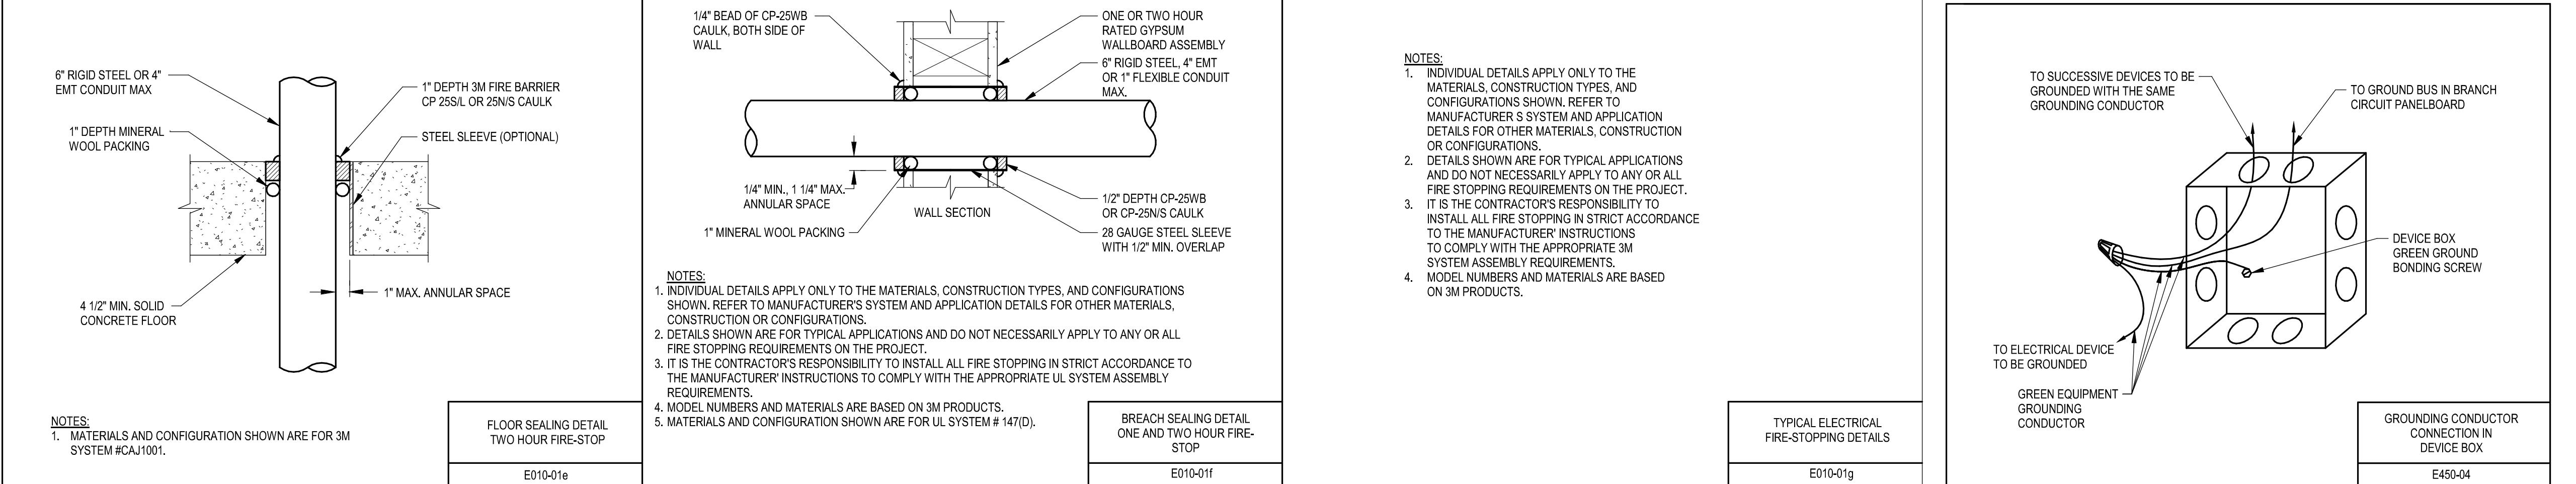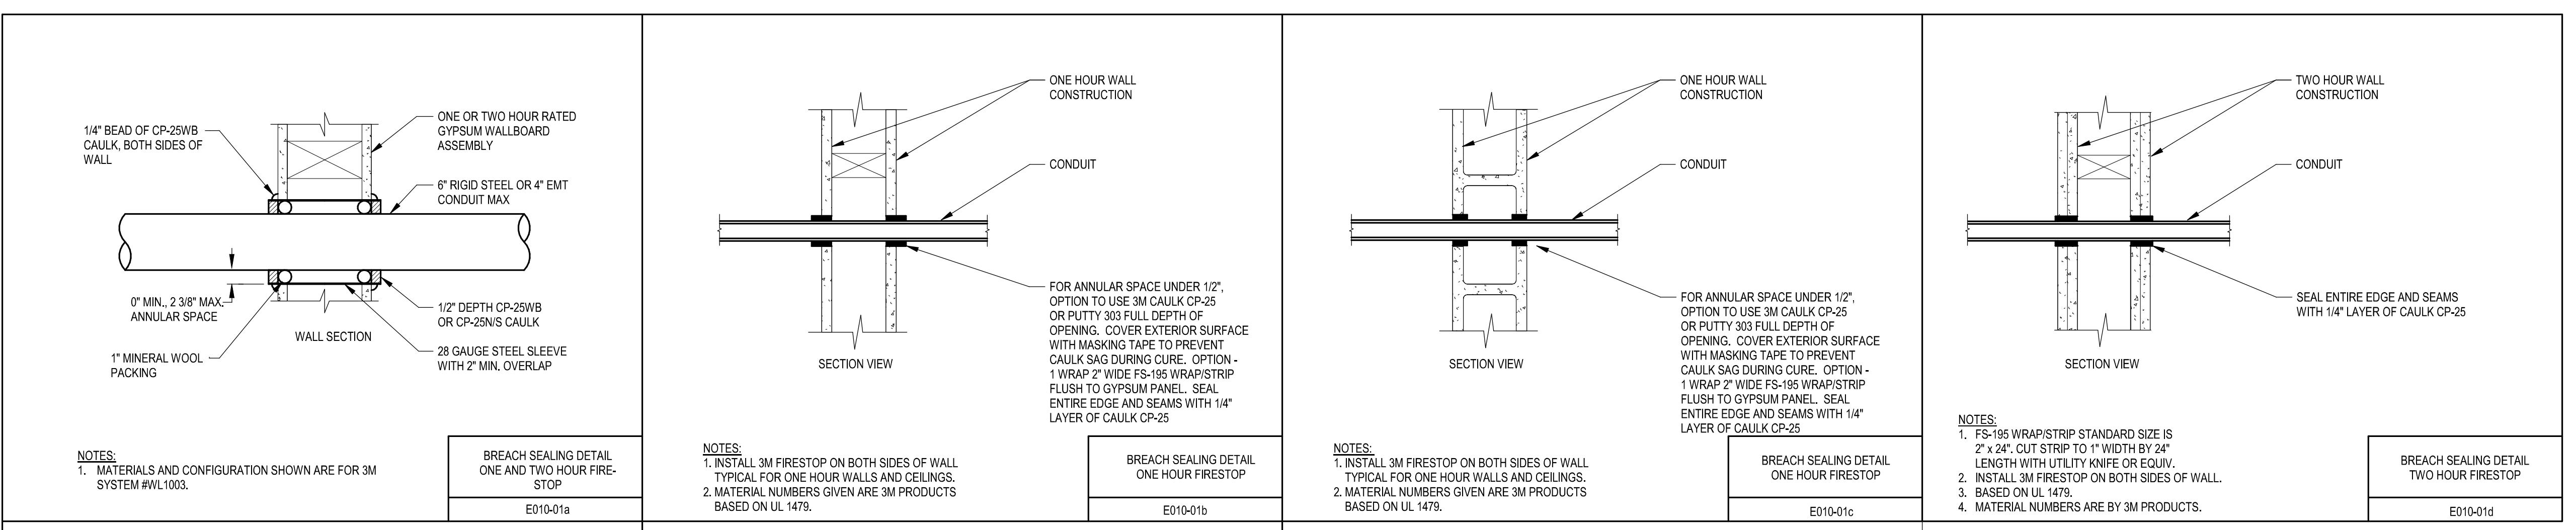





KEYED NOTES	
T-1	DIV.27 INSTALLER TO INSTALL J-HOOK PATHWAY FROM CONDUIT STUB-OUTS TO EQUIPMENT RACK.
T-2	DIV.28 INSTALLER TO INSTALL 1" TO 4" SQUARE BACKBOX AT NOTED LEVEL AND ROTATE COVER WITH BLANK COVERPLATE.
T-3	DIV.28 INSTALLER TO MOUNT THE CAMERA ON TOP OF THE OWNERS FURNACE AND ROTATE CAMERA 90 DEGREES TO DIRECTION WHERE THE MAIN UNIT WILL BE INSTALLED. COORDINATE WITH OWNER FOR INSTALLATION.
T-4	DIV.29 INSTALLER TO MOUNT CABLE MANAGEMENT STRUCTURE WITHIN 5 FEET OF CONDUIT SERVICING CAMERA LOCATION.
T-5	DIV.28 INSTALLER TO INSTALL A HORIZONTAL PLATE OVER J-BOX OPENING.
T-6	DIV.27 AV INSTALLER SHALL COORDINATE ROUGH-IN AND BACKBOX NEEDS WITH DIV.26 INSTALLER.

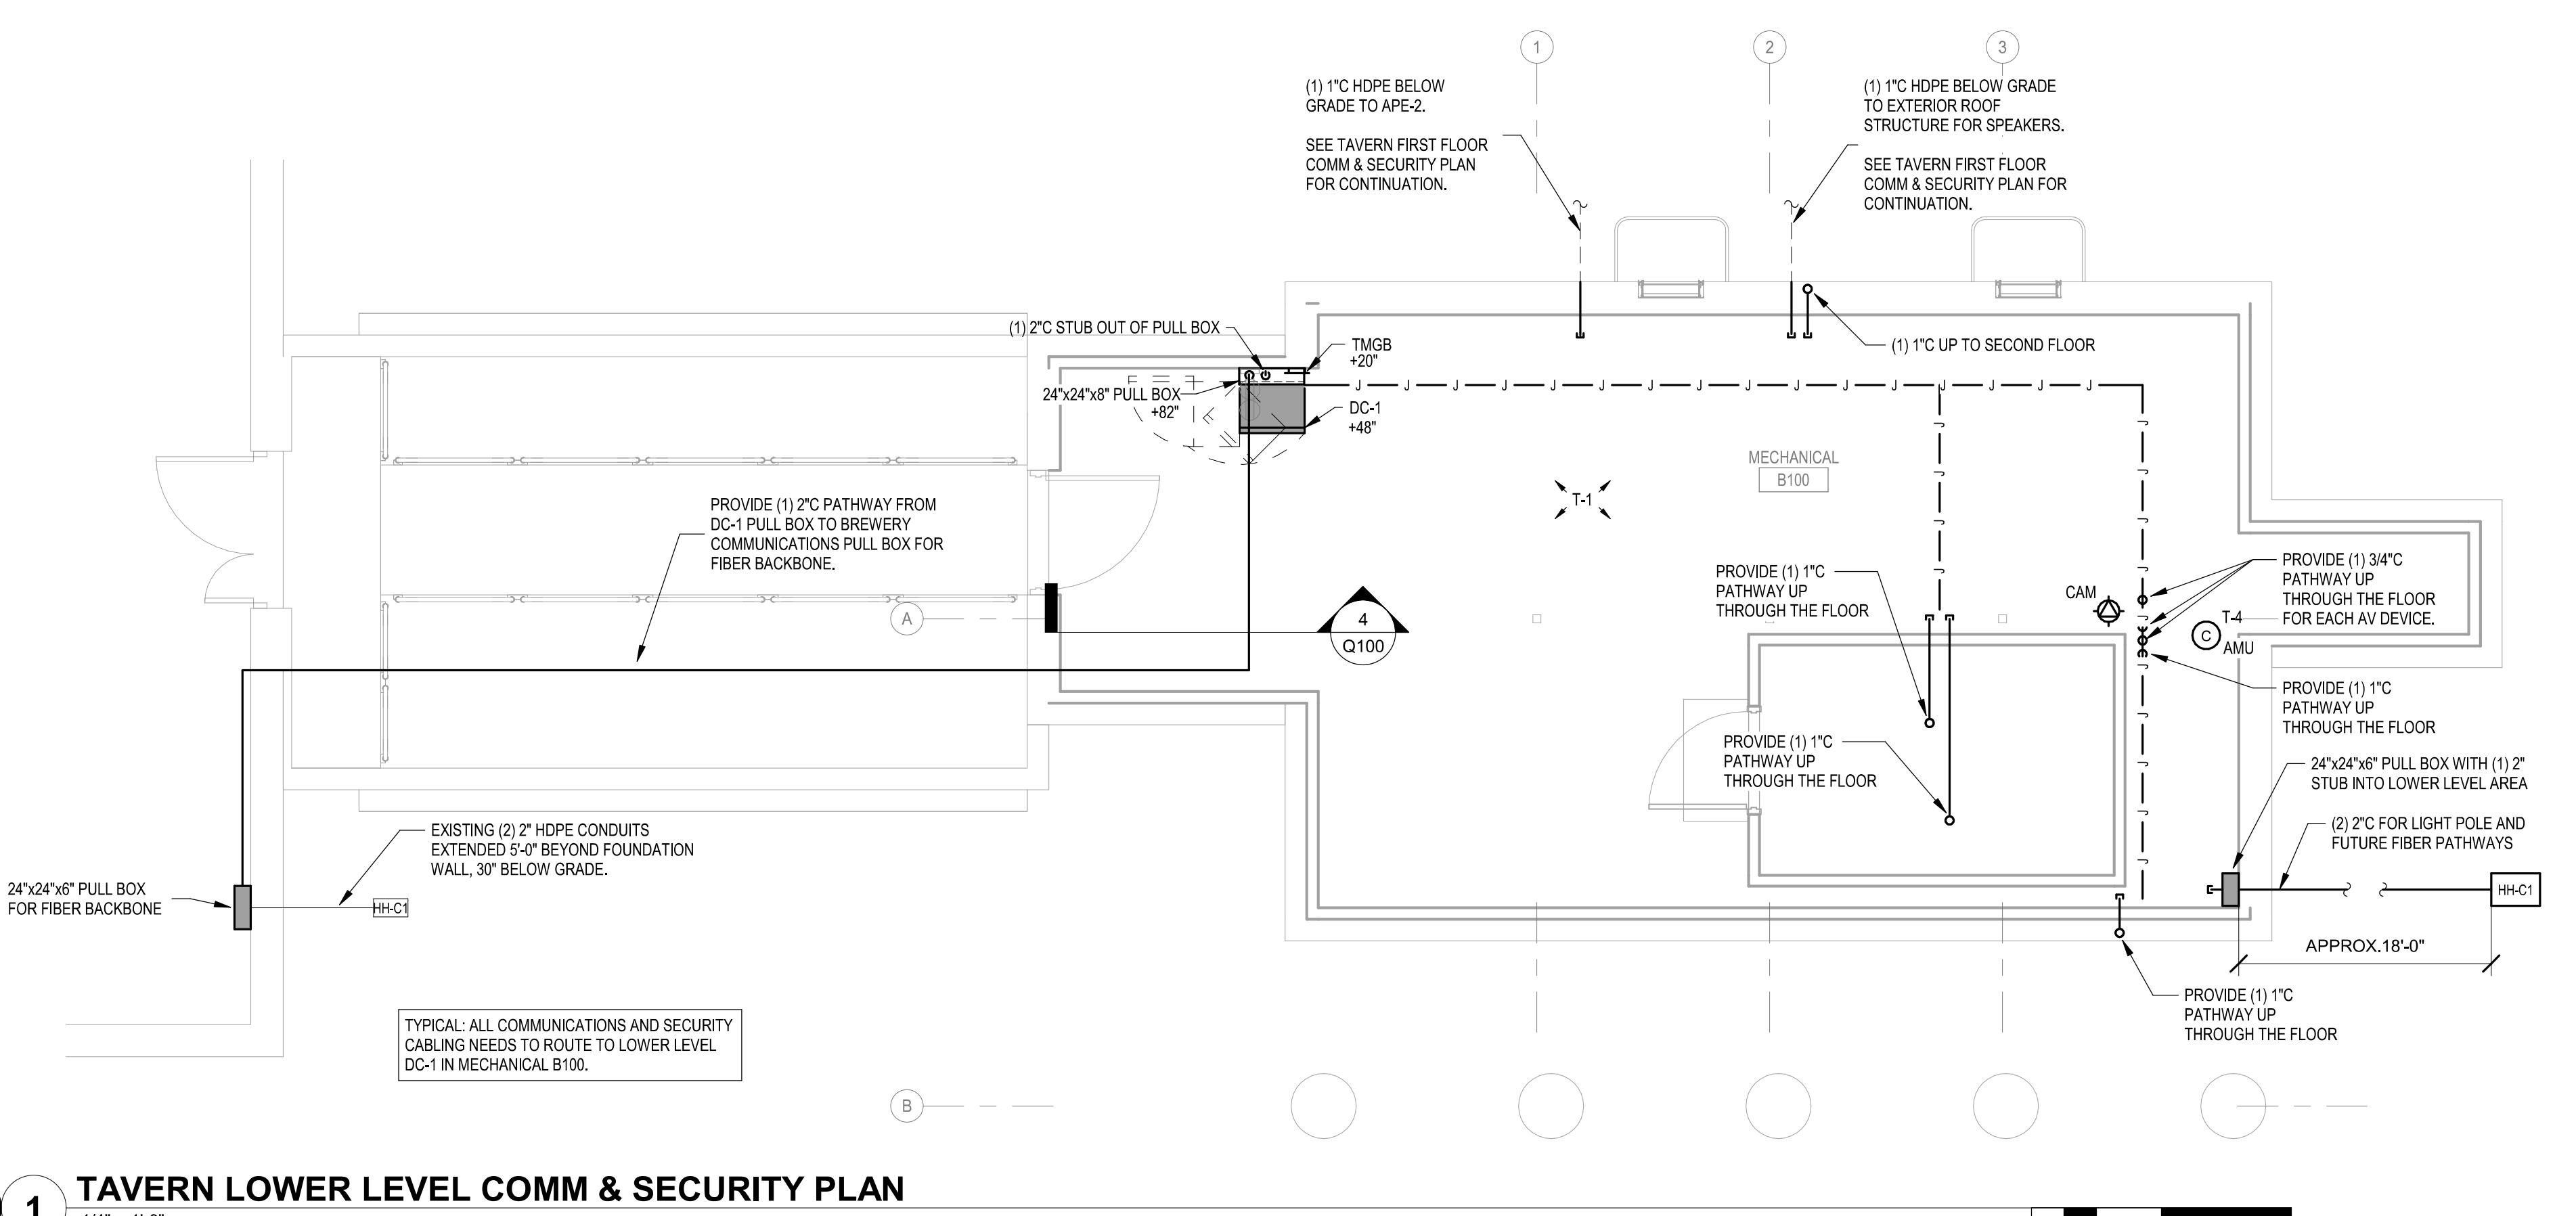


NORTH
1 TAVERN LOWER LEVEL COMM & SECURITY PLAN

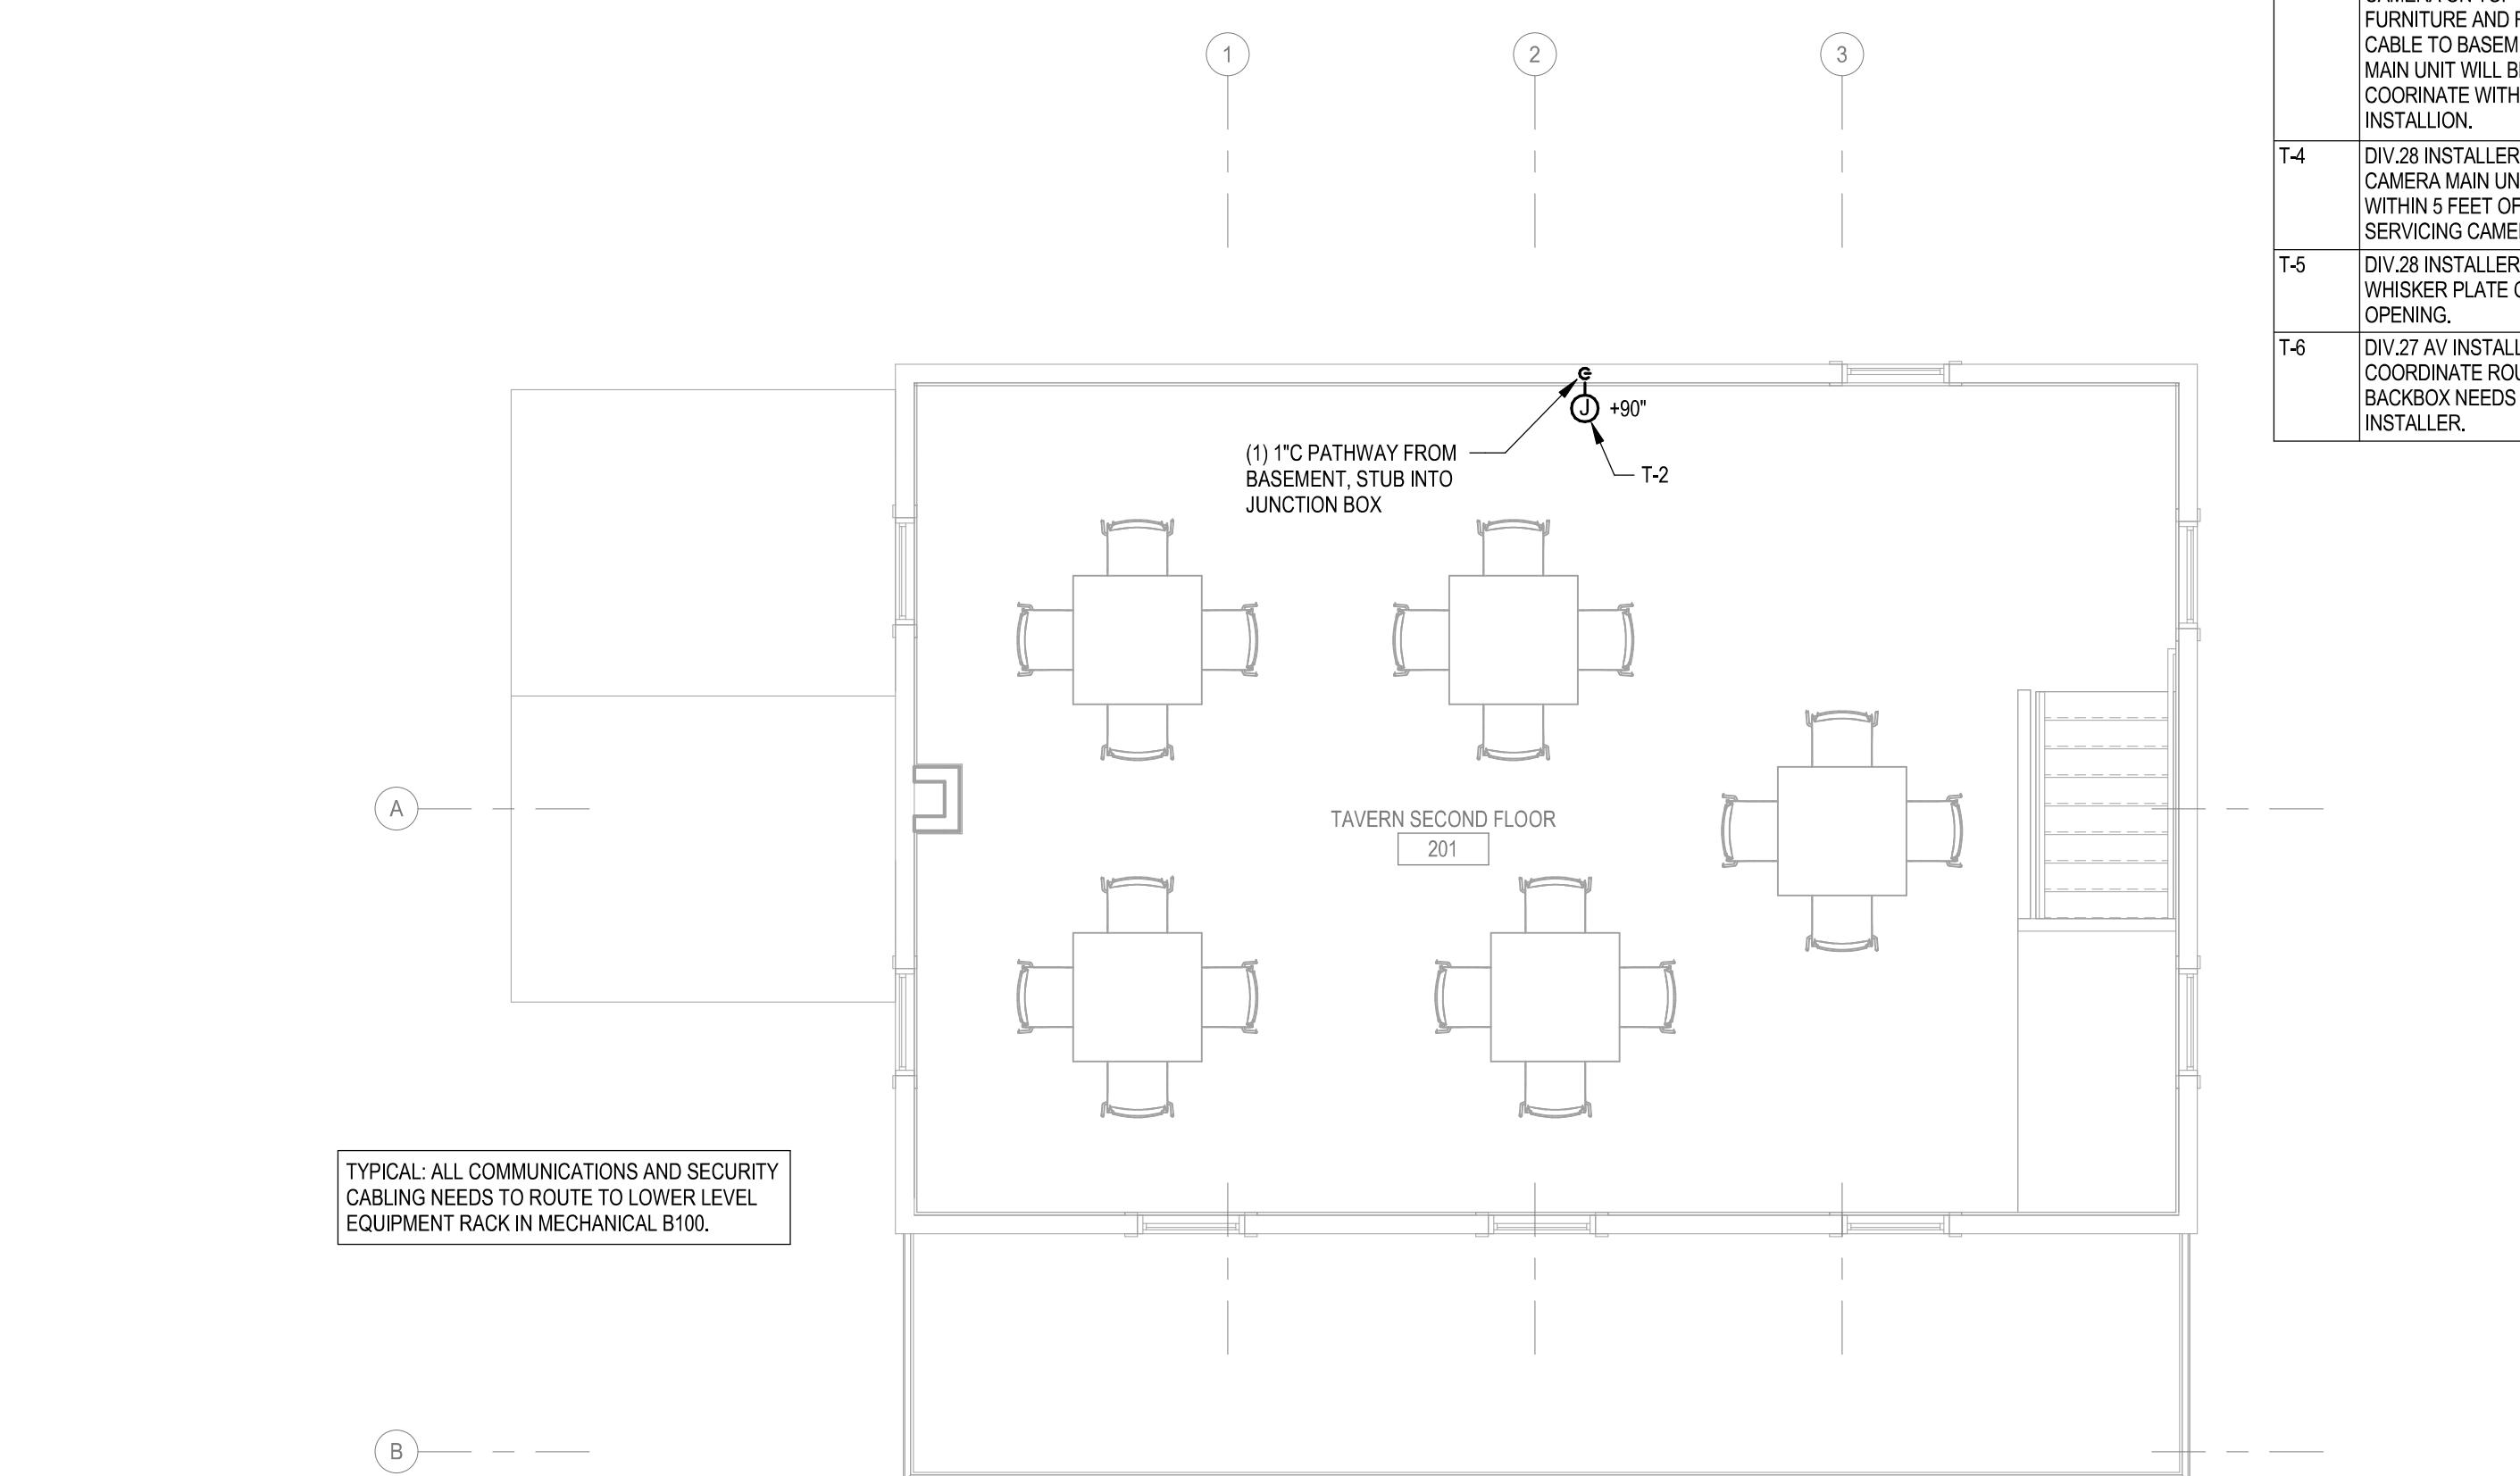

NORTH
3 TAVERN SECOND FLOOR COMM & SECURITY PLAN

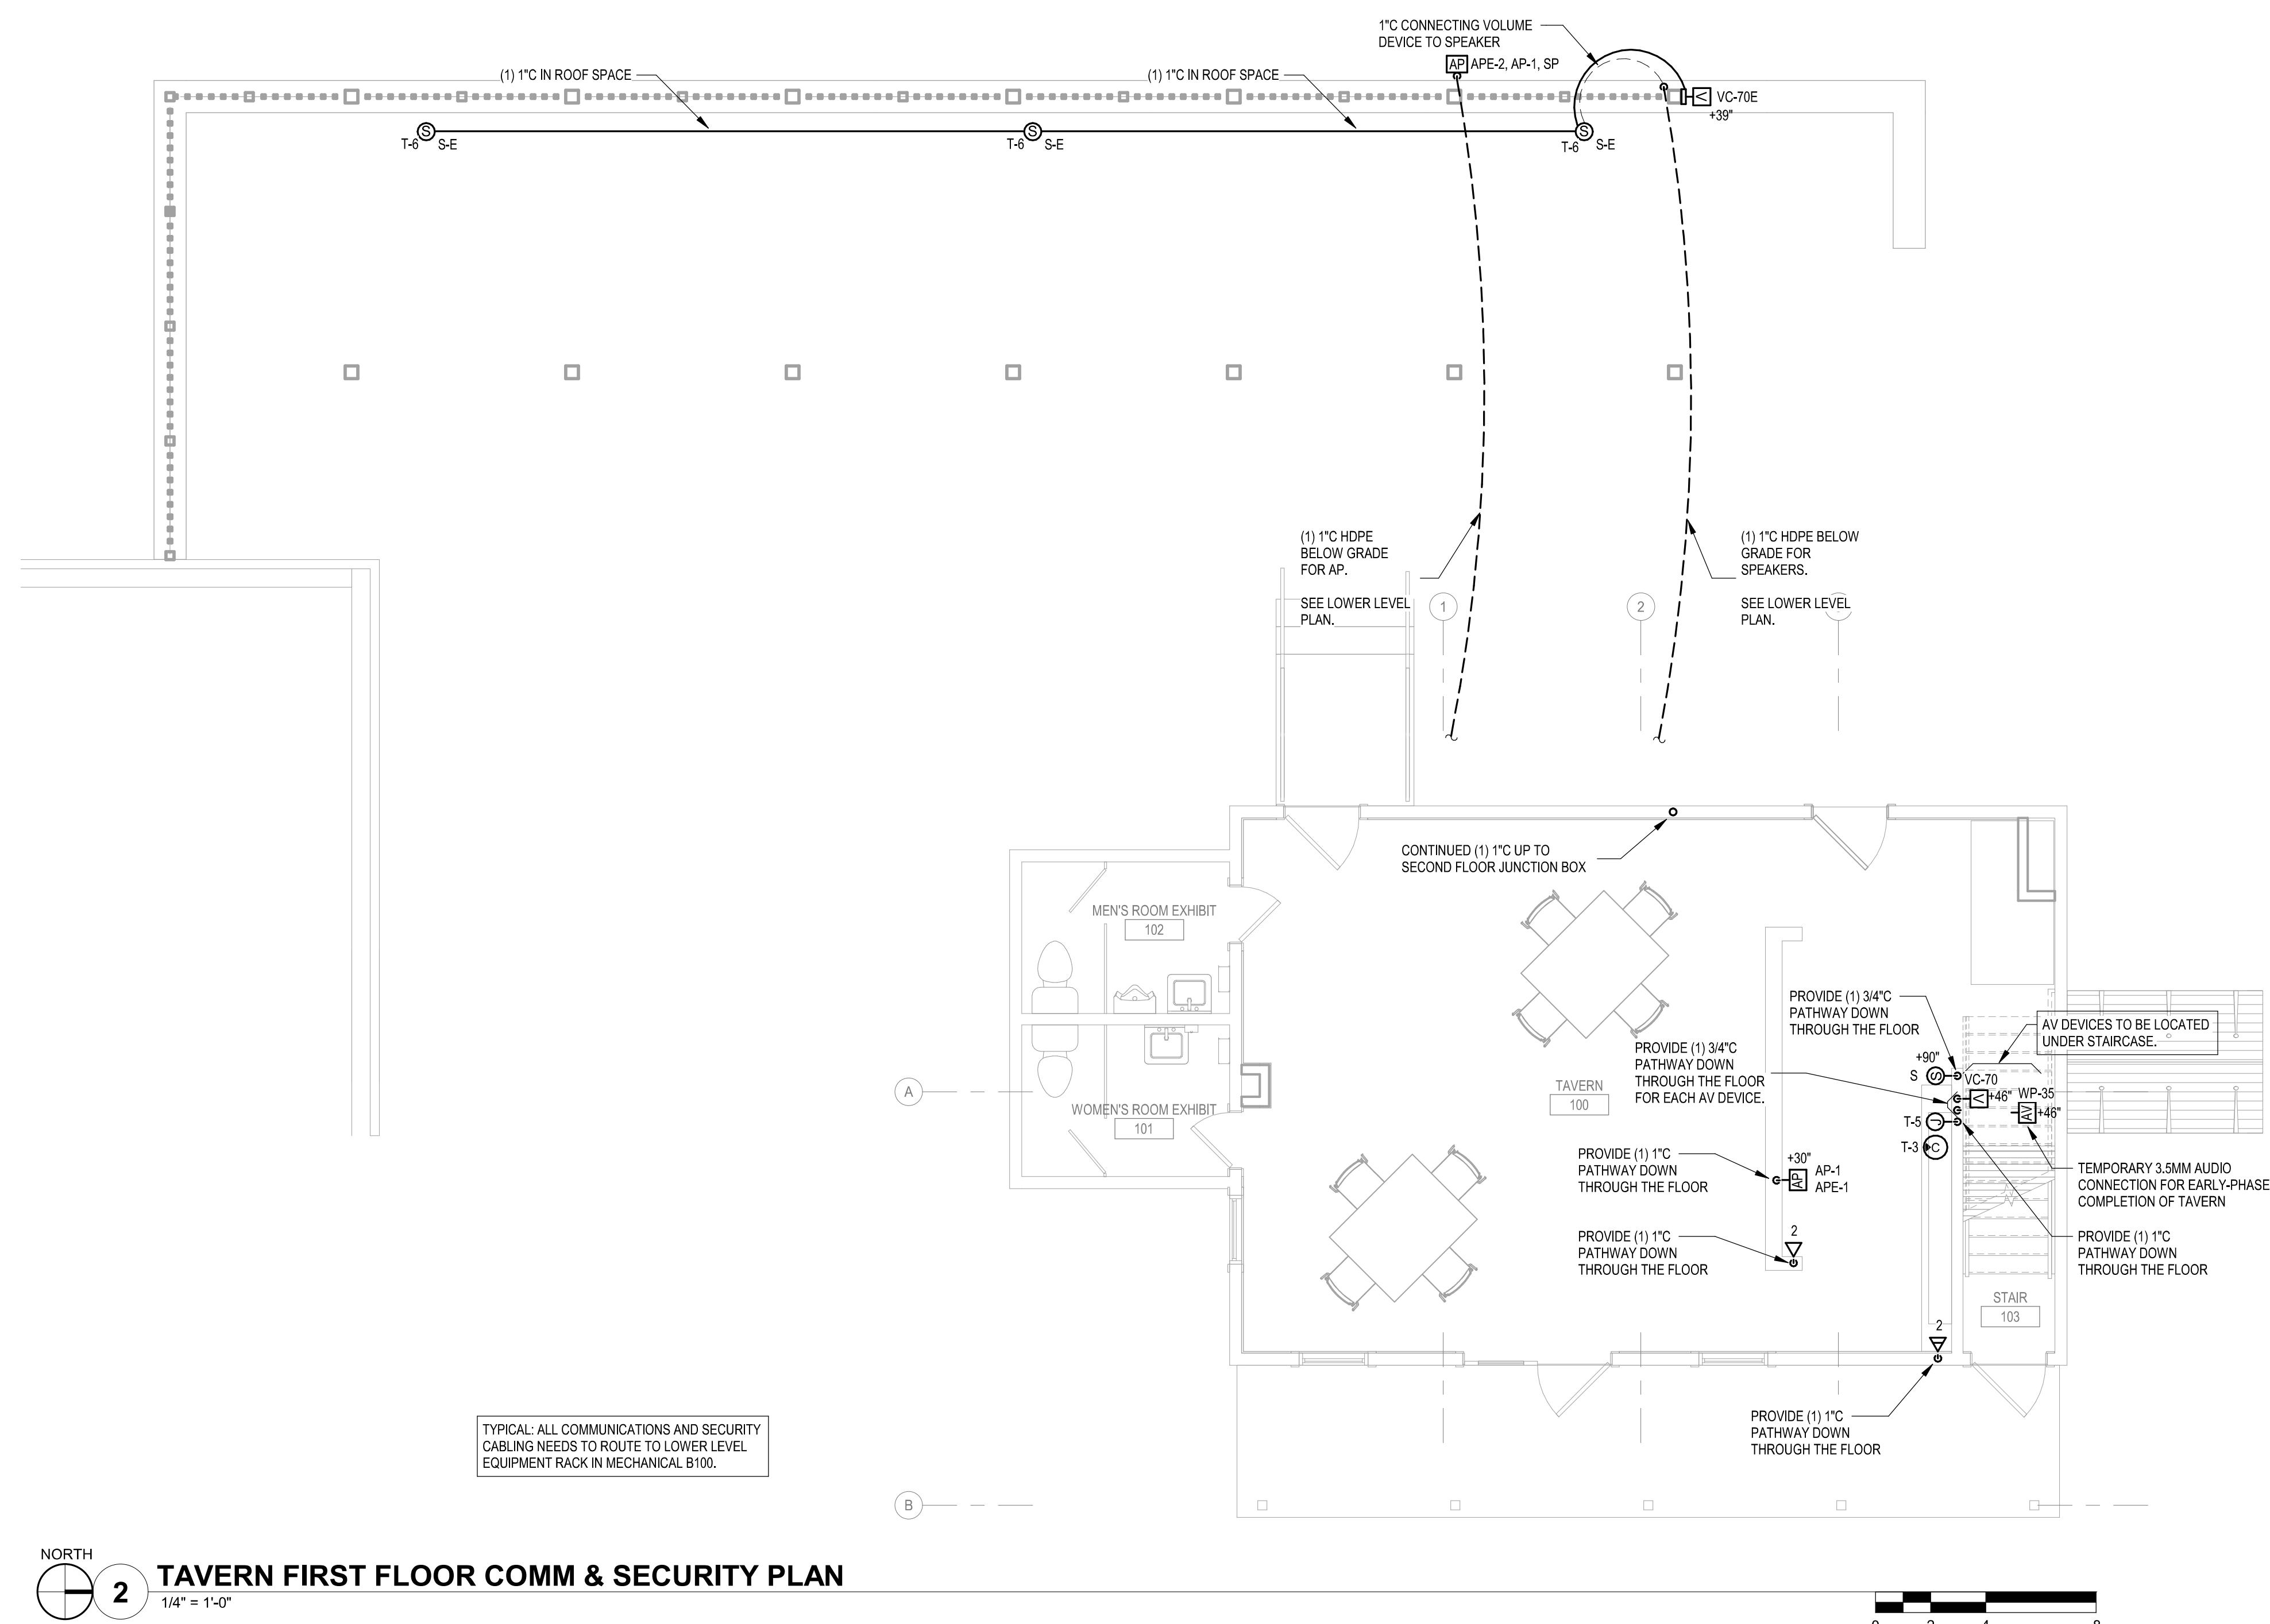

NORTH
2 TAVERN FIRST FLOOR COMM & SECURITY PLAN

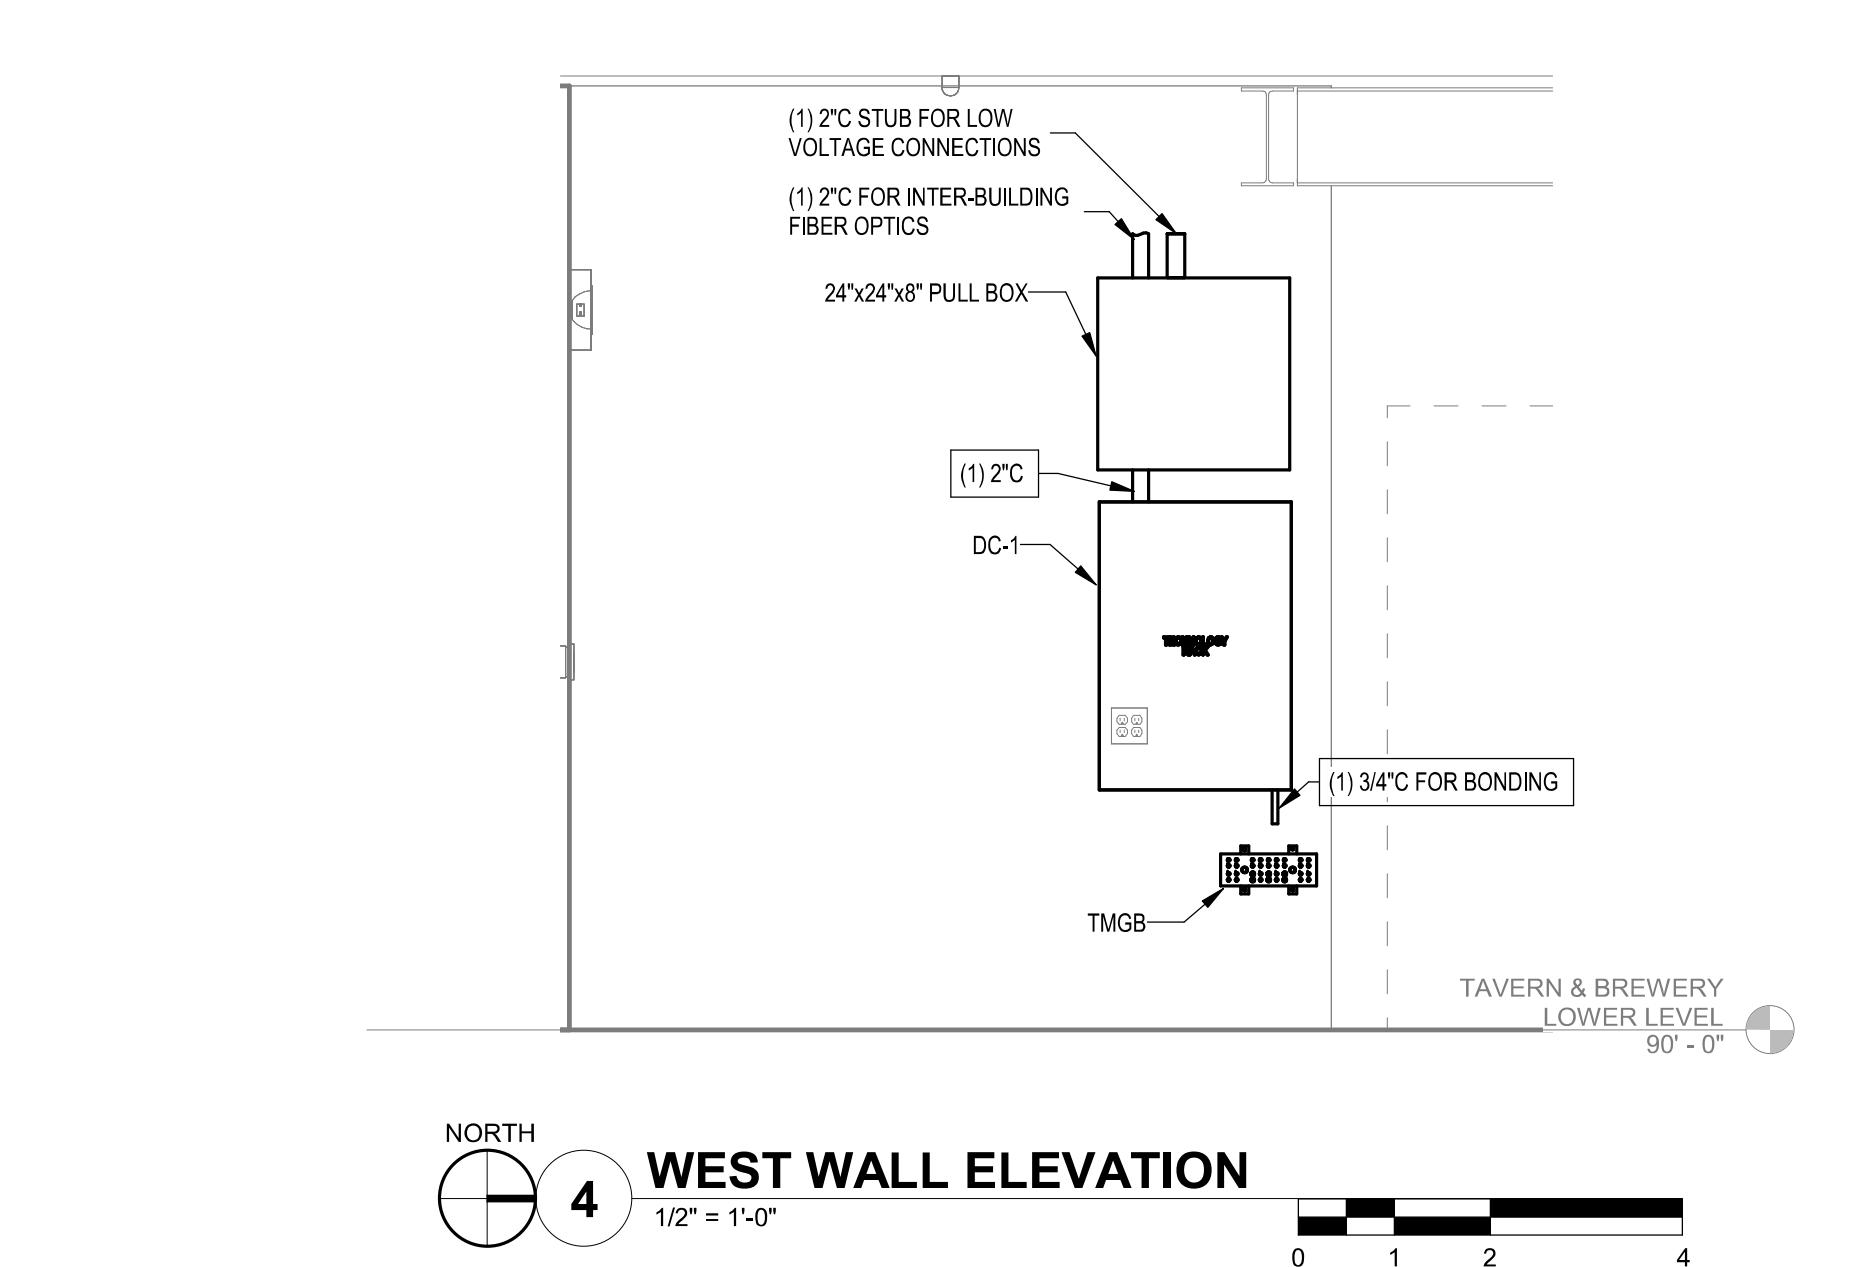

NORTH
4 WEST WALL ELEVATION

HAND HOLE SCHEDULE						
PLAN MARK	SIZE	DEPTH	TIER	COVER IDENTIFICATION	COVER CONSTRUCTION	ASSEMBLY CONSTRUCTION
HH-C1	24x36	30	8	COMMUNICATIONS	SKID RESISTANT SURFACE. (2) PULL SLOTS	POLYMER CONCRETE, STACKABLE
NOTES						
1. OPEN BOTTOM WITH MOUSE HOLES 2. REFER TO SPECIFICATION 26.05.33 RACEWAY AND BOXES FOR ELECTRICAL SYSTEMS FOR ADDITIONAL INFORMATION						

State of Wisconsin
Department of Administration
Division of Facilities Development

Old World Wisconsin Ethnic Outdoor Museum
Town of Eagle, Wisconsin



Tavern Renovations
Old World Wisconsin Ethnic Outdoor Museum
Wisconsin Historical Society
Town of Eagle, Wisconsin

Sheet Title: TAVERN COMM & SECURITY PLANS

Revisions:

No. Date: Description:

Graphic Scale	See Details
DFD Number	171K-04
Set Type	BD
Date Issued	9/8/2023
Sheet Number	Q100